

CURRENT APPLICABLE CODES

LIFE SAFETY CODE NFPA 101

LIFE SAFETY CODE 2018 EDITION
WITH 2020 GEORGIA STATE FIRE MARSHAL AMENDMENTS

GEORGIA STATE MINIMUM STANDARD BUILDING CODE

INTERNATIONAL BUILDING CODE, 2018 EDITION
WITH GEORGIA AMENDMENTS (2020)INTERNATIONAL RESIDENTIAL CODE, 2018 EDITION
WITH GEORGIA AMENDMENTS (2020)

GEORGIA STATE MINIMUM STANDARD FIRE CODE

INTERNATIONAL FIRE CODE, 2018 EDITION

GEORGIA STATE MINIMUM STANDARD PLUMBING CODE

INTERNATIONAL PLUMBING CODE, 2018 EDITION,
WITH GEORGIA AMENDMENTS (2020)

GEORGIA STATE MINIMUM STANDARD MECHANICAL CODE

INTERNATIONAL MECHANICAL CODE, 2018 EDITION
WITH GEORGIA AMENDMENTS (2020)

GEORGIA STATE MINIMUM STANDARD GAS CODE

INTERNATIONAL FUEL GAS CODE, 2018 EDITION,
WITH GEORGIA AMENDMENTS (2020)

GEORGIA STATE MINIMUM STANDARD ELECTRICAL CODE

NATIONAL ELECTRICAL CODE, 2020 EDITION

GEORGIA STATE MINIMUM STANDARD ENERGY CODE

INTERNATIONAL ENERGY CONSERVATION CODE, 2015 EDITION
WITH GEORGIA AMENDMENTS (2020)

GEORGIA STATE MINIMUM FIRE SAFETY STANDARDS 12-3-3

OCCUPANCY CLASSIFICATION

PRIMARY - LIFE SAFETY CODE NFPA 101

NEW RESIDENTIAL OCCUPANCY

SUPPLEMENTAL - INTERNATIONAL BUILDING CODE

RESIDENTIAL GROUP R-3 OCCUPANCY

CONSTRUCTION TYPE

PRIMARY - INTERNATIONAL BUILDING CODE

TYPE 5B - UNPROTECTED, COMBUSTIBLE

SINGLE FAMILY HOUSE - 4 BEDROOM 3.5 BATH

404 PEACHTREE CIRCLE
ATLANTA, GA 30318

CONSTRUCTION DOCUMENTS AUGUST 9, 2023

Sheet List	
Sheet Number	Sheet Name
GENERAL	
G000	COVER SHEET
ARCHITECTURE	
A010	SITE PLAN
A100	BASEMENT FLOOR PLAN
A101	FIRST FLOOR PLAN
A102	SECOND FLOOR PLAN
A103	ROOF PLAN
A120	BASEMENT FINISH PLAN
A121	FIRST FLOOR FINISH PLAN
A122	SECOND FLOOR FINISH PLAN
A200	BASEMENT REFLECTED CEILING PLAN
A201	FIRST FLOOR REFLECTED CEILING PLAN
A202	SECOND FLOOR REFLECTED CEILING PLAN
A300	EXTERIOR ELEVATIONS
A301	EXTERIOR ELEVATIONS
A320	BUILDING SECTIONS
A400	ENLARGED FLOOR PLANS
A500	WALL SECTIONS
A501	WALL SECTIONS
A502	WALL SECTIONS
A600	SECTION DETAILS
A601	SECTION DETAILS
A620	PLAN DETAILS
A700	INTERIOR ELEVATIONS
A701	INTERIOR ELEVATIONS
A702	INTERIOR ELEVATIONS
A800	WALL TYPES
A820	DOOR SCHEDULE & TYPES
A840	WINDOW SCHEDULE & TYPES
A860	FINISH SCHEDULE
A900	INTERIOR DETAILS
A901	INTERIOR DETAILS
A902	INTERIOR DETAILS

THE PROJECT CONSISTS OF A NEW SINGLE FAMILY RESIDENTIAL HOUSE OF APPROXIMATELY 2,634 SQ FT LOCATED IN ATLANTA GEORGIA. THE WORK INCLUDES NEW CONSTRUCTION FOR THE ARCHITECTURE, STRUCTURE AND MEP.

THE PROJECT AND CONSTRUCTION DOCUMENTS ARE NOT FOR CONSTRUCTION AND WERE DRAWN FOR THE SOLE PURPOSE OF TESTING THE CAPABILITIES OF AI AND LARGE LANGUAGE MODELS TO DETERMINE IF THE TECHNOLOGY COULD BE USED TO MAKE INFORMATION RETRIEVAL QUICKER.

INTERIOR	CONSTRUCTION
BEDROOMS	STYLE
4	SINGLE FAMILY, CONVENTIONAL ARCHITECTURAL STYLE
BATHROOMS	MATERIAL INFORMATION
3 1/2	STICK FRAME CONSTRUCTION MATERIALS SHINGLE ROOF SIDING BRICK
BASEMENT	UTILITIES
FINISHED	PUBLIC SEWER PUBLIC WATER ELECTRICITY: OTHER ENERGY EFFICIENT APPLIANCES AND THERMOSTAT
HEATING	
CENTRAL	
COOLING	
CENTRAL	
APPLIANCES	
DISHWASHER, DRYER, FREEZER, GARBAGE DISPOSAL, MICROWAVE, RANGE/OVEN, REFRIGERATOR, WASHER, DRYER	
INTERIOR FEATURES	
INSULATED WINDOWS, PLANTATION SHUTTERS, BOOKCASES DOUBLE VANITY, HIGH CEILINGS 9FT MAIN, FIREPLACE, NO COMMON WALLS	
PROPERTY	
PARKING	
FOUR TOTAL SPACES, GARAGE ATTACHED, OFF-STREET	
EXTERIOR FEATURES	
FRONT PORCH PORTICO, BACK DECK, FENCED	
LOT	
LOT SIZE: 5,662 SQ FT	

WILLCIOFFI

 770 Peachtree St NW
Atlanta, GA 30308
willcioffi.com

 Architect: Will Cioffi, AIA
770 Peachtree St NW
Atlanta, GA 30308
hey@willcioffi.com

 NOT FOR
CONSTRUCTION

**SINGLE FAMILY HOUSE
4 BEDROOM 3.5 BATH**
CIOFFI FAMILY
404 PEACHTREE CIRCLE
ATLANTA, GA 30318

 Project number 2023.001
Issue Date 09.06.23
CONSTRUCTION DOCUMENTS
 Revisions
No. Description Date

Scale



As Indicated

COVER SHEET


G000

Architect: Will Cioffi, AIA
 770 Peachtree St NW
 Atlanta, GA 30308
 hey@willcioffi.com

SITE PLAN LEGEND

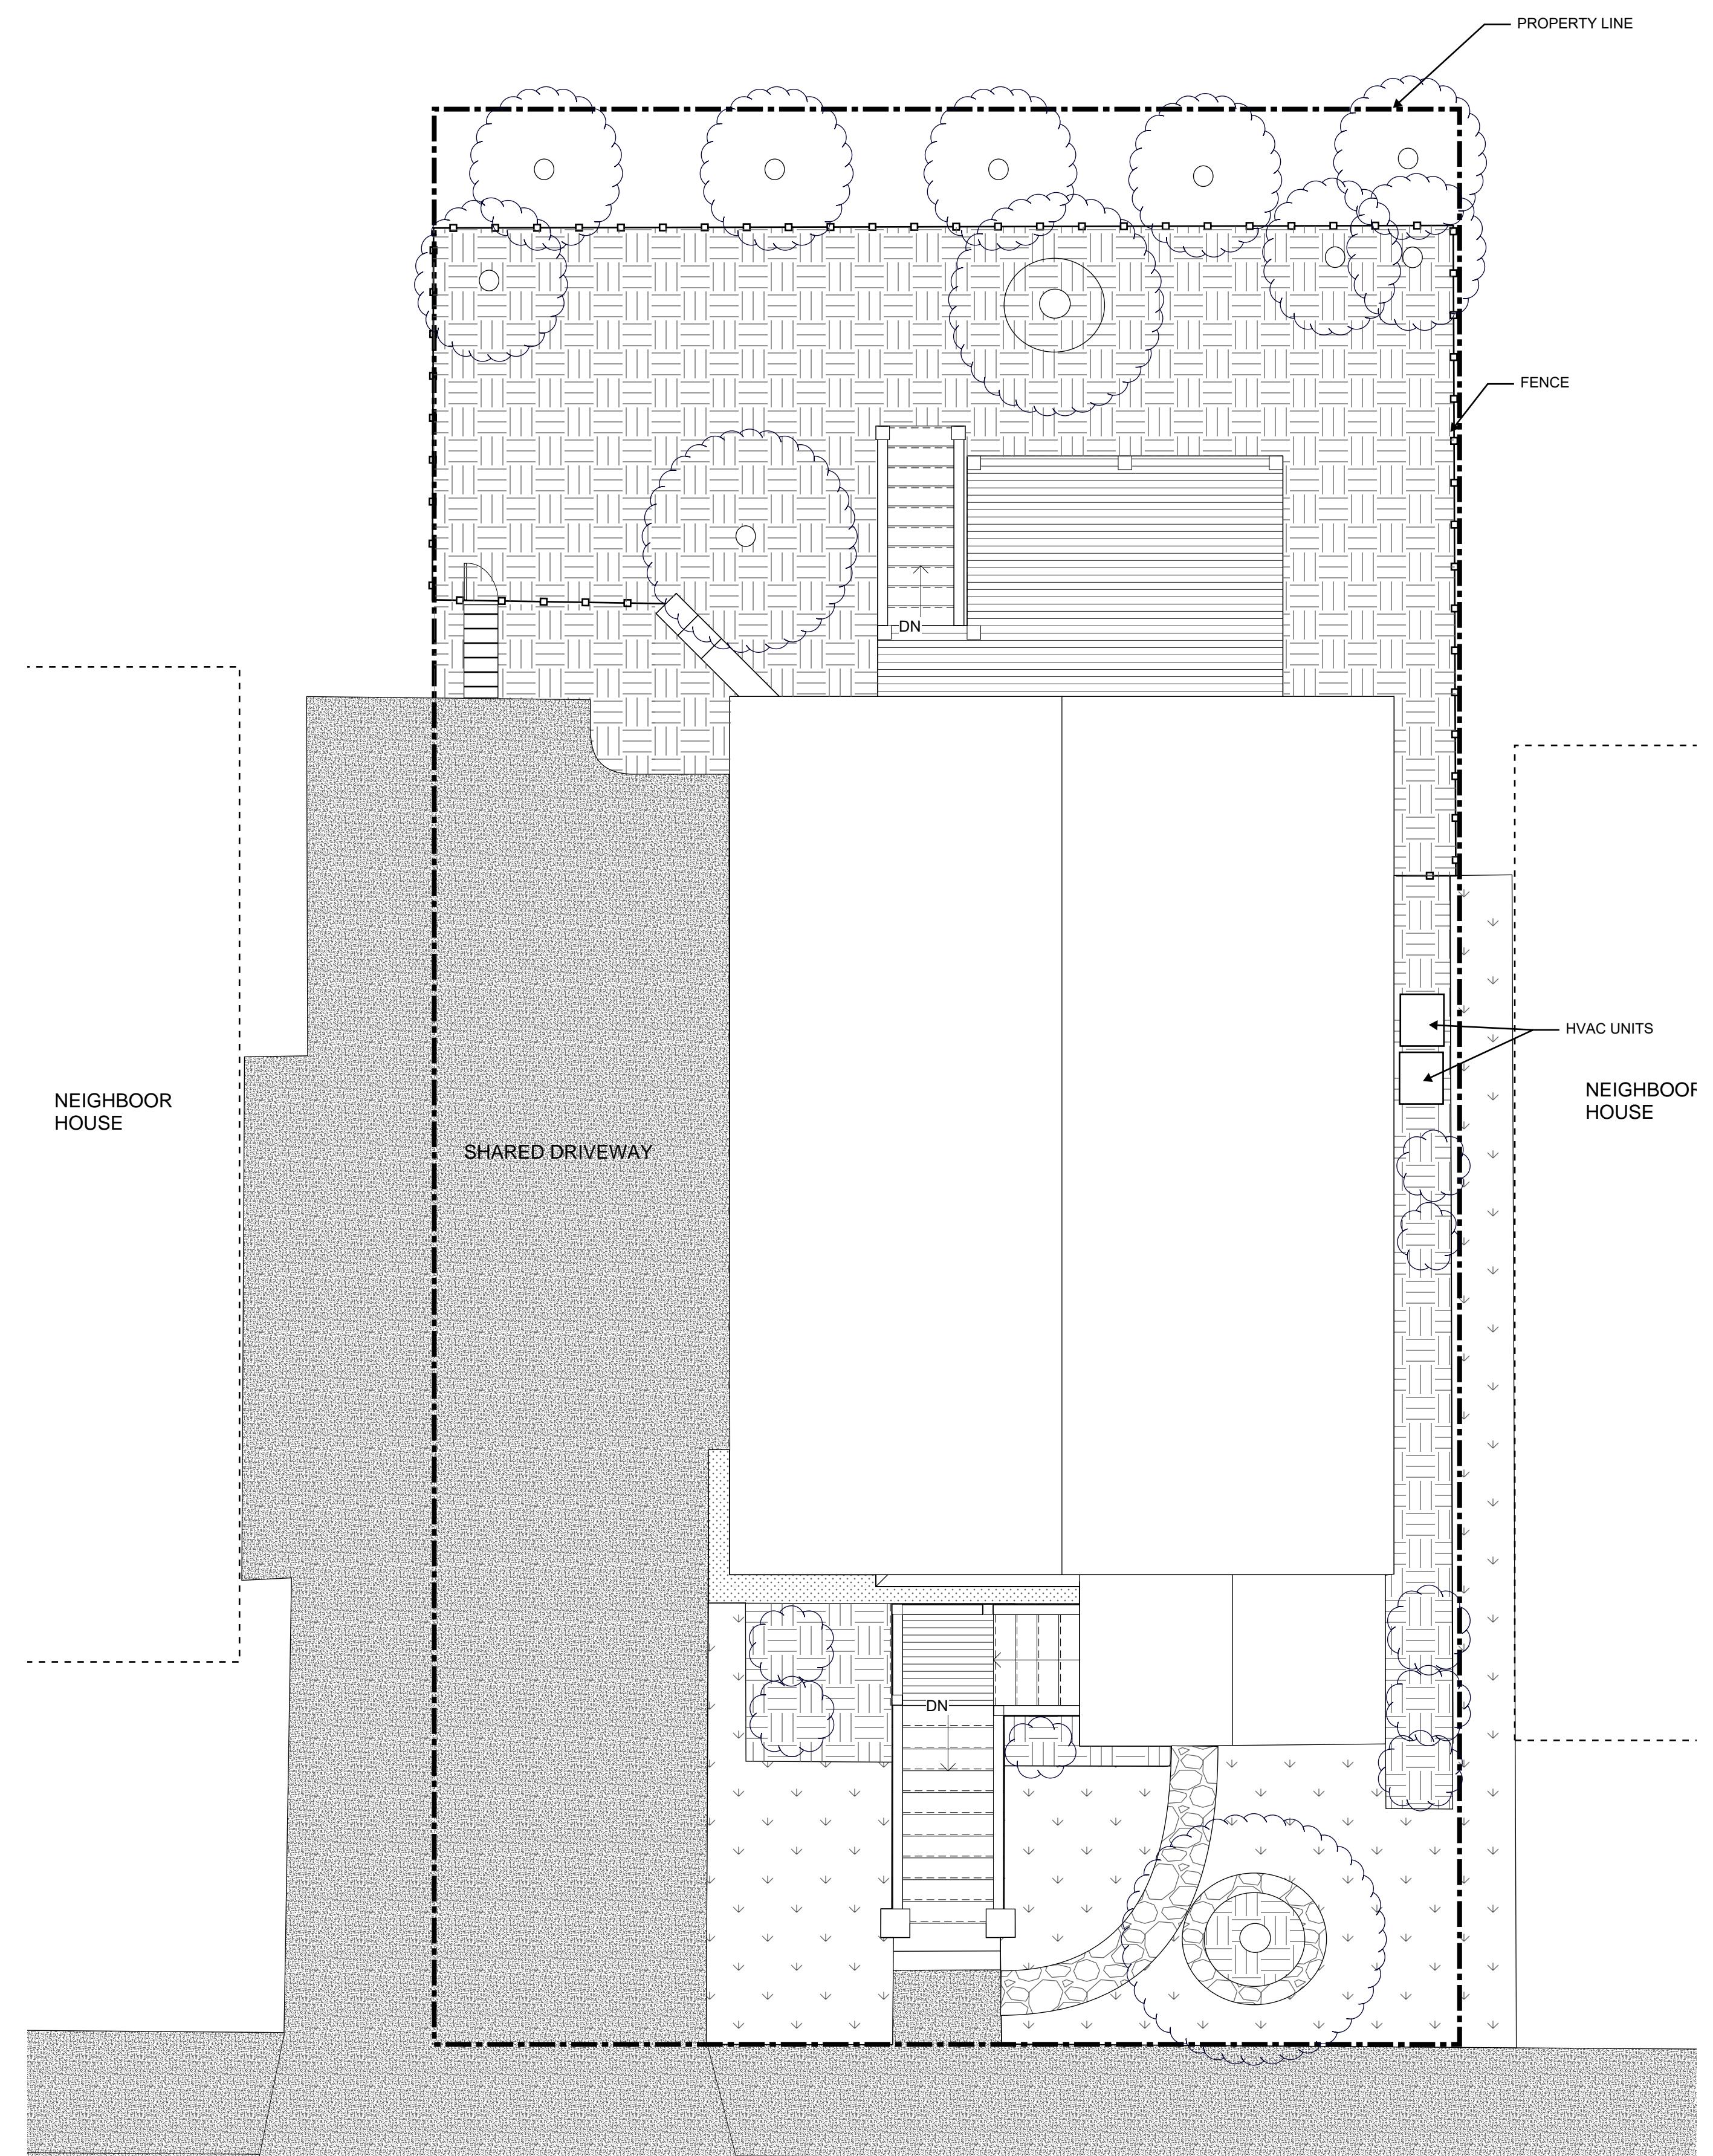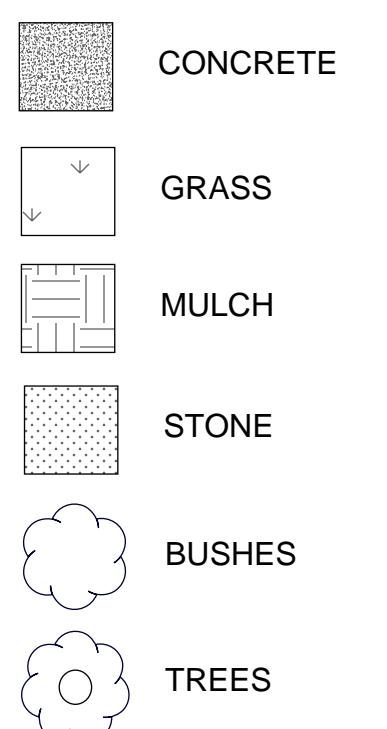

Architect Seal

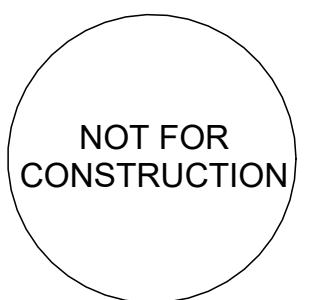

**SINGLE FAMILY HOUSE
4 BEDROOM 3.5 BATH**

CIOFFI FAMILY
 404 PEACHTREE CIRCLE
 ATLANTA, GA 30318

Project number 2023.001
 Issue Date 09.06.23

CONSTRUCTION DOCUMENTS


Revisions
 No. Description Date


SITE PLAN

A010

Scale


As Indicated

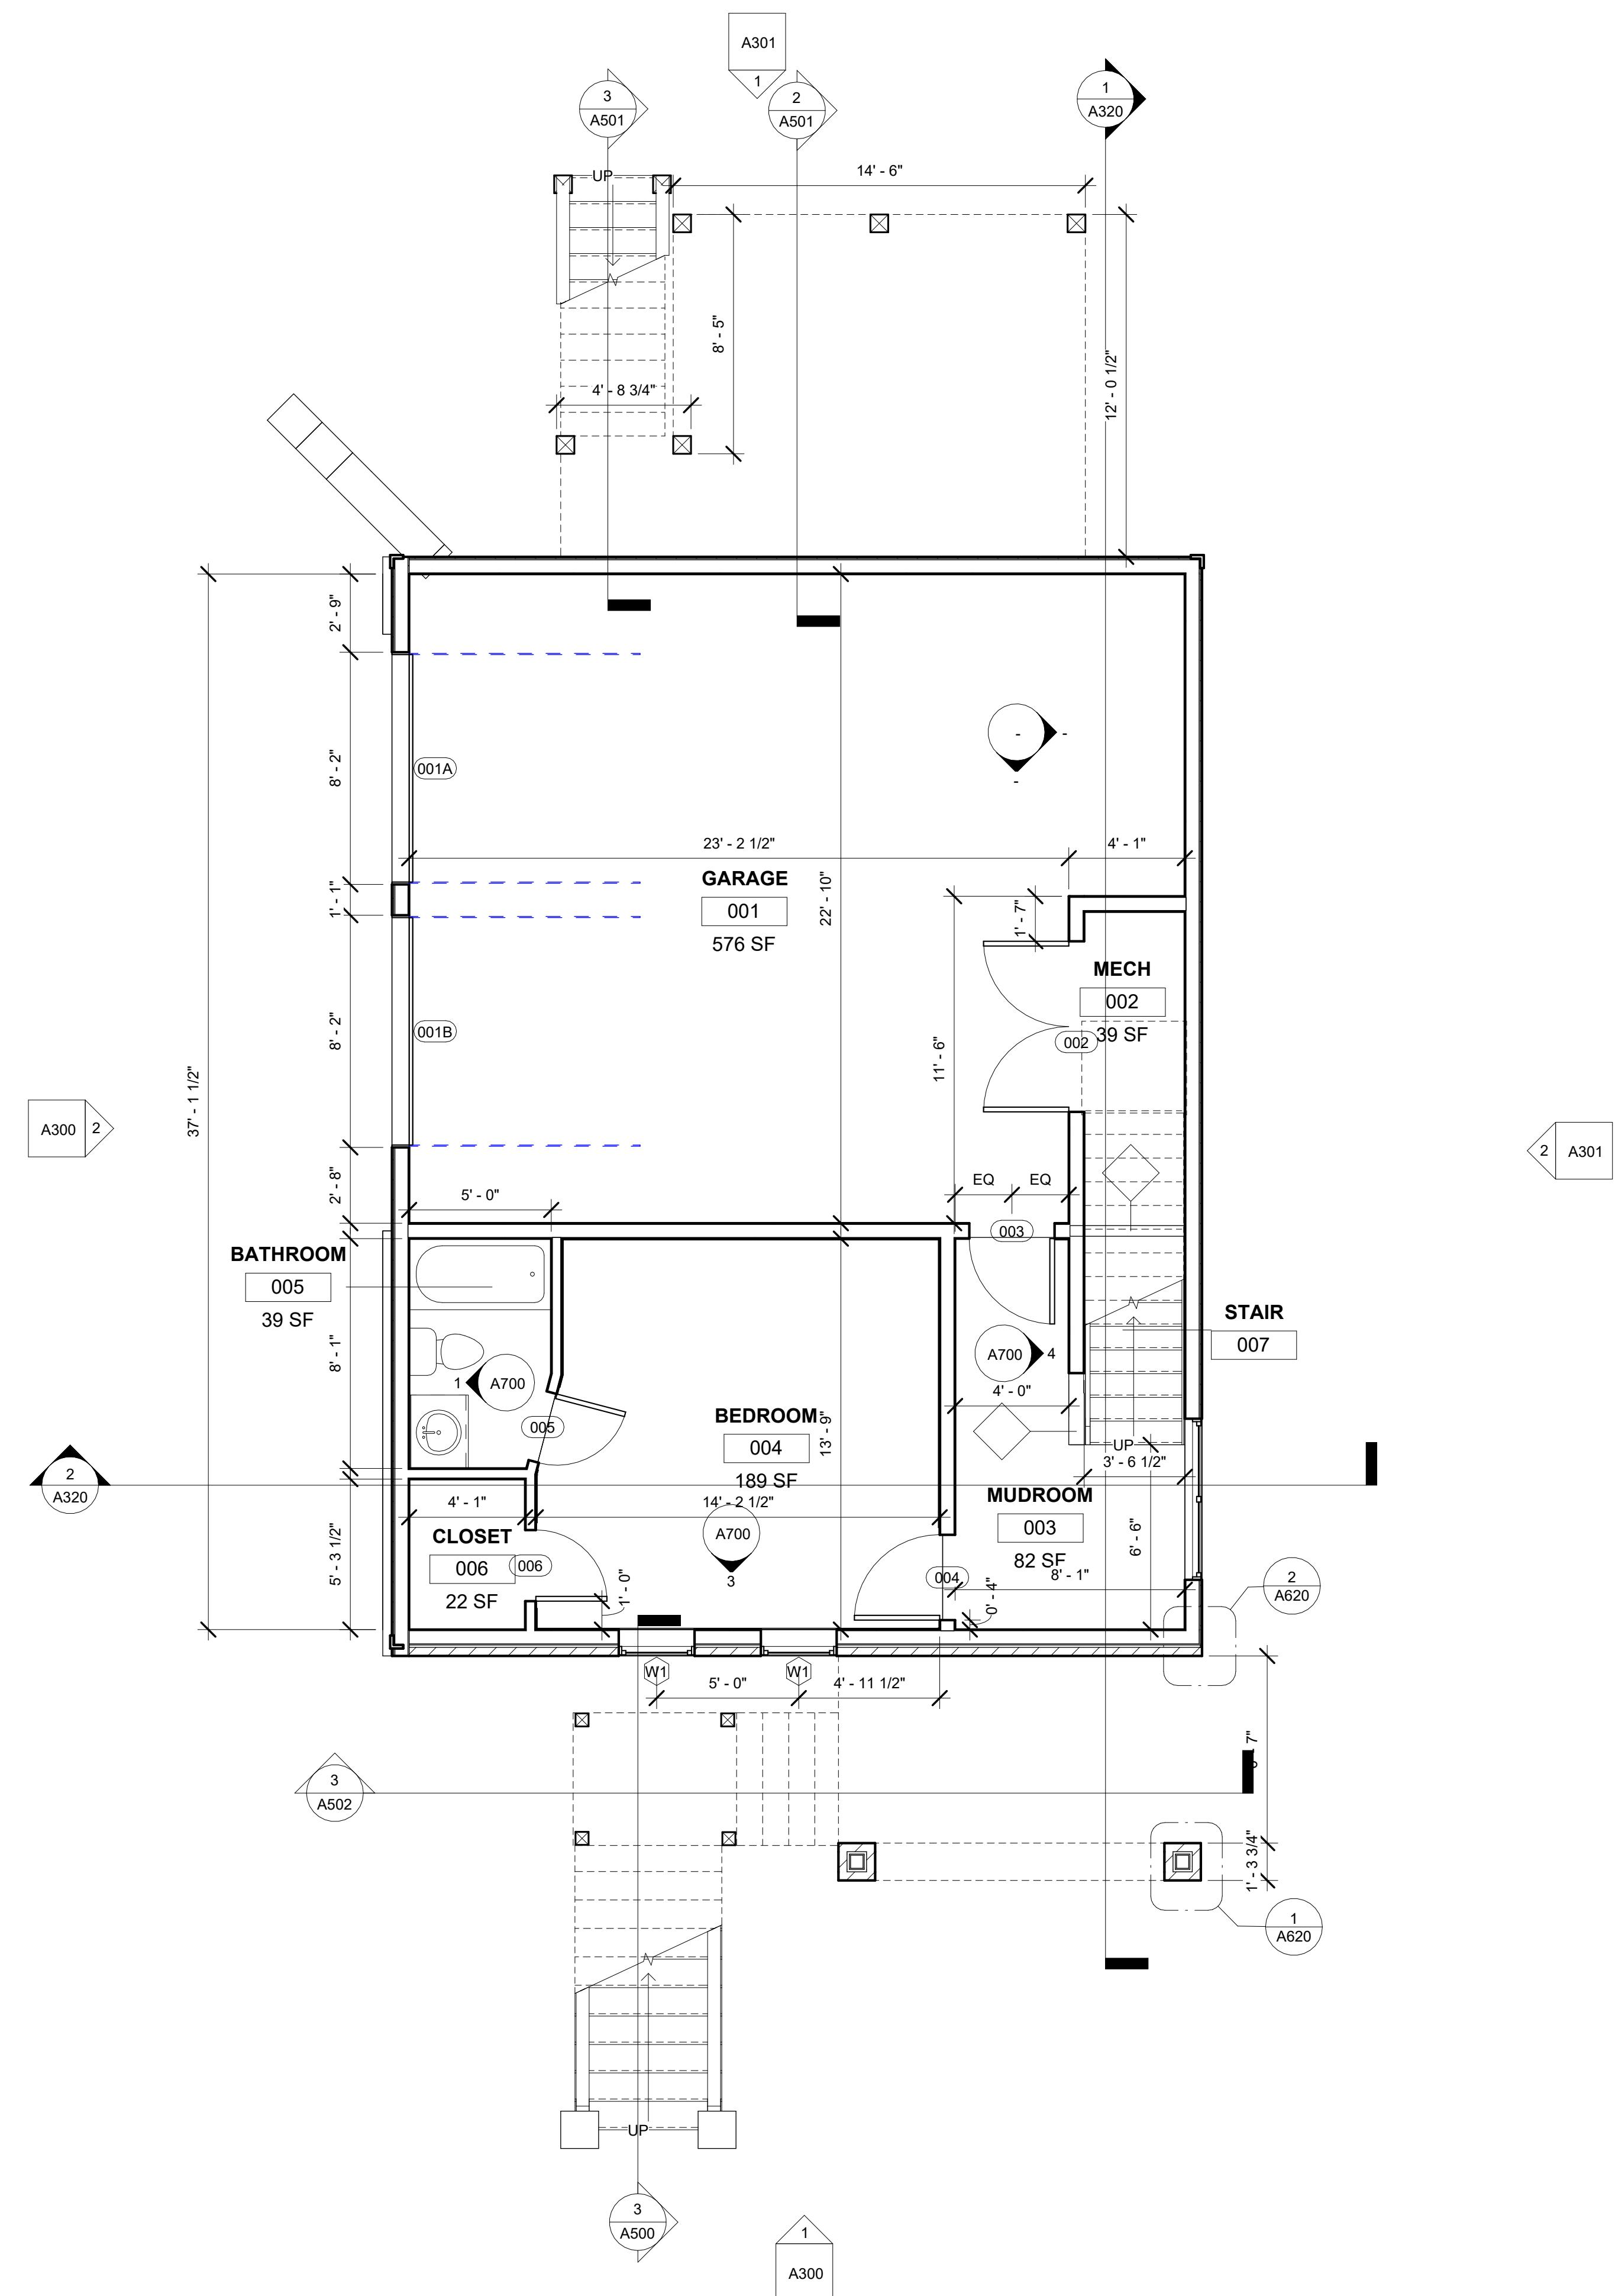

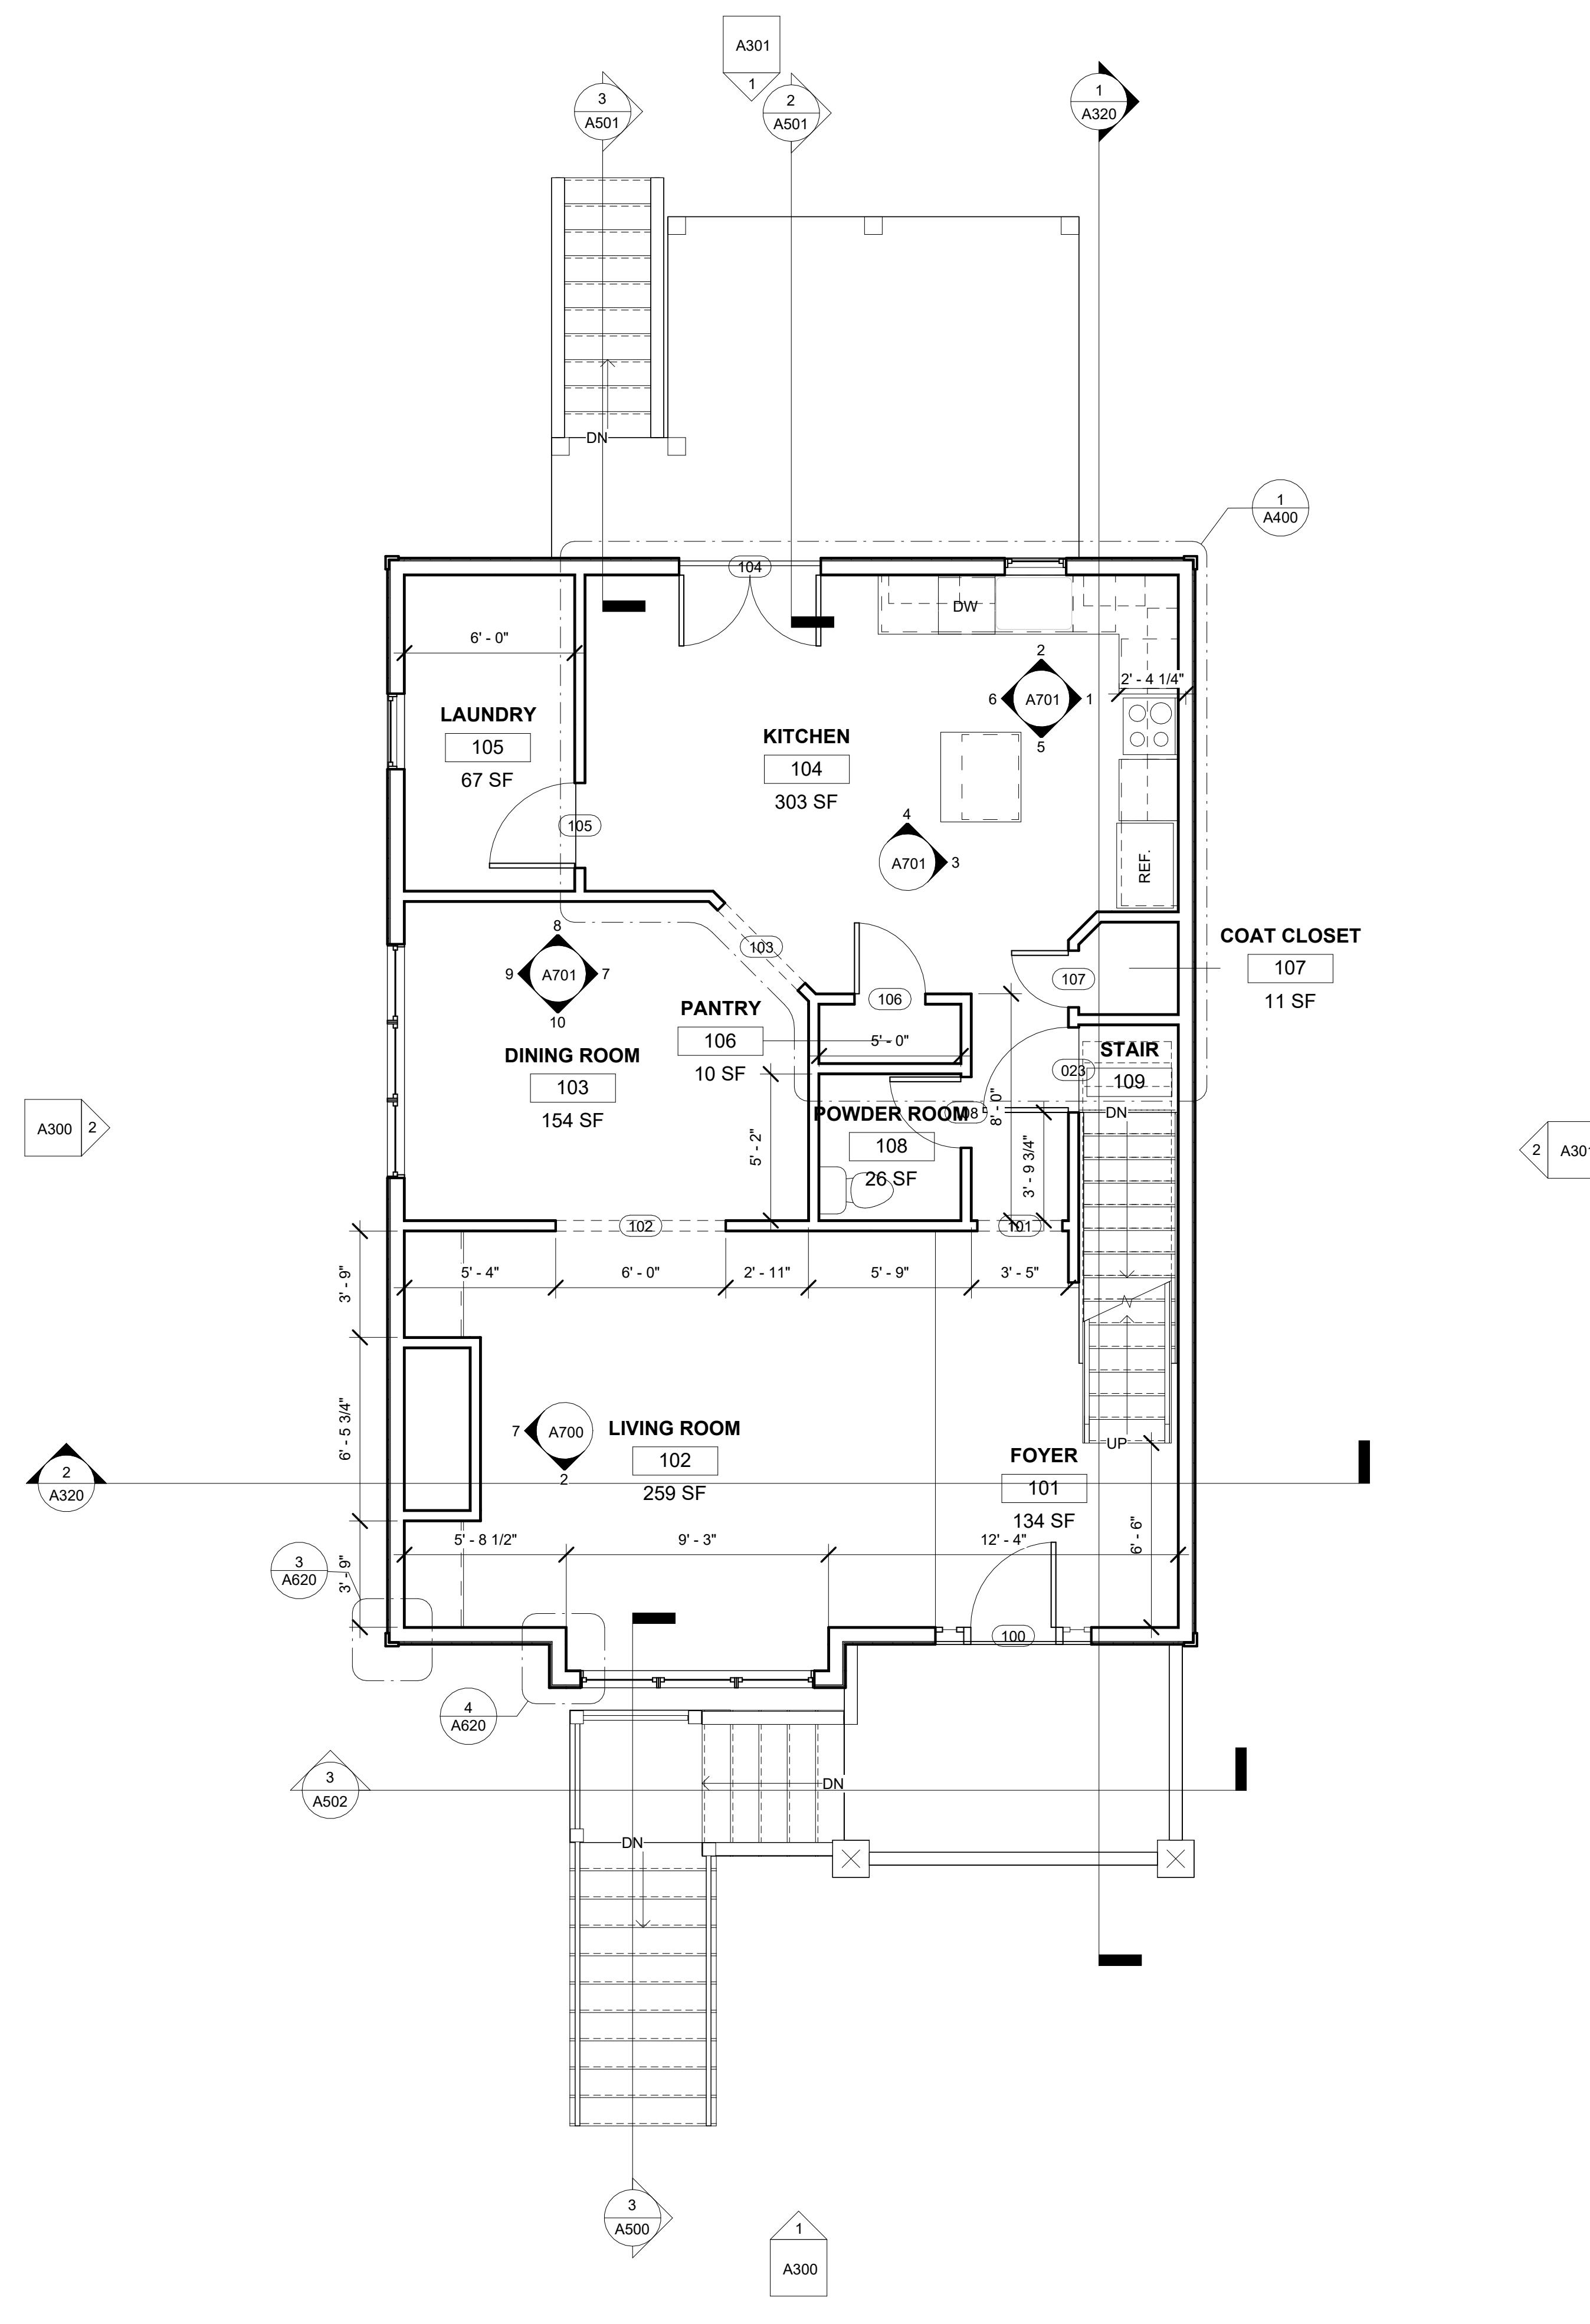

FIRST FLOOR PLAN

A101

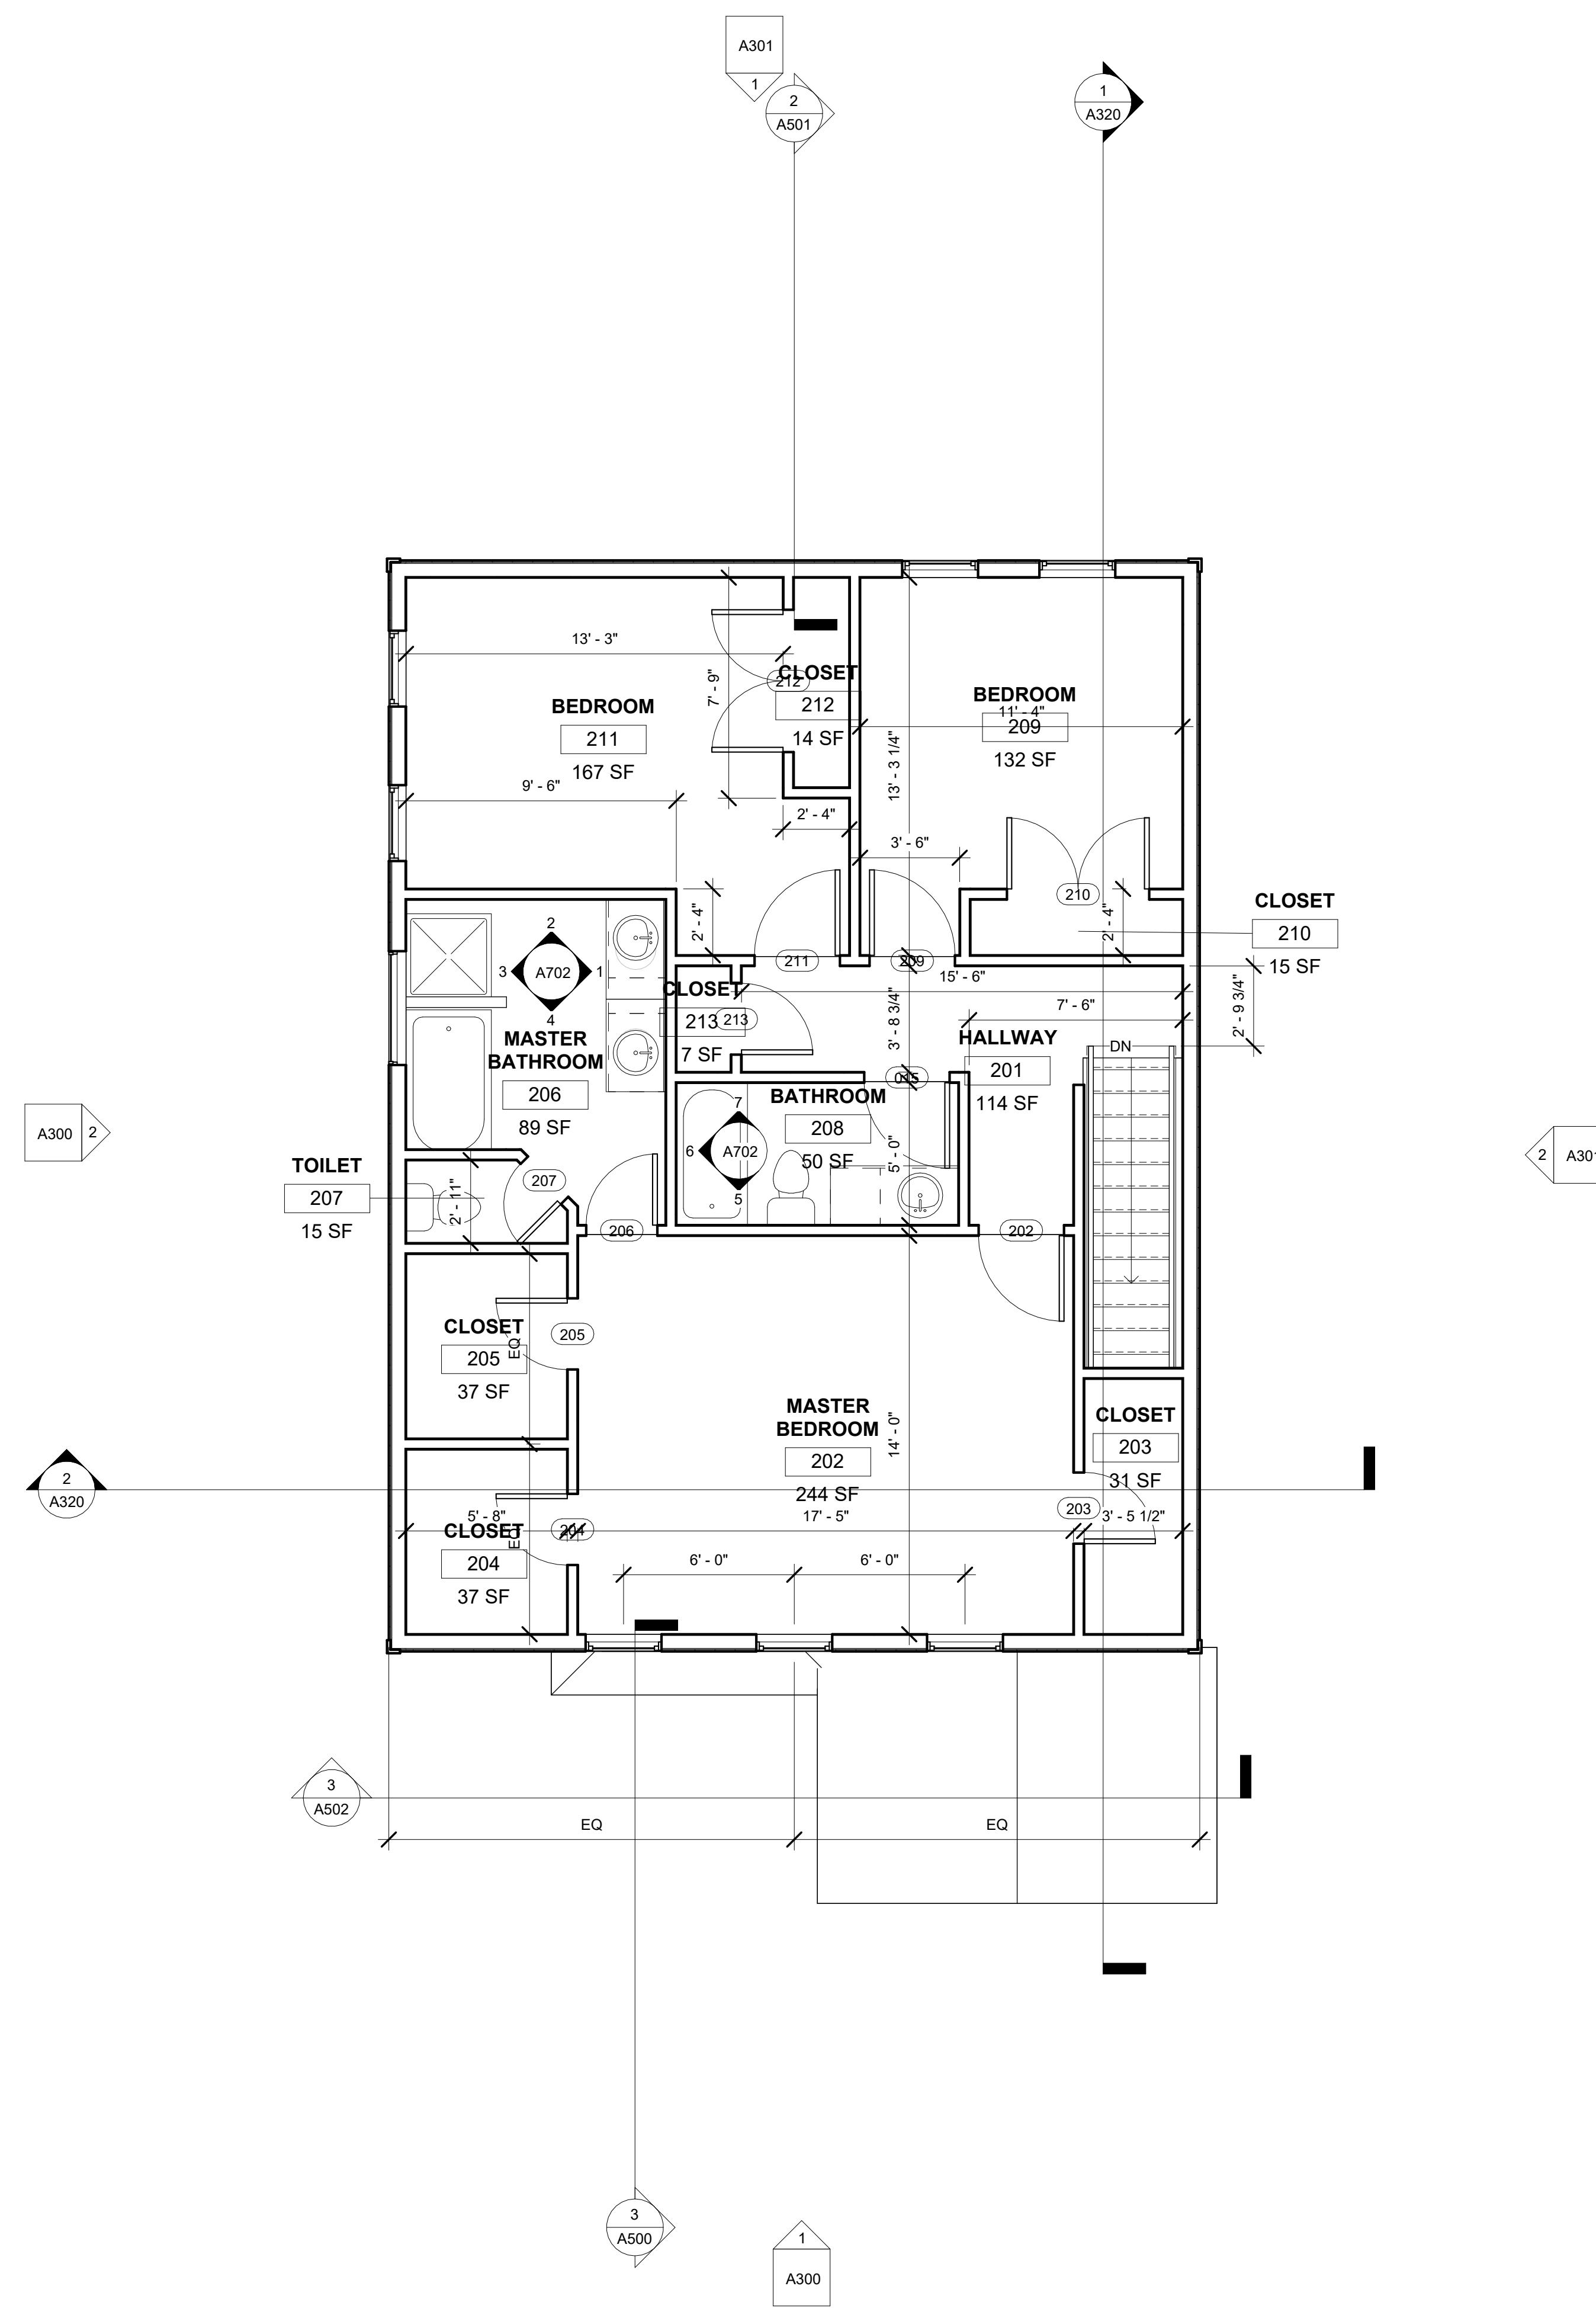

SINGLE FAMILY HOUSE 4 BEDROOM 3.5 BATH

CIOFFI FAMILY


404 PEACHTREE CIRCLE
ATLANTA, GA 30318

Project number 2023.001
Issue Date 09.09.2023



CONSTRUCTION DOCUMENTS

Revisions		
No.	Description	Date



A102

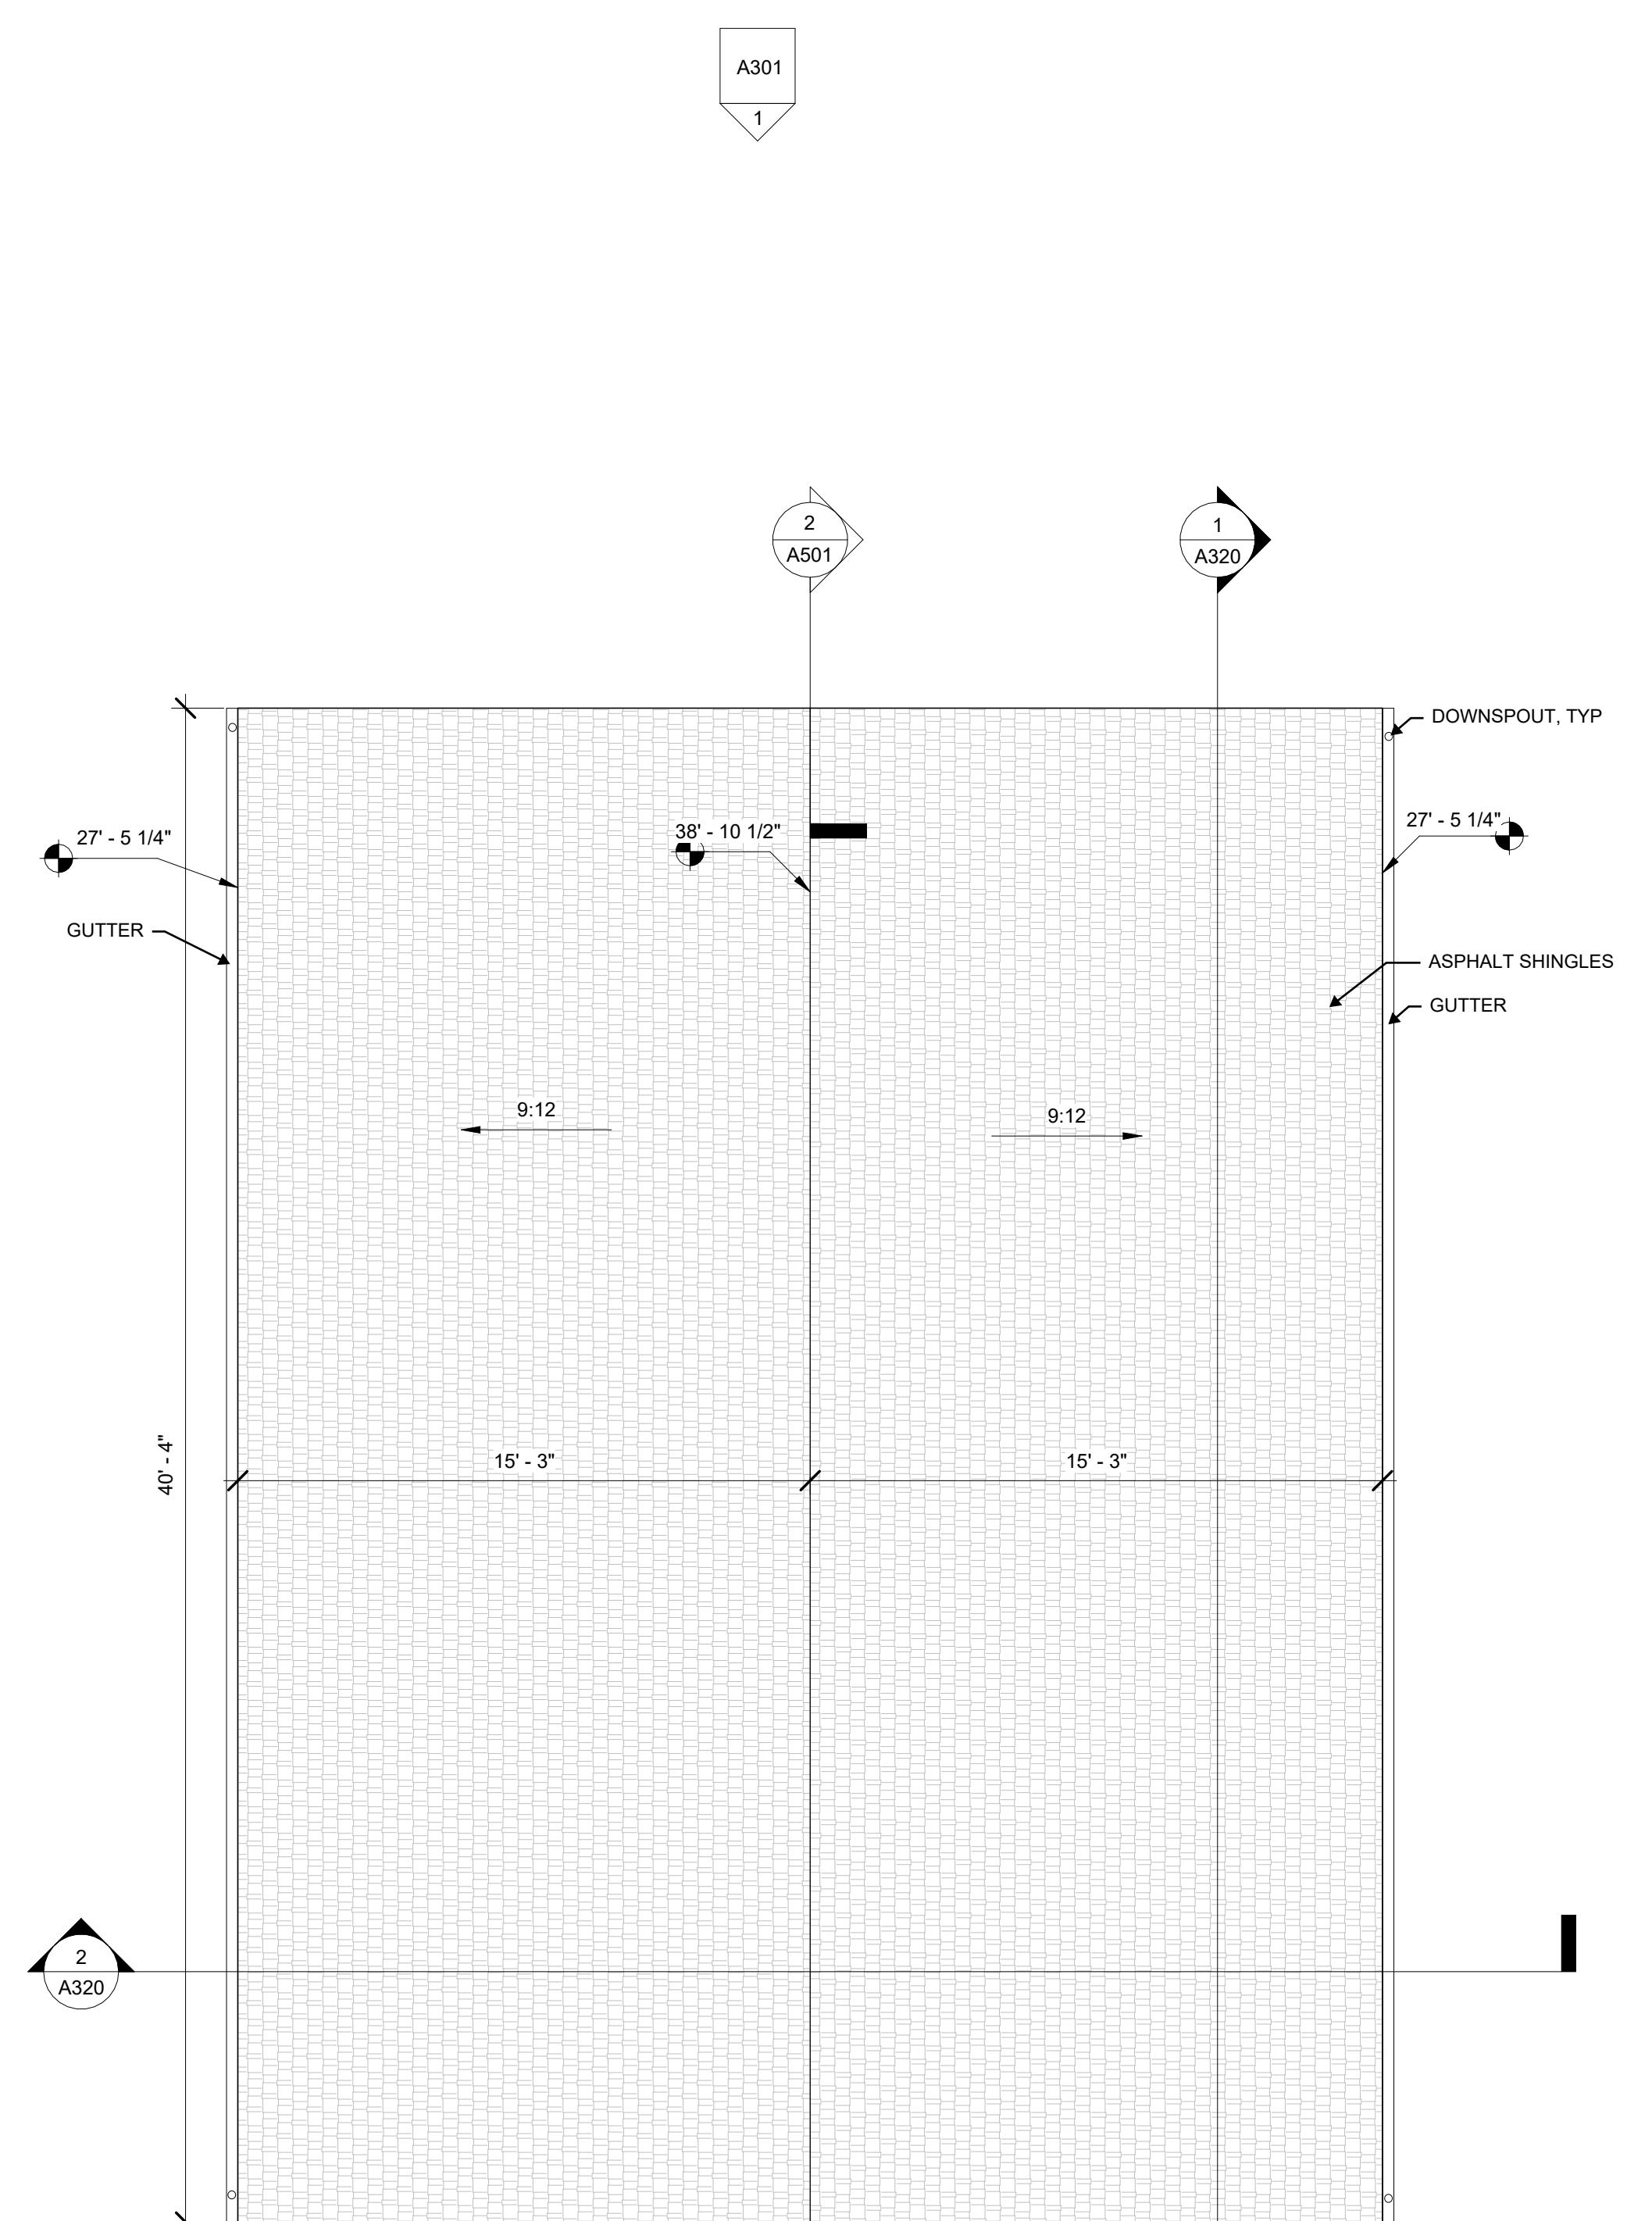

- FINISH PLAN GENERAL NOTES**
1. REFER TO A125 FOR FINISH SCHEDULE
 2. REFER TO DOOR DETAILS FOR SILL TRANSITIONS UNDER THE DOOR
 3. ALL FLOORING TRANSITIONS TO OCCUR BENEATH AND AT CENTER OF DOOR UNO

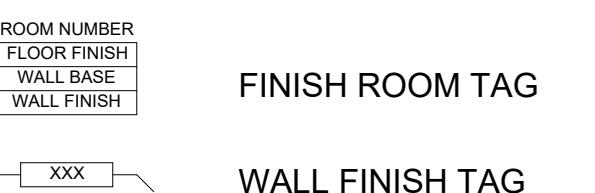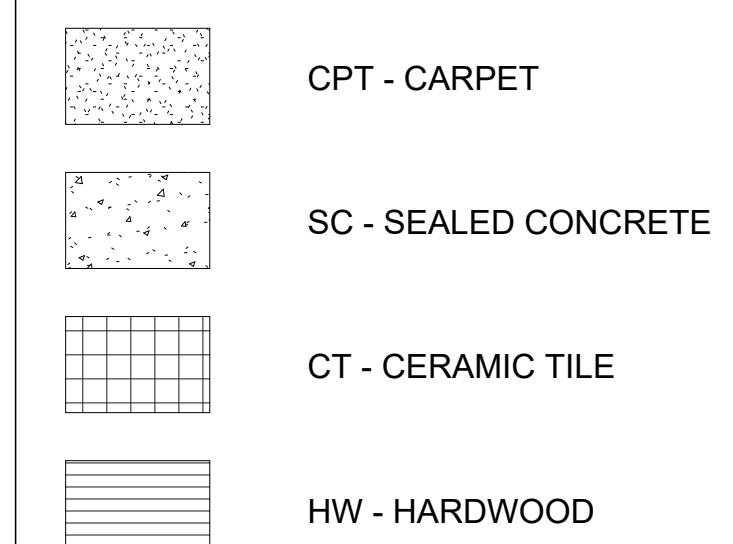FINISH LEGEND**FINISH MATERIAL GRAPHICS**

Architect Seal

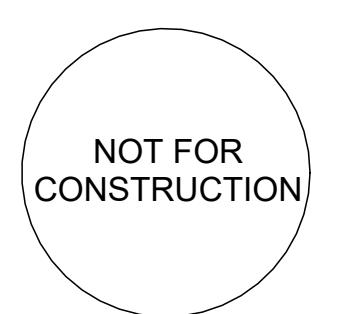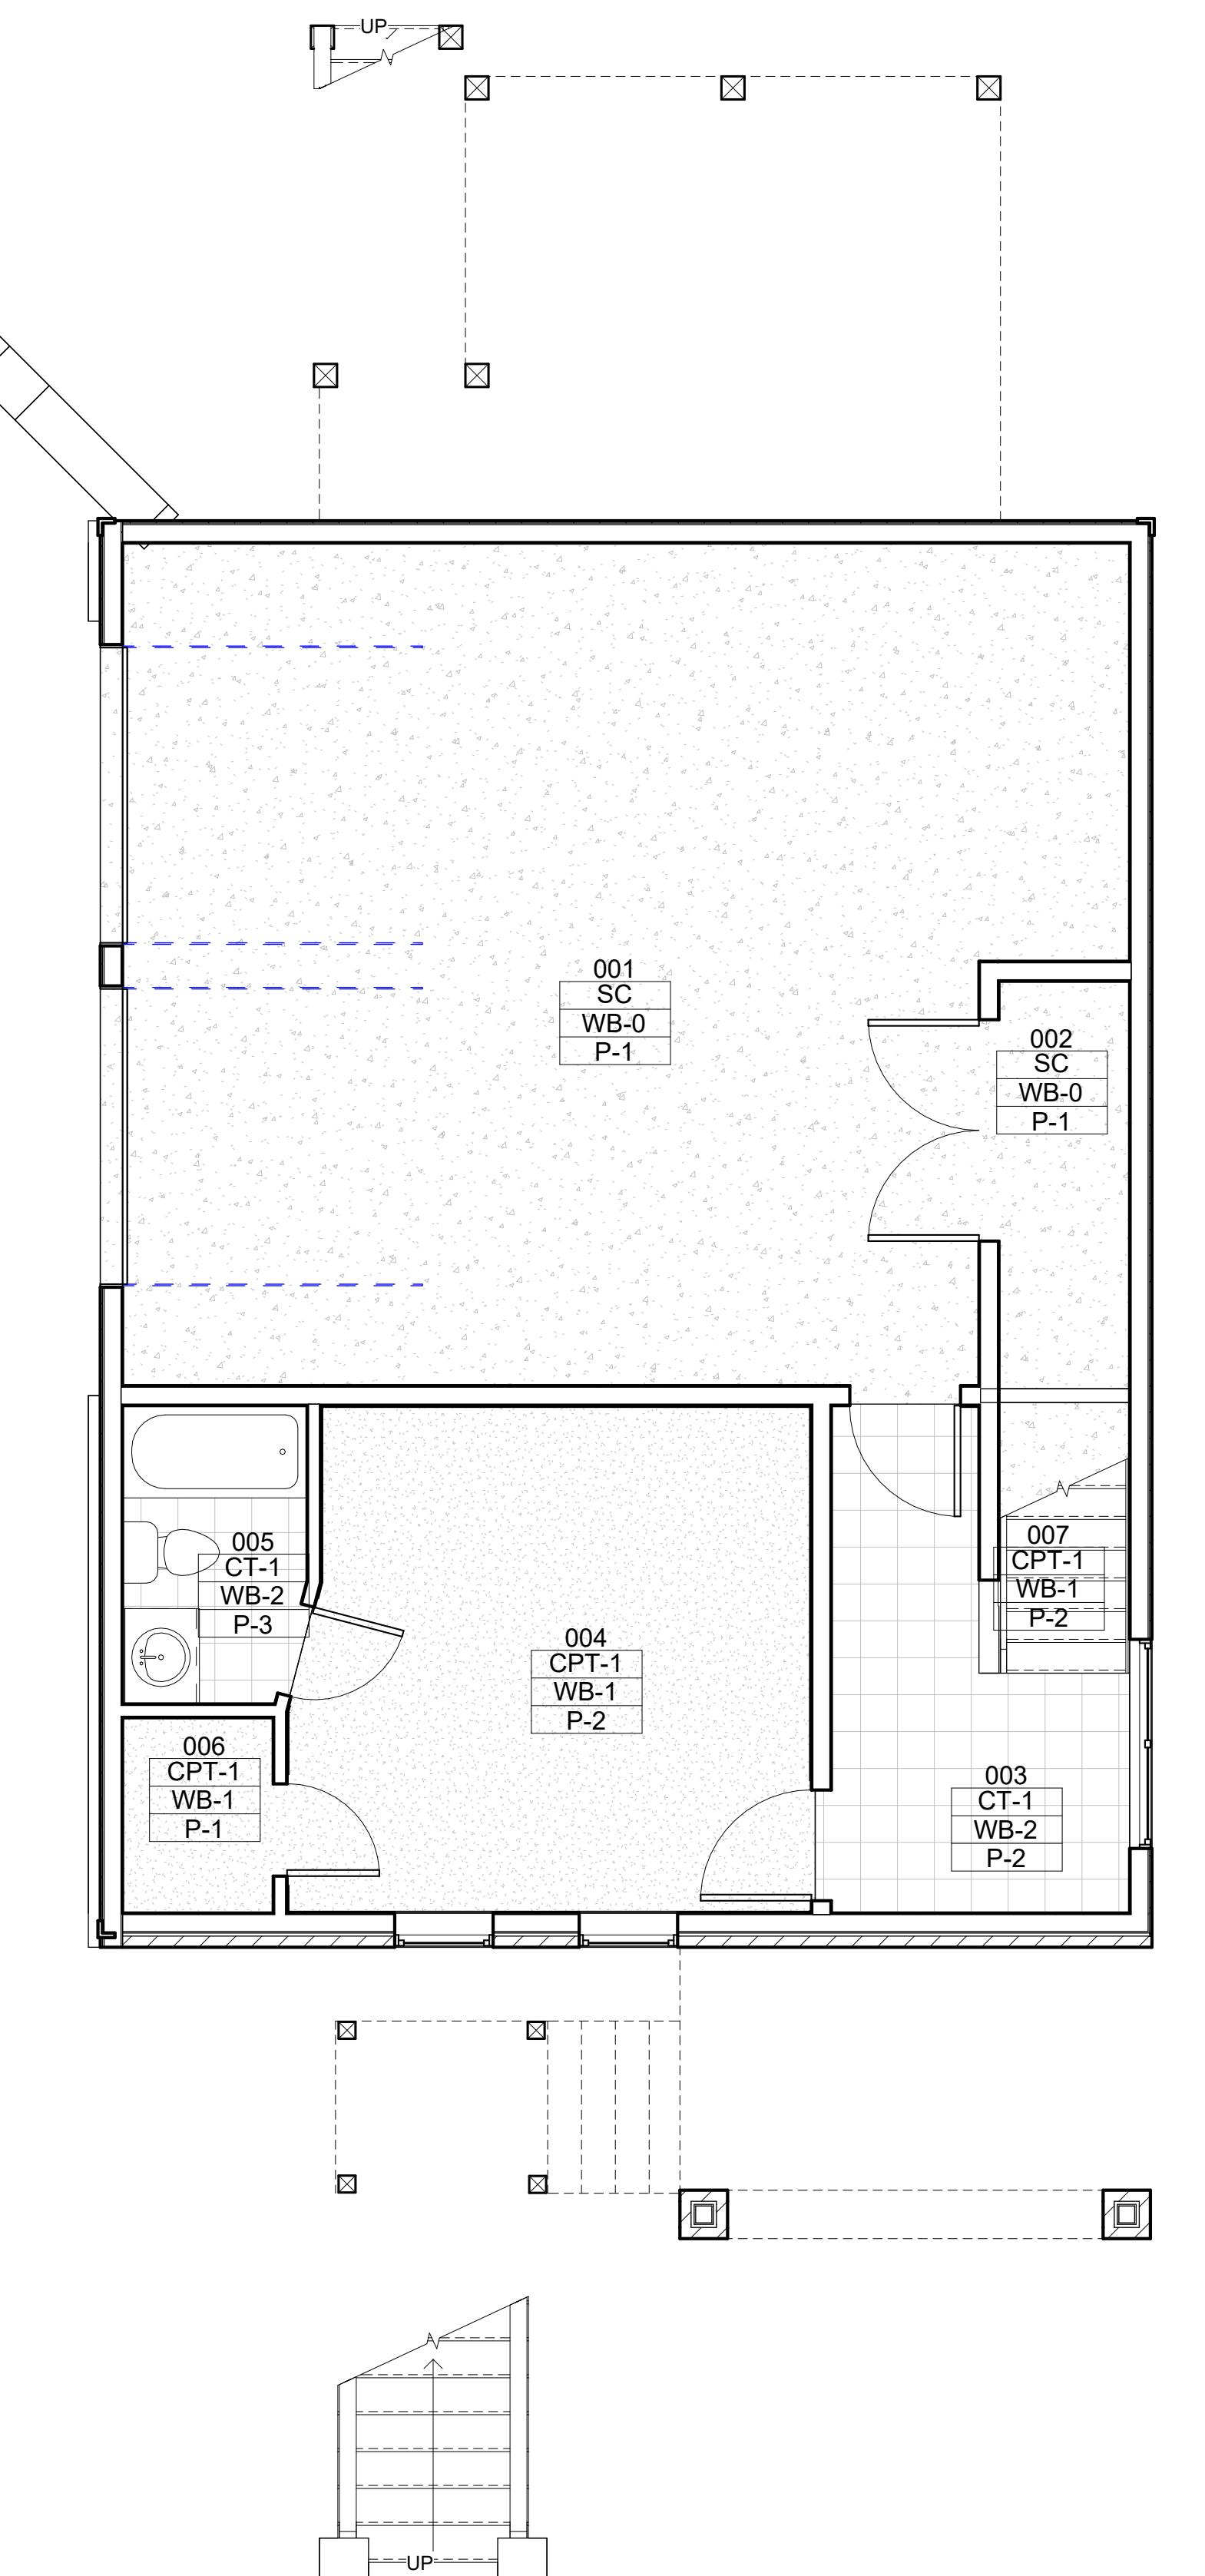**SINGLE FAMILY HOUSE
4 BEDROOM 3.5 BATH****CIOFFI FAMILY**404 PEACHTREE CIRCLE
ATLANTA, GA 30318Project number 2023.001
Issue Date 09.06.23**CONSTRUCTION DOCUMENTS**Revisions
No. Description Date

① BASEMENT FINISH PLAN
1/4" = 1'-0"


**BASEMENT FINISH
PLAN**

A120

Scale


As Indicated

- FINISH PLAN GENERAL NOTES**
1. REFER TO A125 FOR FINISH SCHEDULE
 2. REFER TO DOOR DETAILS FOR SILL TRANSITIONS UNDER THE DOOR
 3. ALL FLOORING TRANSITIONS TO OCCUR BENEATH AND AT CENTER OF DOOR UNO

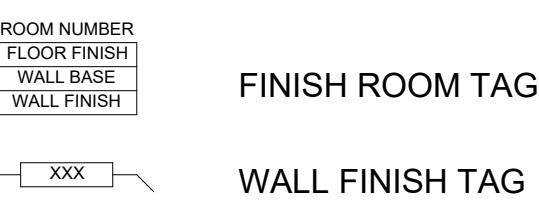FINISH LEGEND

FINISH ROOM TAG

WALL FINISH TAG

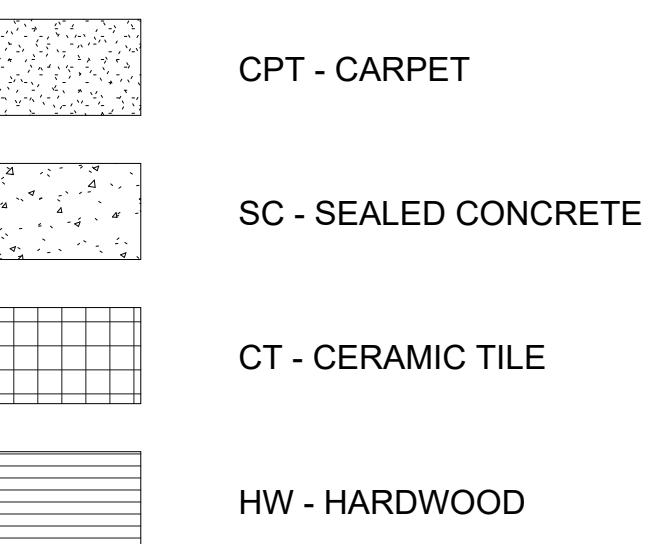FINISH MATERIAL GRAPHICS


CPT - CARPET

SC - SEALED CONCRETE


CT - CERAMIC TILE

HW - HARDWOOD


Architect Seal

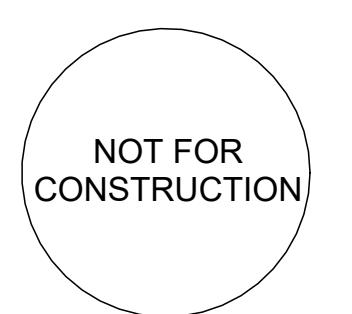**SINGLE FAMILY HOUSE
4 BEDROOM 3.5 BATH****CIOFFI FAMILY**404 PEACHTREE CIRCLE
ATLANTA, GA 30318Project number 2023.001
Issue Date 09.06.23**CONSTRUCTION DOCUMENTS**Revisions
No. Description Date**FIRST FLOOR FINISH
PLAN**

A121

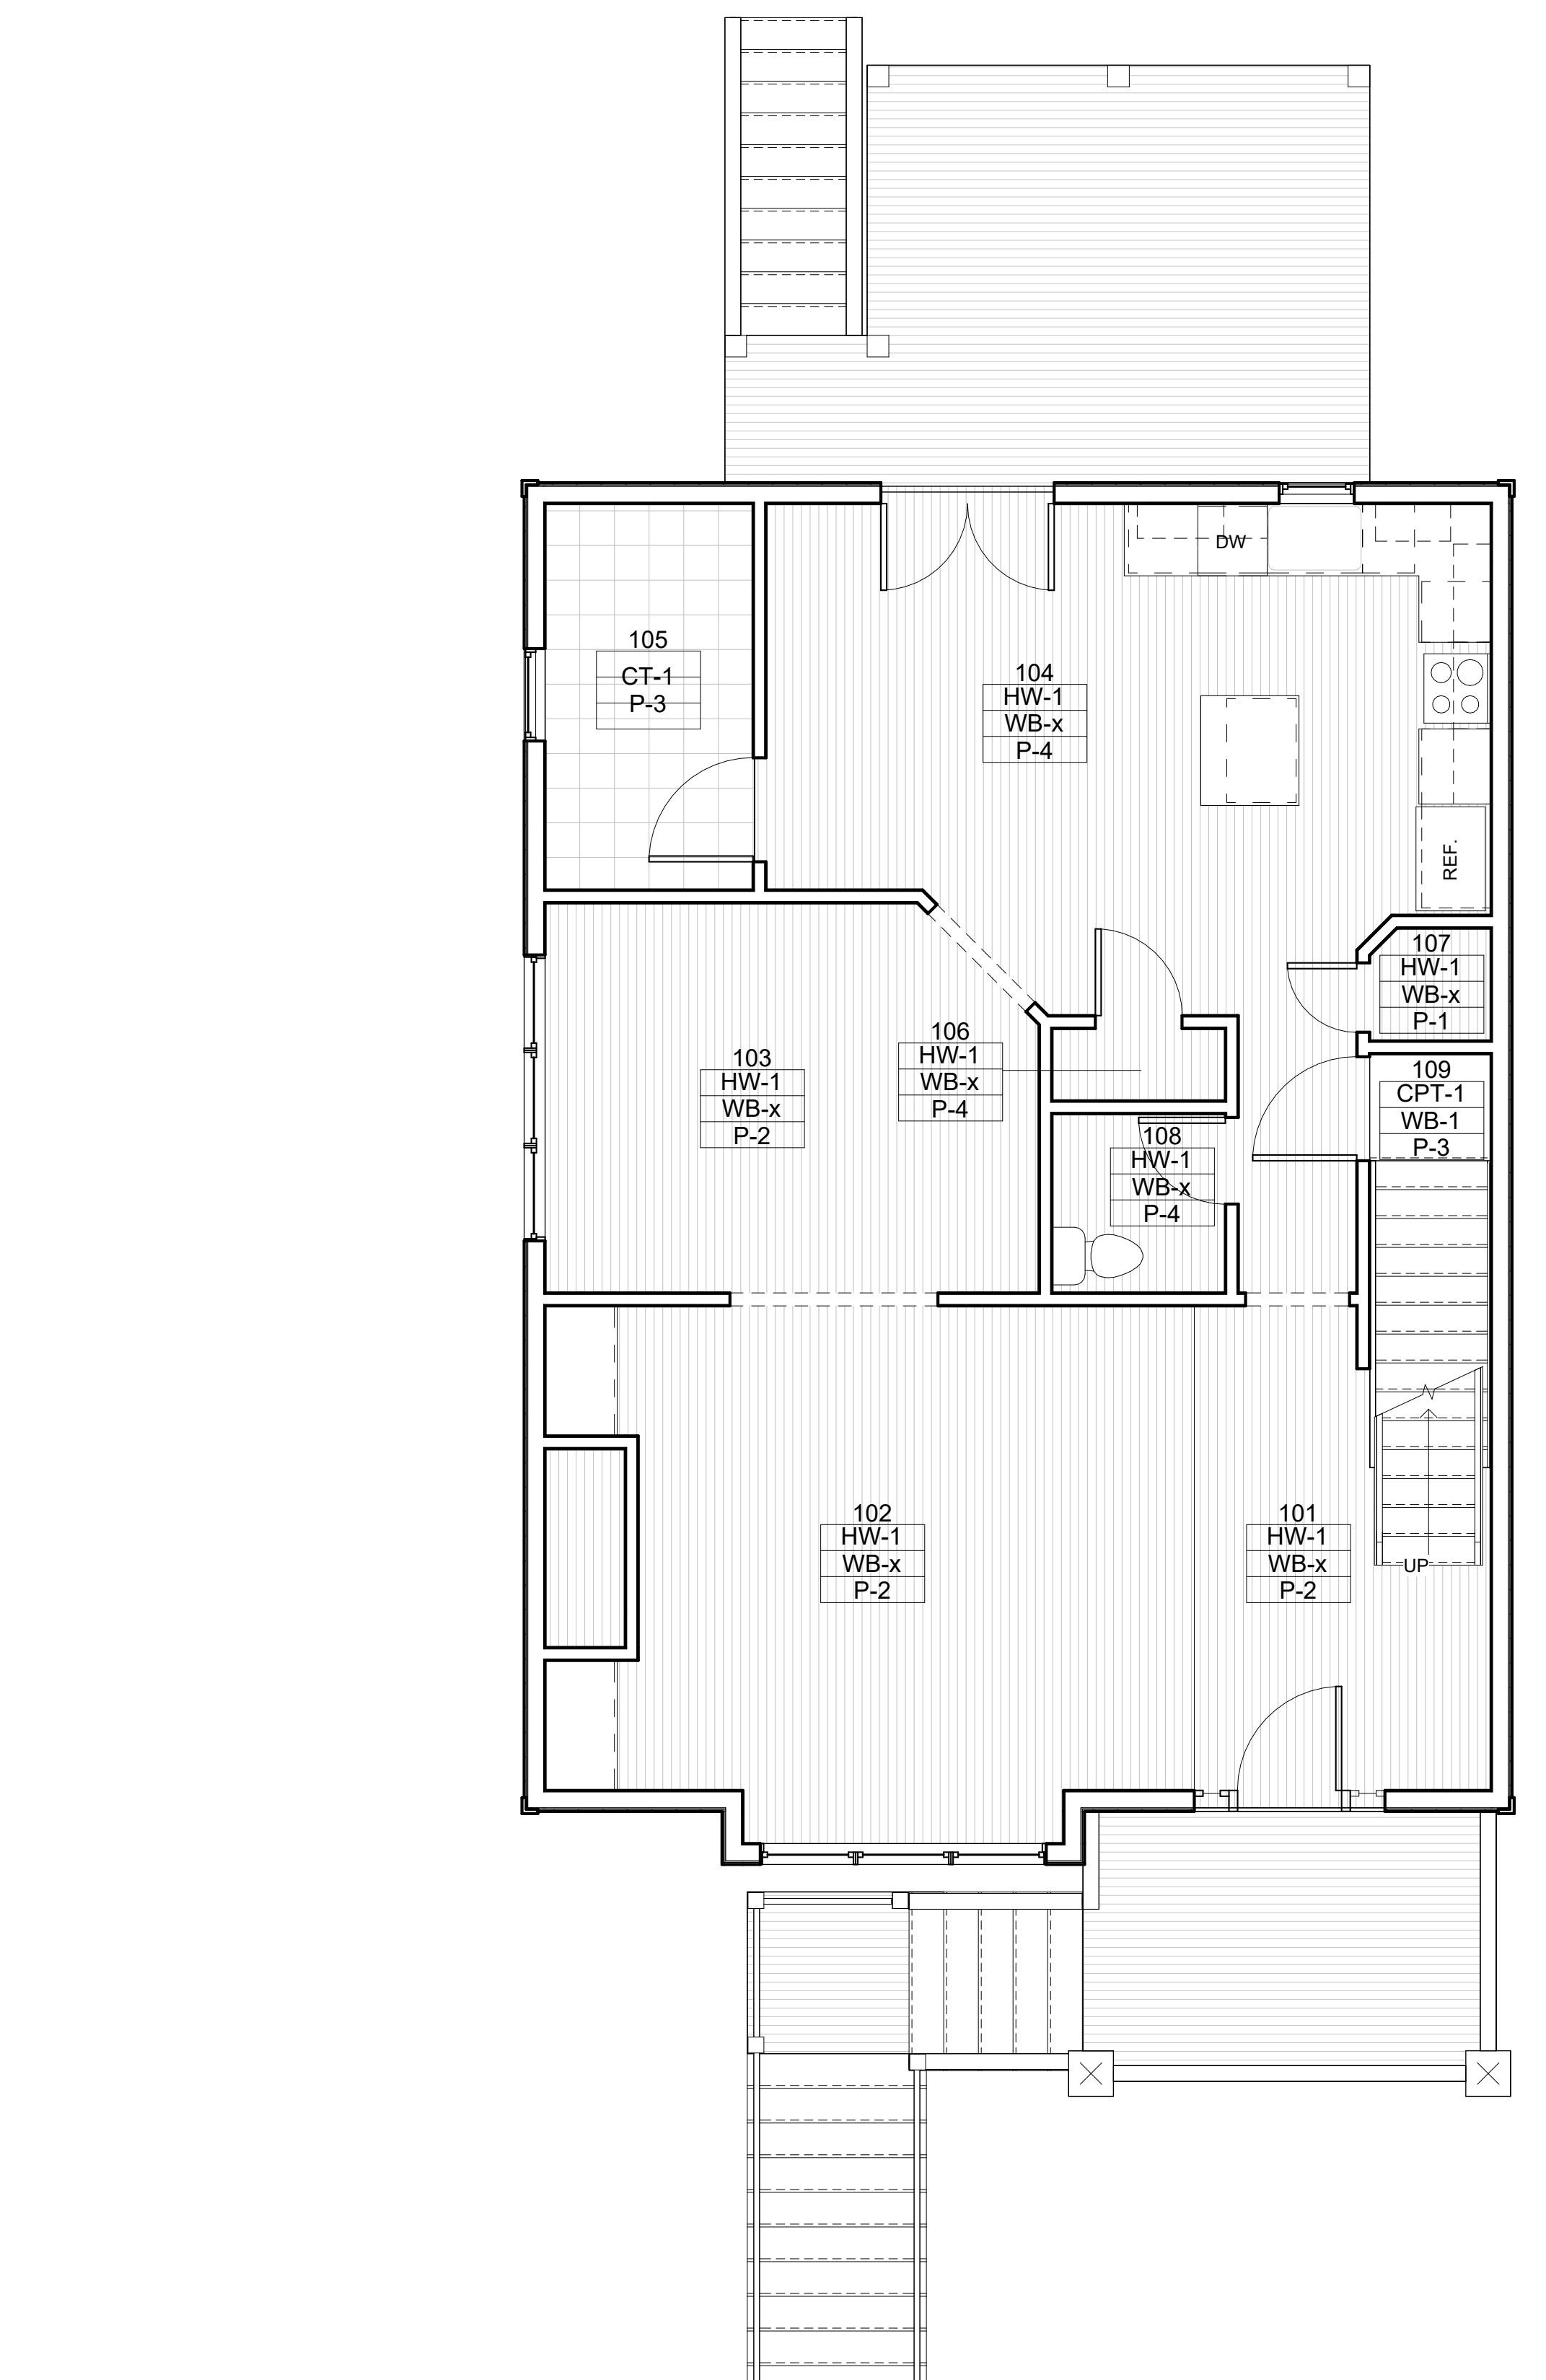


- FINISH PLAN GENERAL NOTES**
1. REFER TO A125 FOR FINISH SCHEDULE
 2. REFER TO DOOR DETAILS FOR SILL TRANSITIONS UNDER THE DOOR
 3. ALL FLOORING TRANSITIONS TO OCCUR BENEATH AND AT CENTER OF DOOR UNO

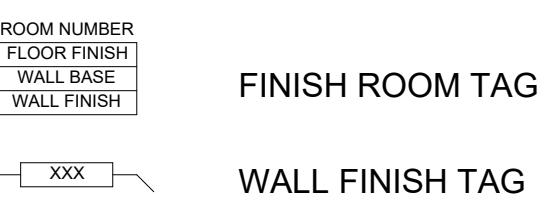FINISH LEGEND

FINISH ROOM TAG

WALL FINISH TAG

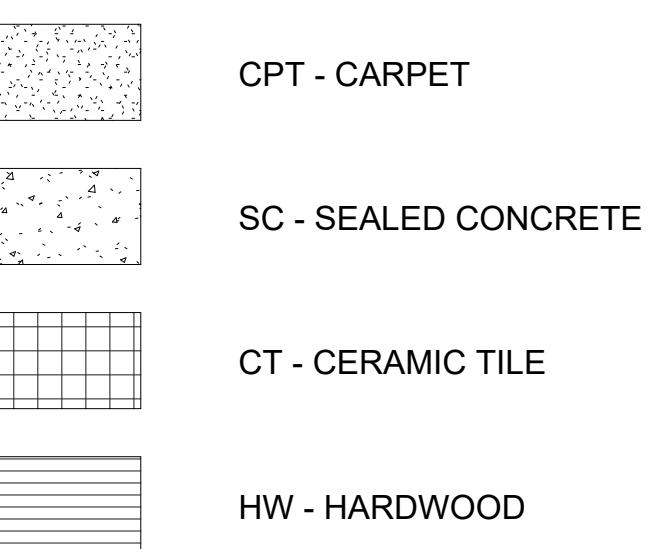FINISH MATERIAL GRAPHICS



CPT - CARPET


SC - SEALED CONCRETE

CT - CERAMIC TILE

HW - HARDWOOD


Architect Seal

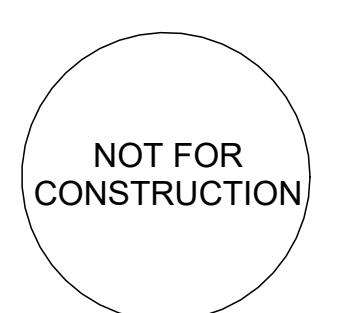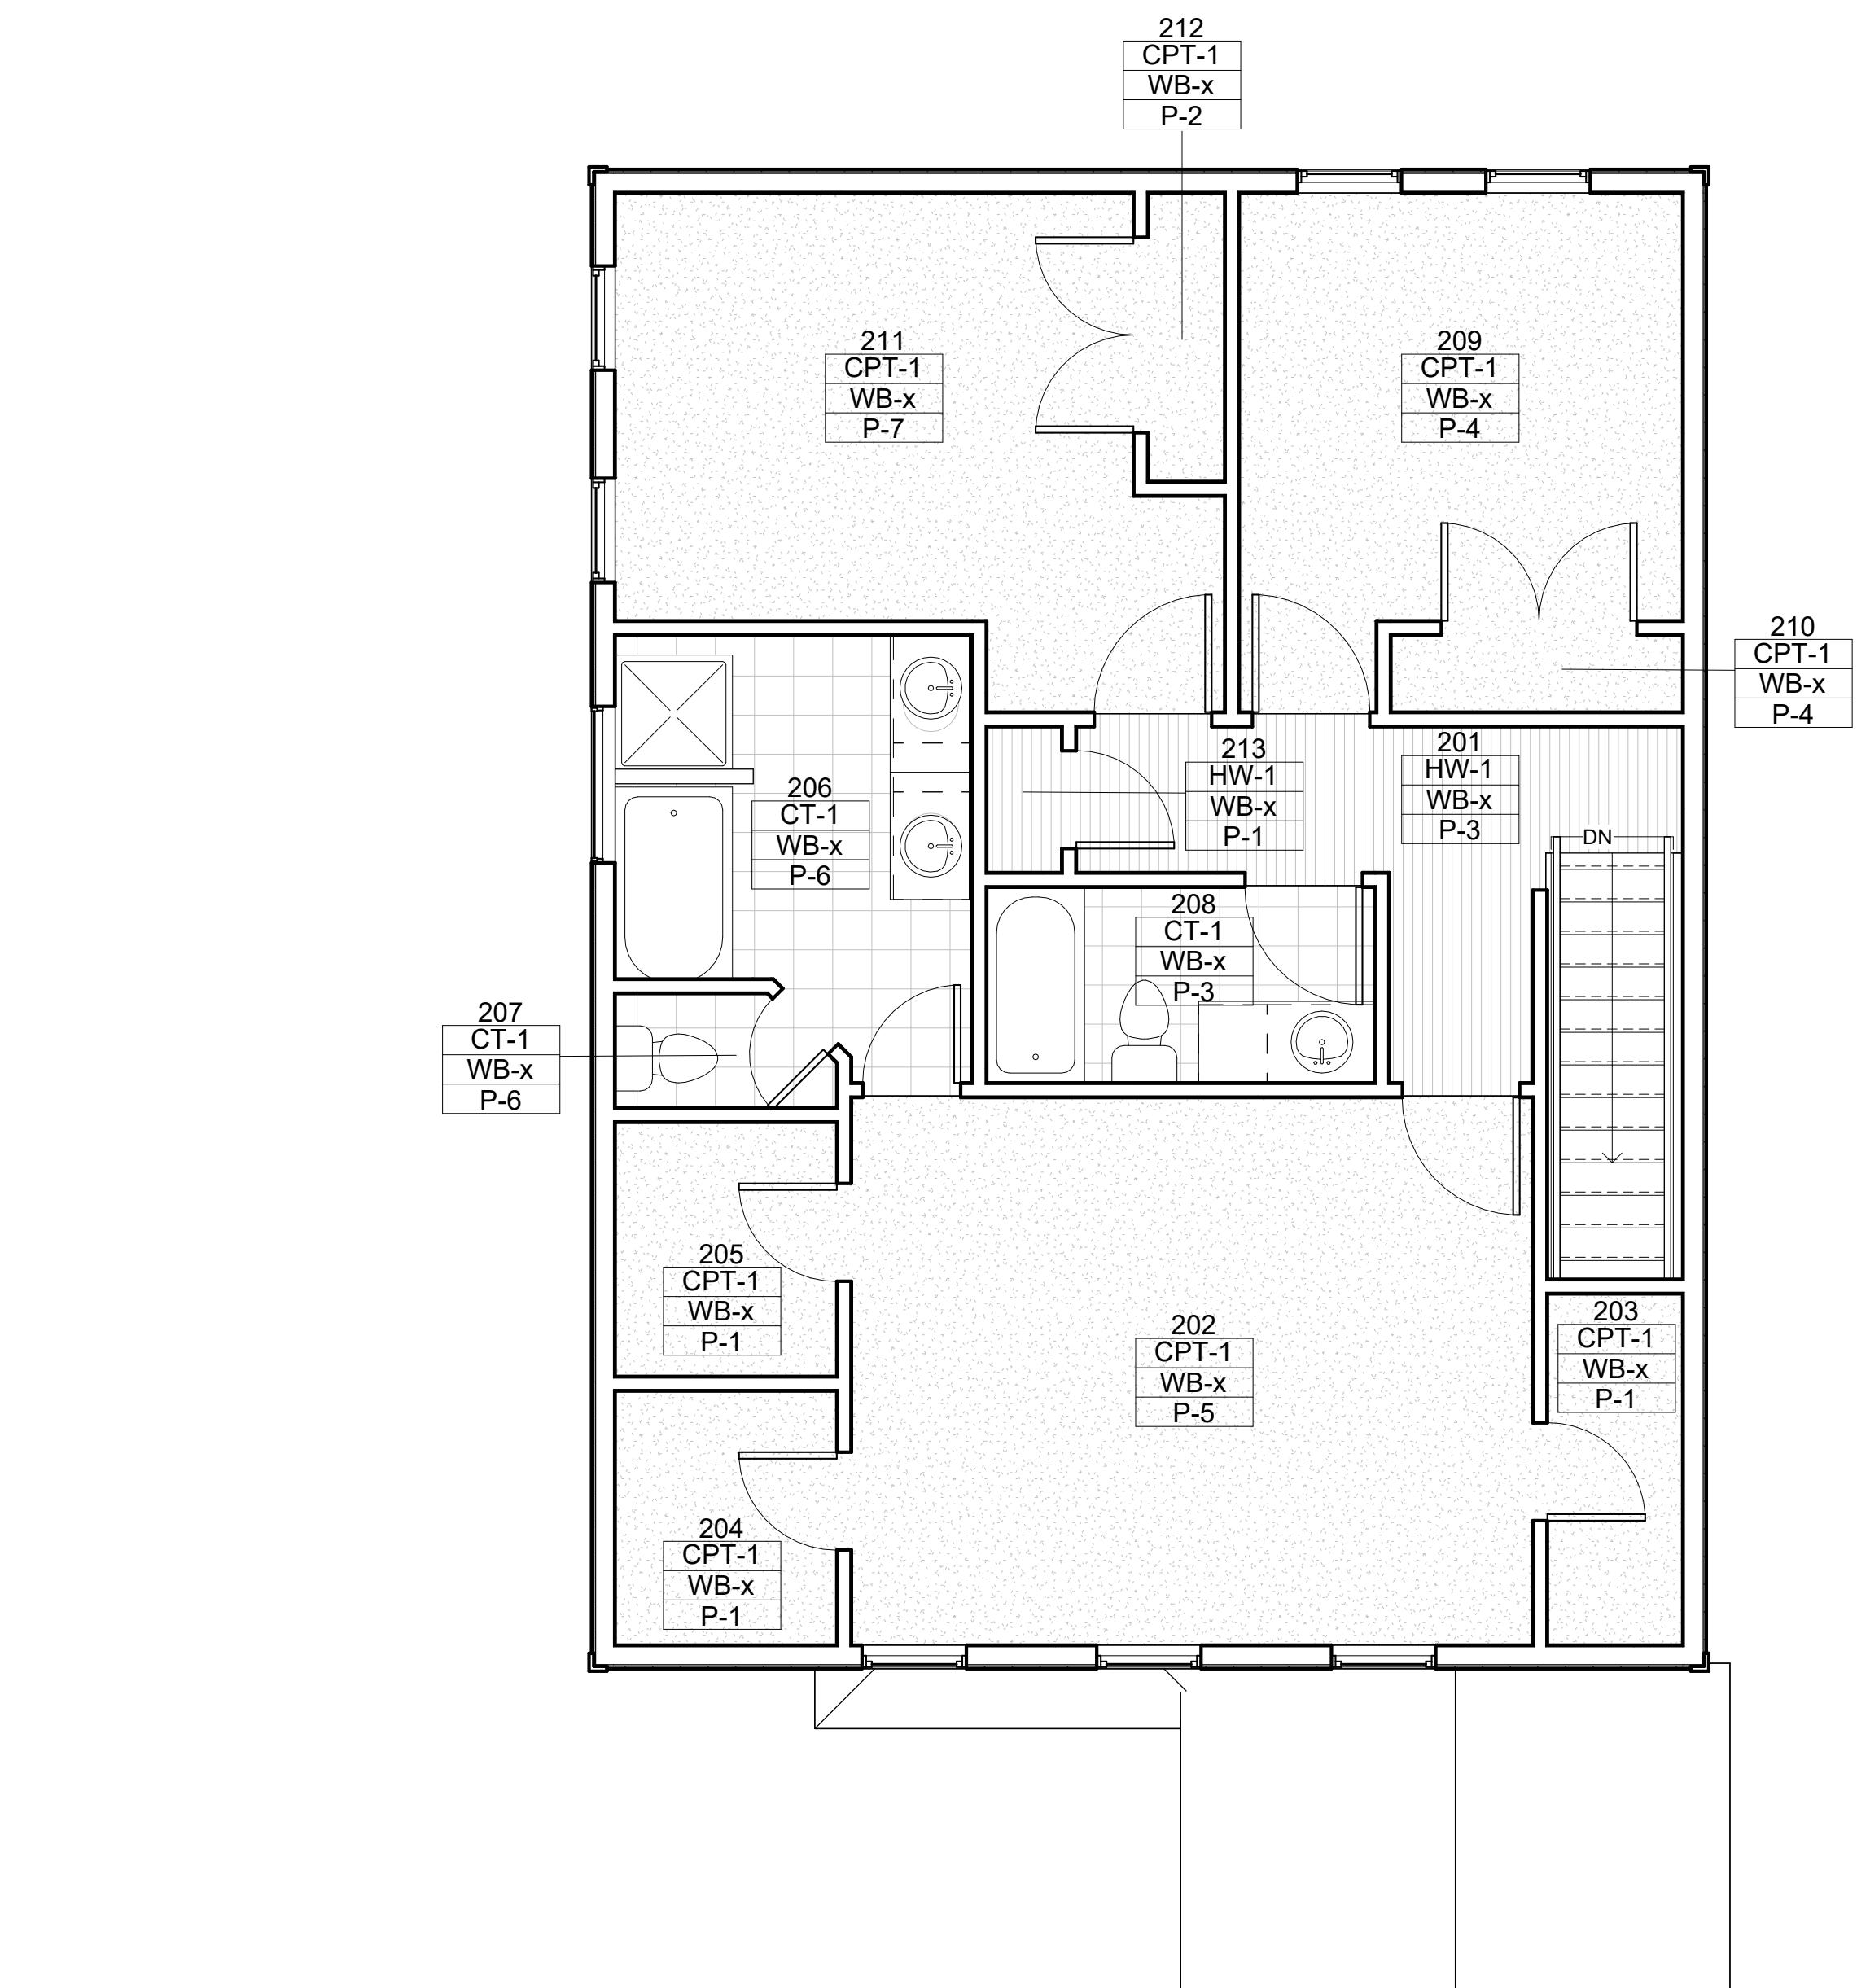**SINGLE FAMILY HOUSE
4 BEDROOM 3.5 BATH****CIOFFI FAMILY**404 PEACHTREE CIRCLE
ATLANTA, GA 30318Project number 2023.001
Issue Date 09.06.23**CONSTRUCTION DOCUMENTS**Revisions
No. Description Date**SECOND FLOOR FINISH
PLAN****A122**

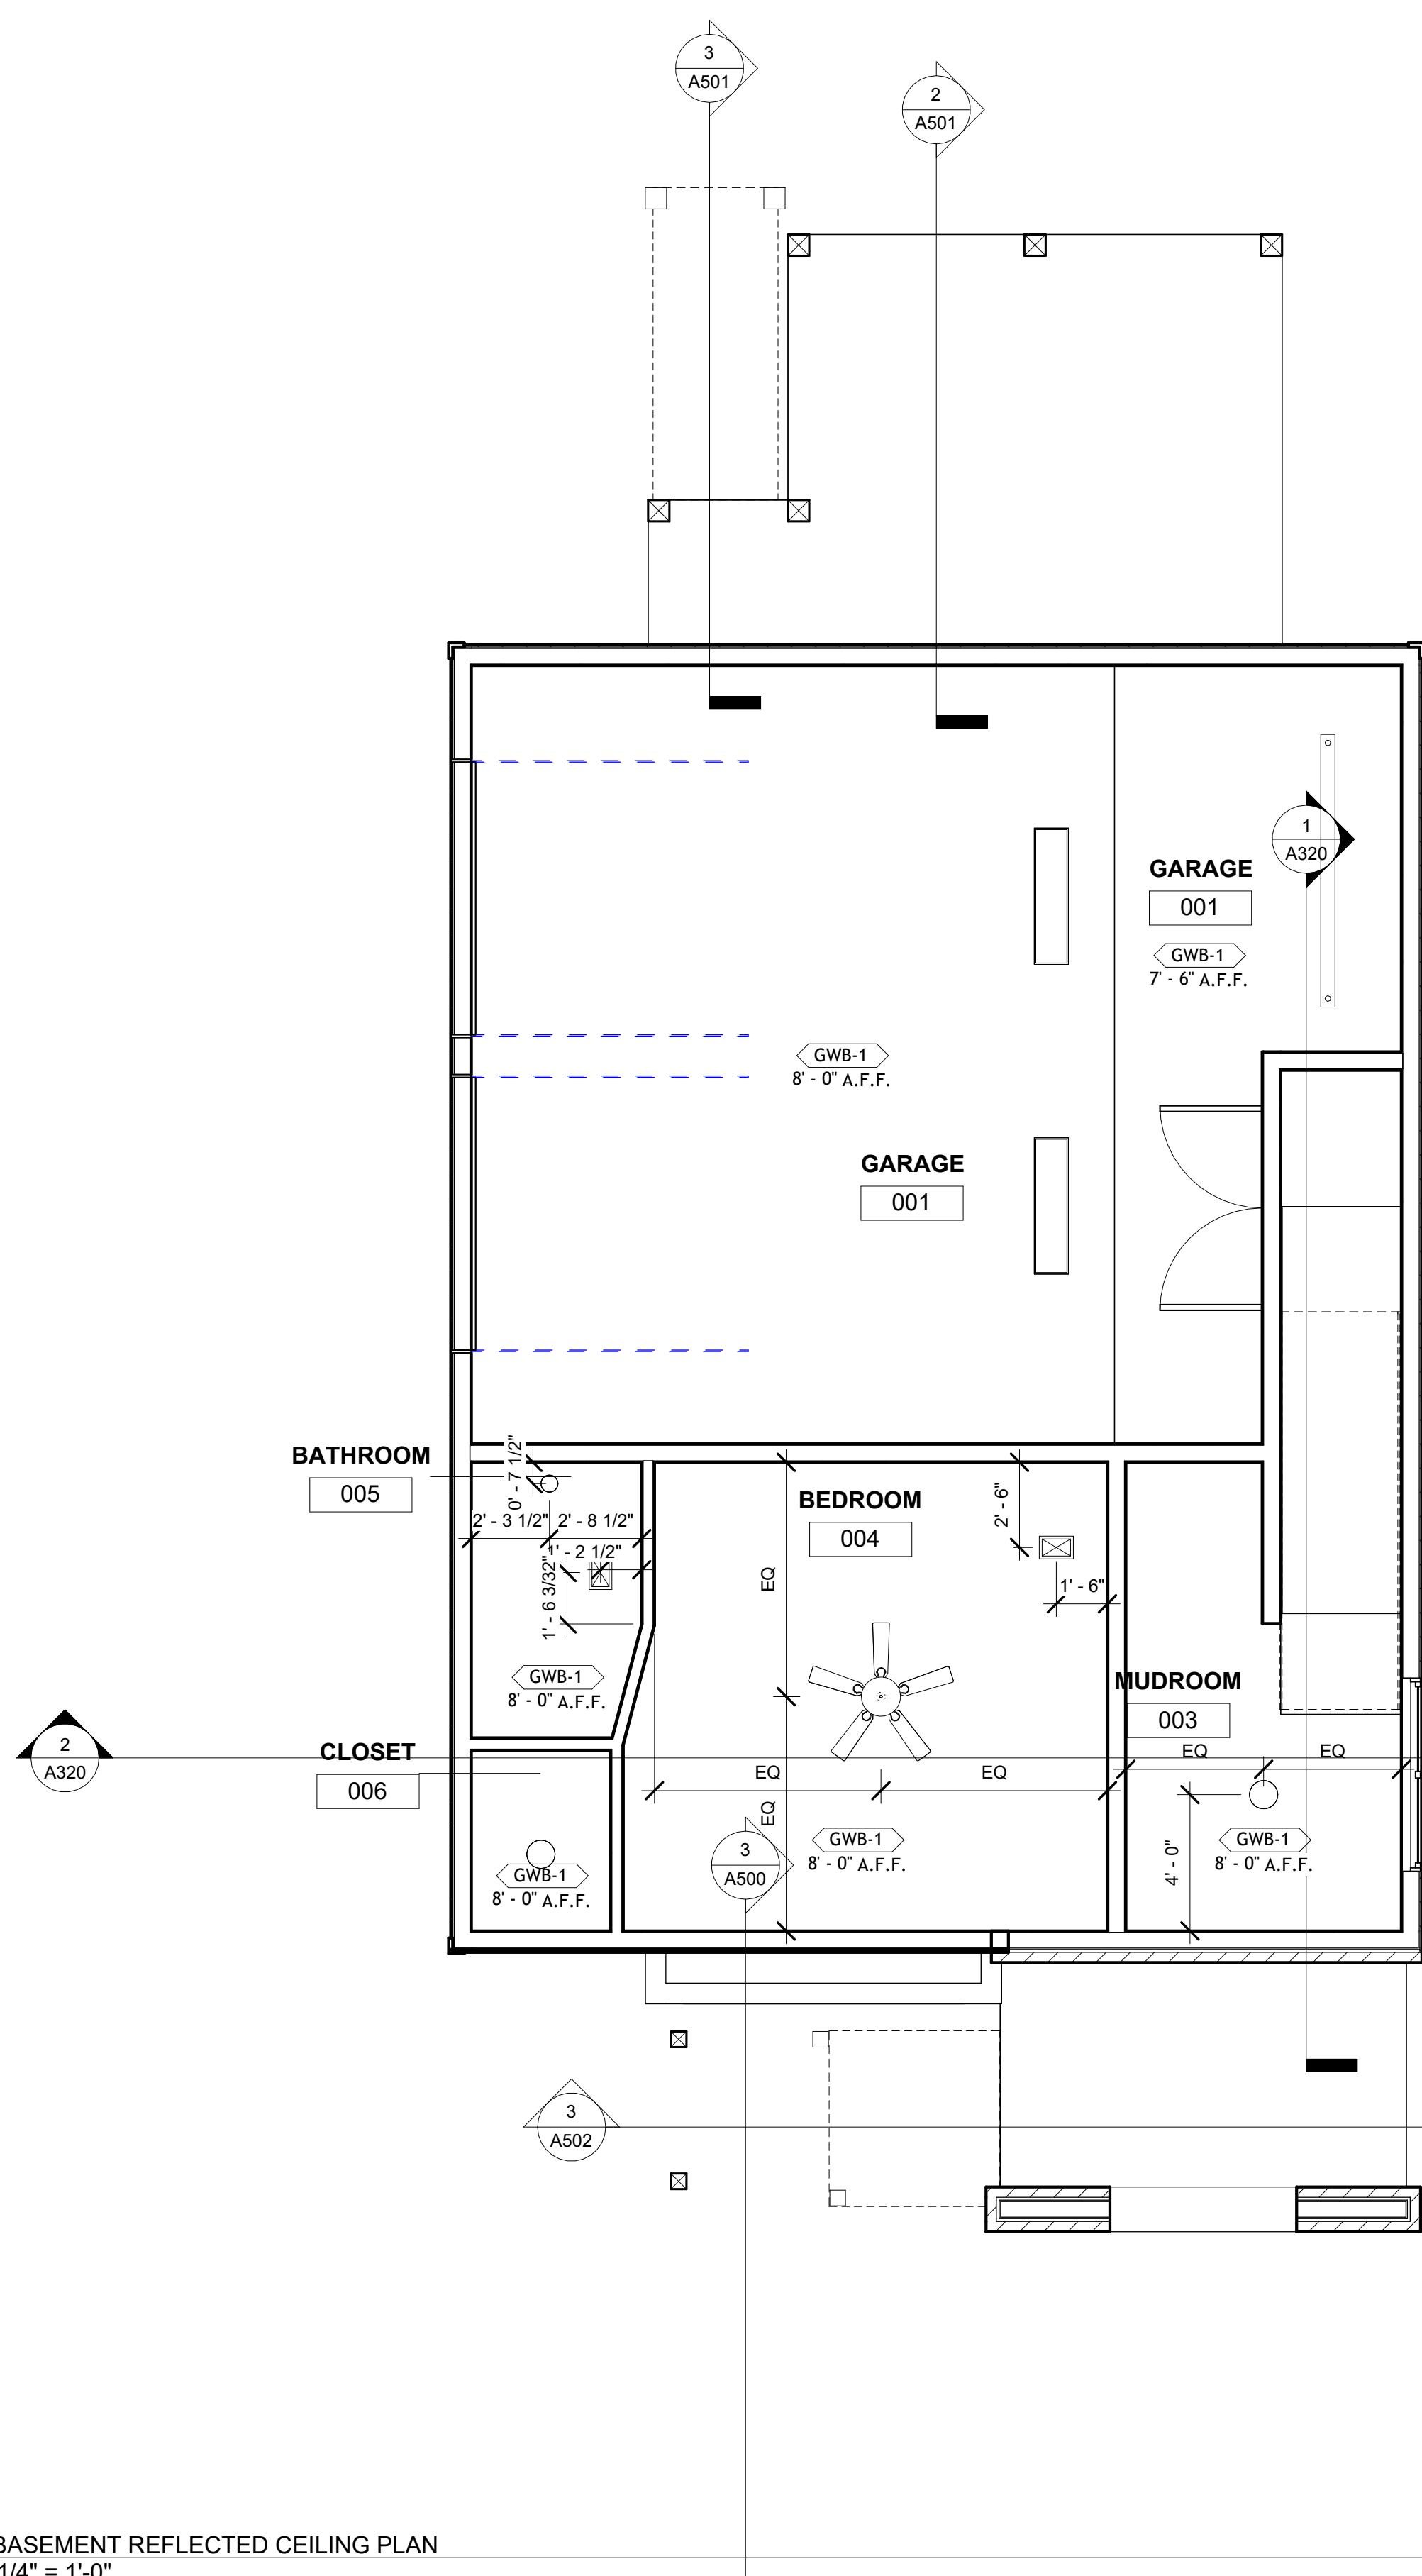
REFLECTED CEILING PLAN
GENERAL NOTES

- REFER TO A125 FOR FINISH SCHEDULE
- REFER TO DOOR DETAILS FOR SILL TRANSITIONS UNDER THE DOOR
- ALL FLOORING TRANSITIONS TO OCCUR BENEATH AND AT CENTER OF DOOR UNO


FINISH LEGEND

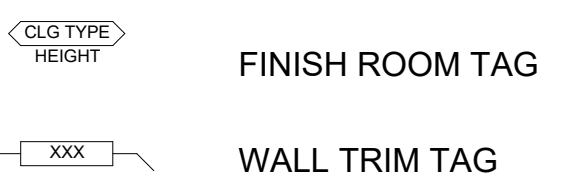

CEILING MATERIAL GRAPHICS

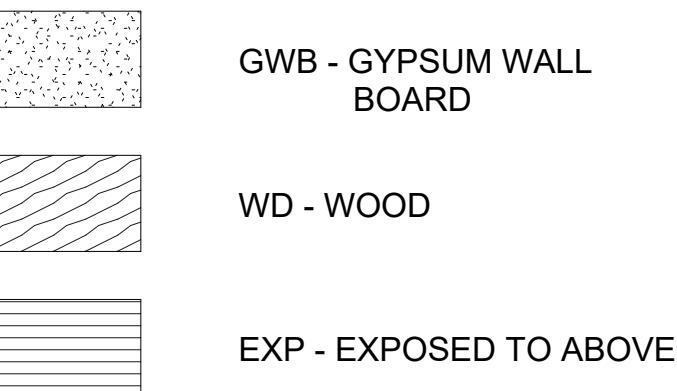

Architect Seal

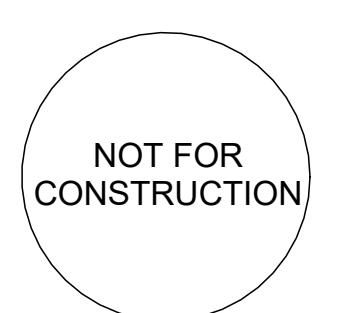**SINGLE FAMILY HOUSE
4 BEDROOM 3.5 BATH****CIOFFI FAMILY**404 PEACHTREE CIRCLE
ATLANTA, GA 30318

Project number 2023.001
Issue Date 09.06.23

CONSTRUCTION DOCUMENTS


Revisions	No.	Description	Date

BASEMENT REFLECTED
CEILING PLAN

A200

Scale

As Indicated

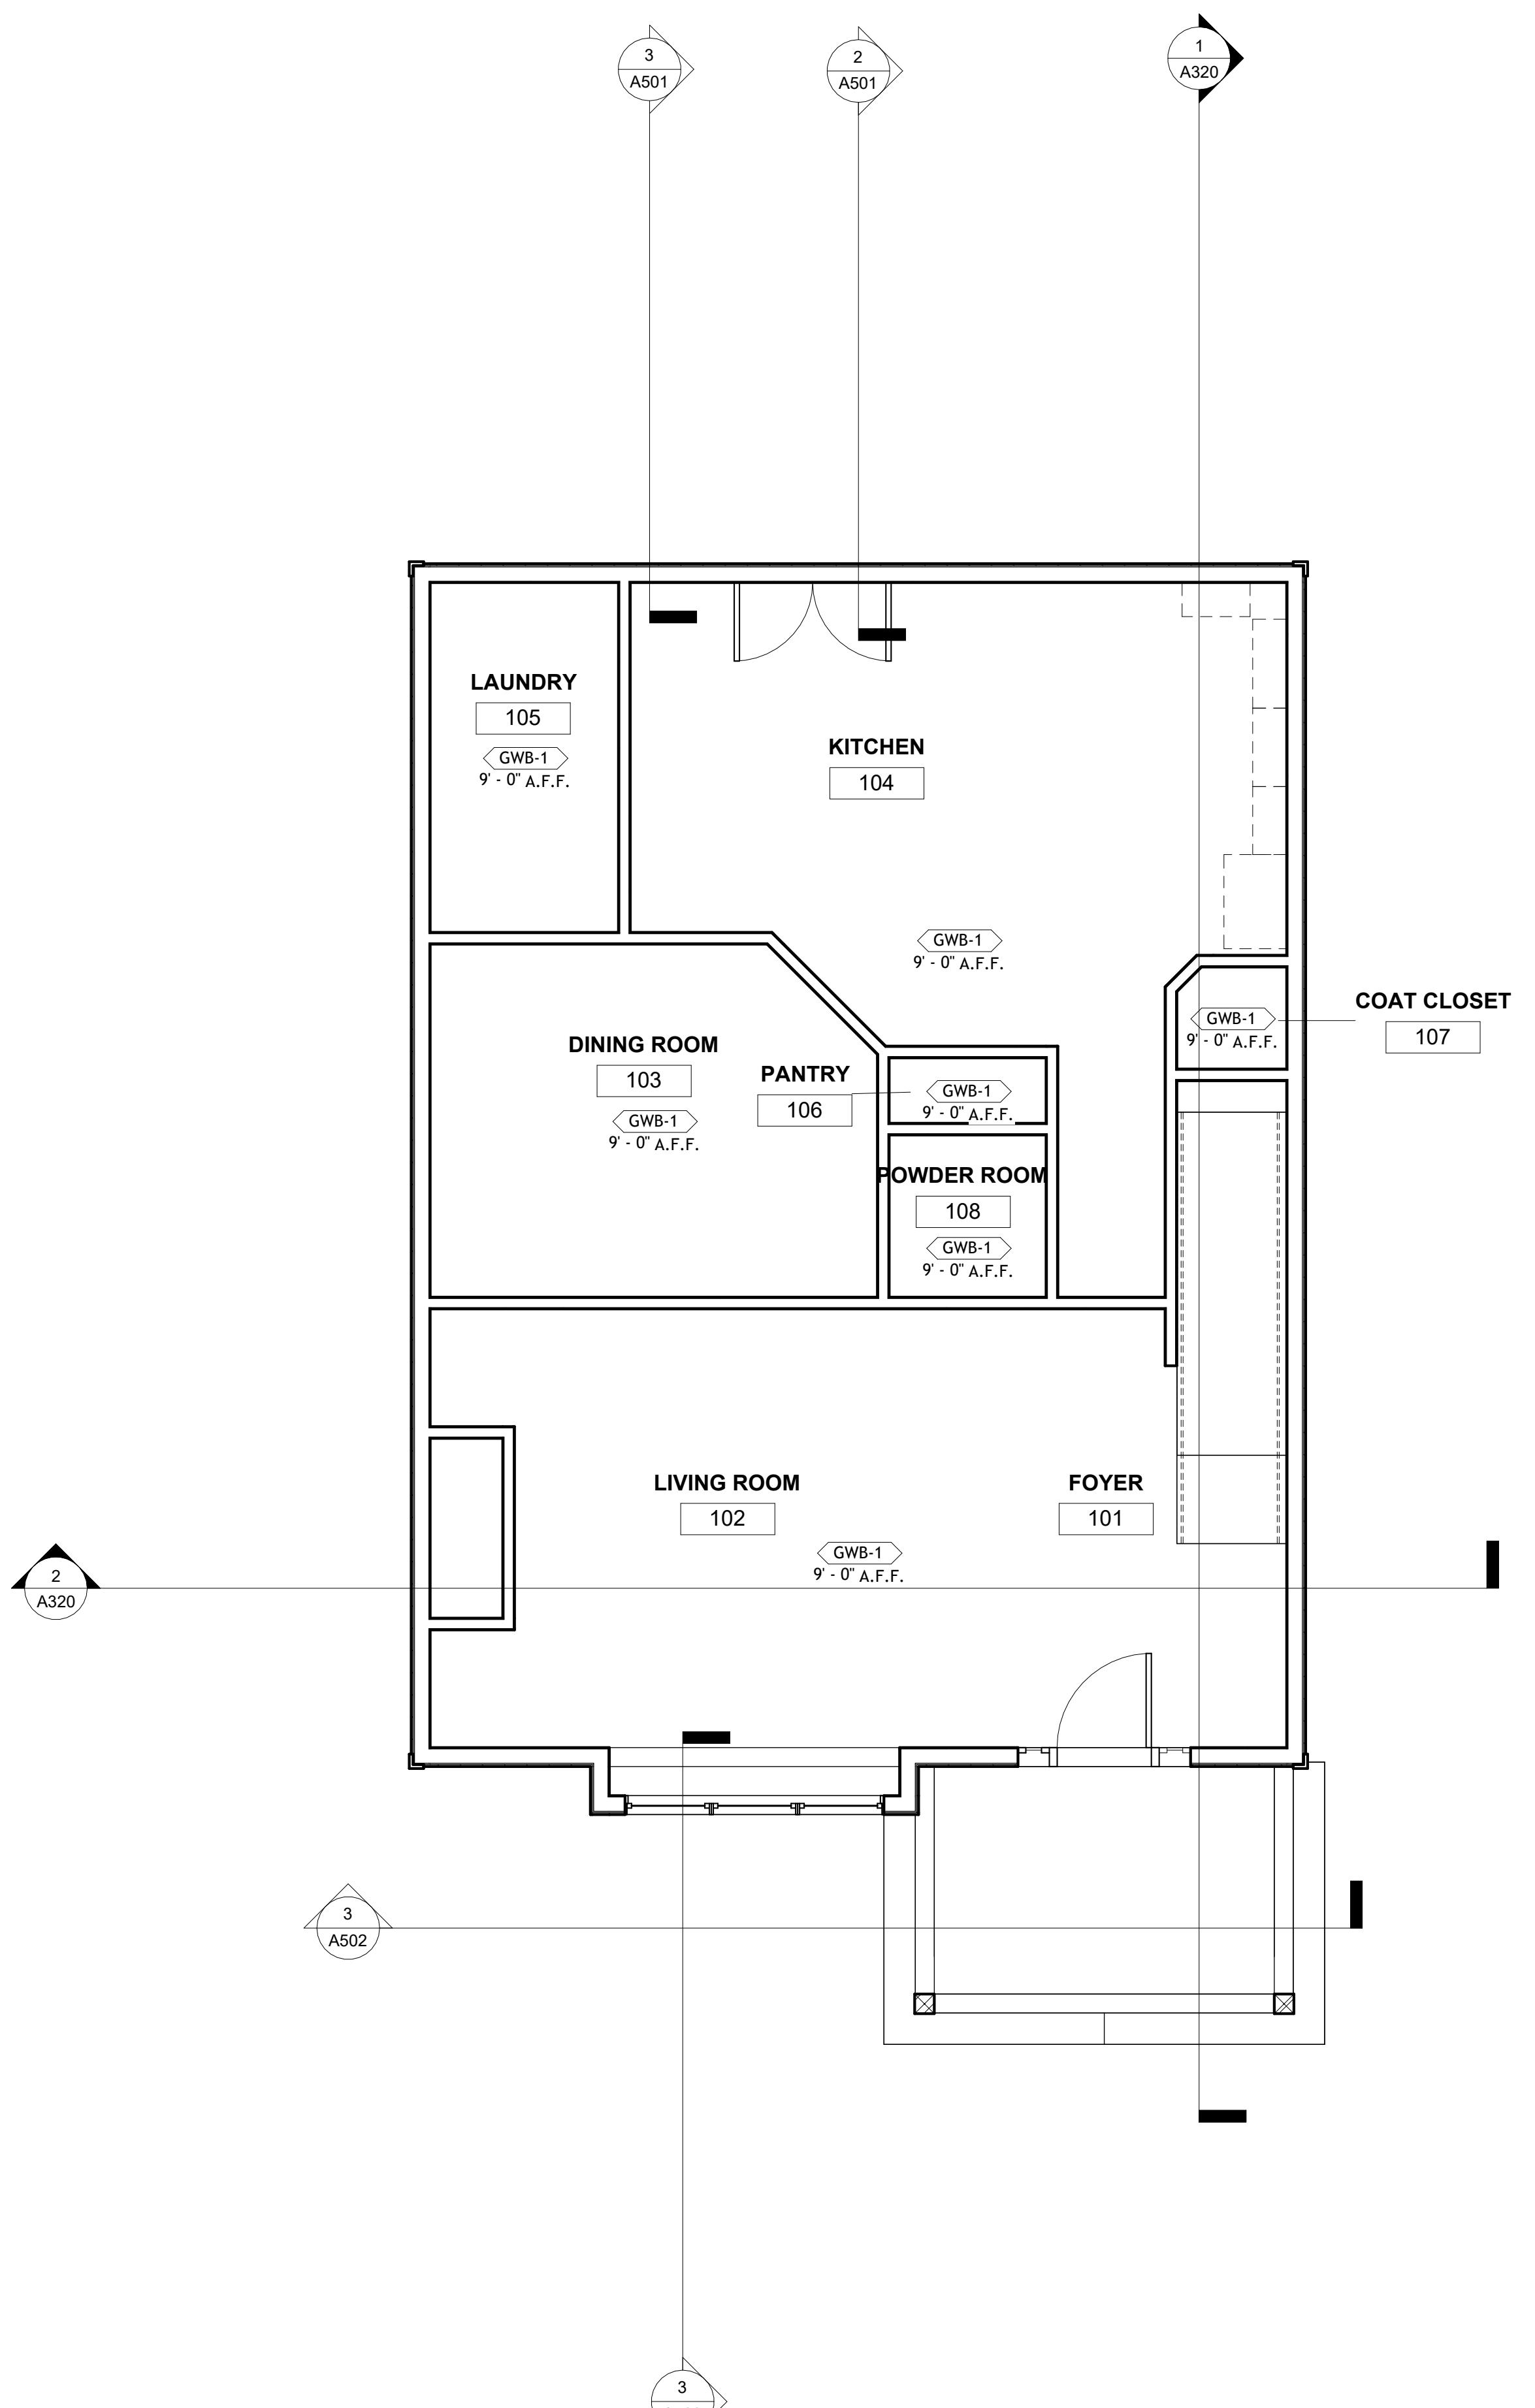


FIRST FLOOR REFLECTED CEILING
PLAN
① 1/4" = 1'-0"


REFLECTED CEILING PLAN GENERAL NOTES

- REFER TO A125 FOR FINISH SCHEDULE
- REFER TO DOOR DETAILS FOR SILL TRANSITIONS UNDER THE DOOR
- ALL FLOORING TRANSITIONS TO OCCUR BENEATH AND AT CENTER OF DOOR UNO


FINISH LEGEND

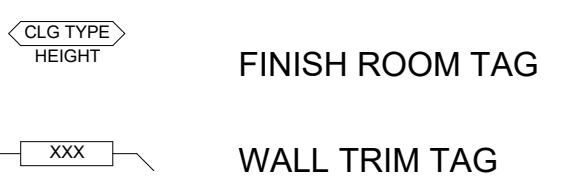

CEILING MATERIAL GRAPHICS

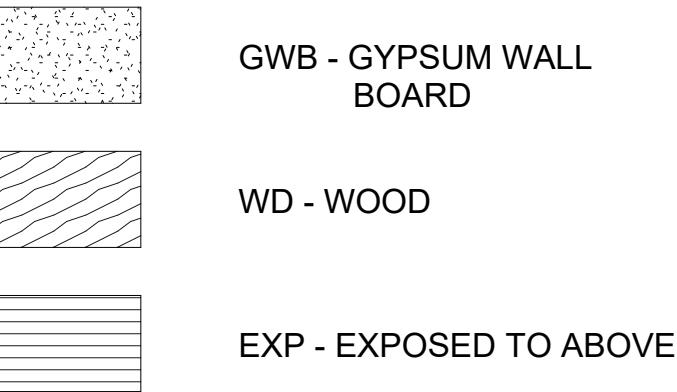

Architect Seal

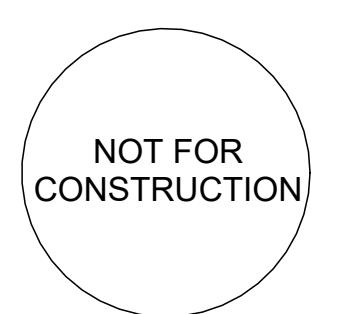

SINGLE FAMILY HOUSE 4 BEDROOM 3.5 BATH

CIOFFI FAMILY

404 PEACHTREE CIRCLE
ATLANTA, GA 30318

Project number 2023.001
Issue Date 09.06.23

CONSTRUCTION DOCUMENTS


Revisions	No.	Description	Date
-----------	-----	-------------	------

FIRST FLOOR
REFLECTED CEILING
PLAN

A201


Scale

As Indicated

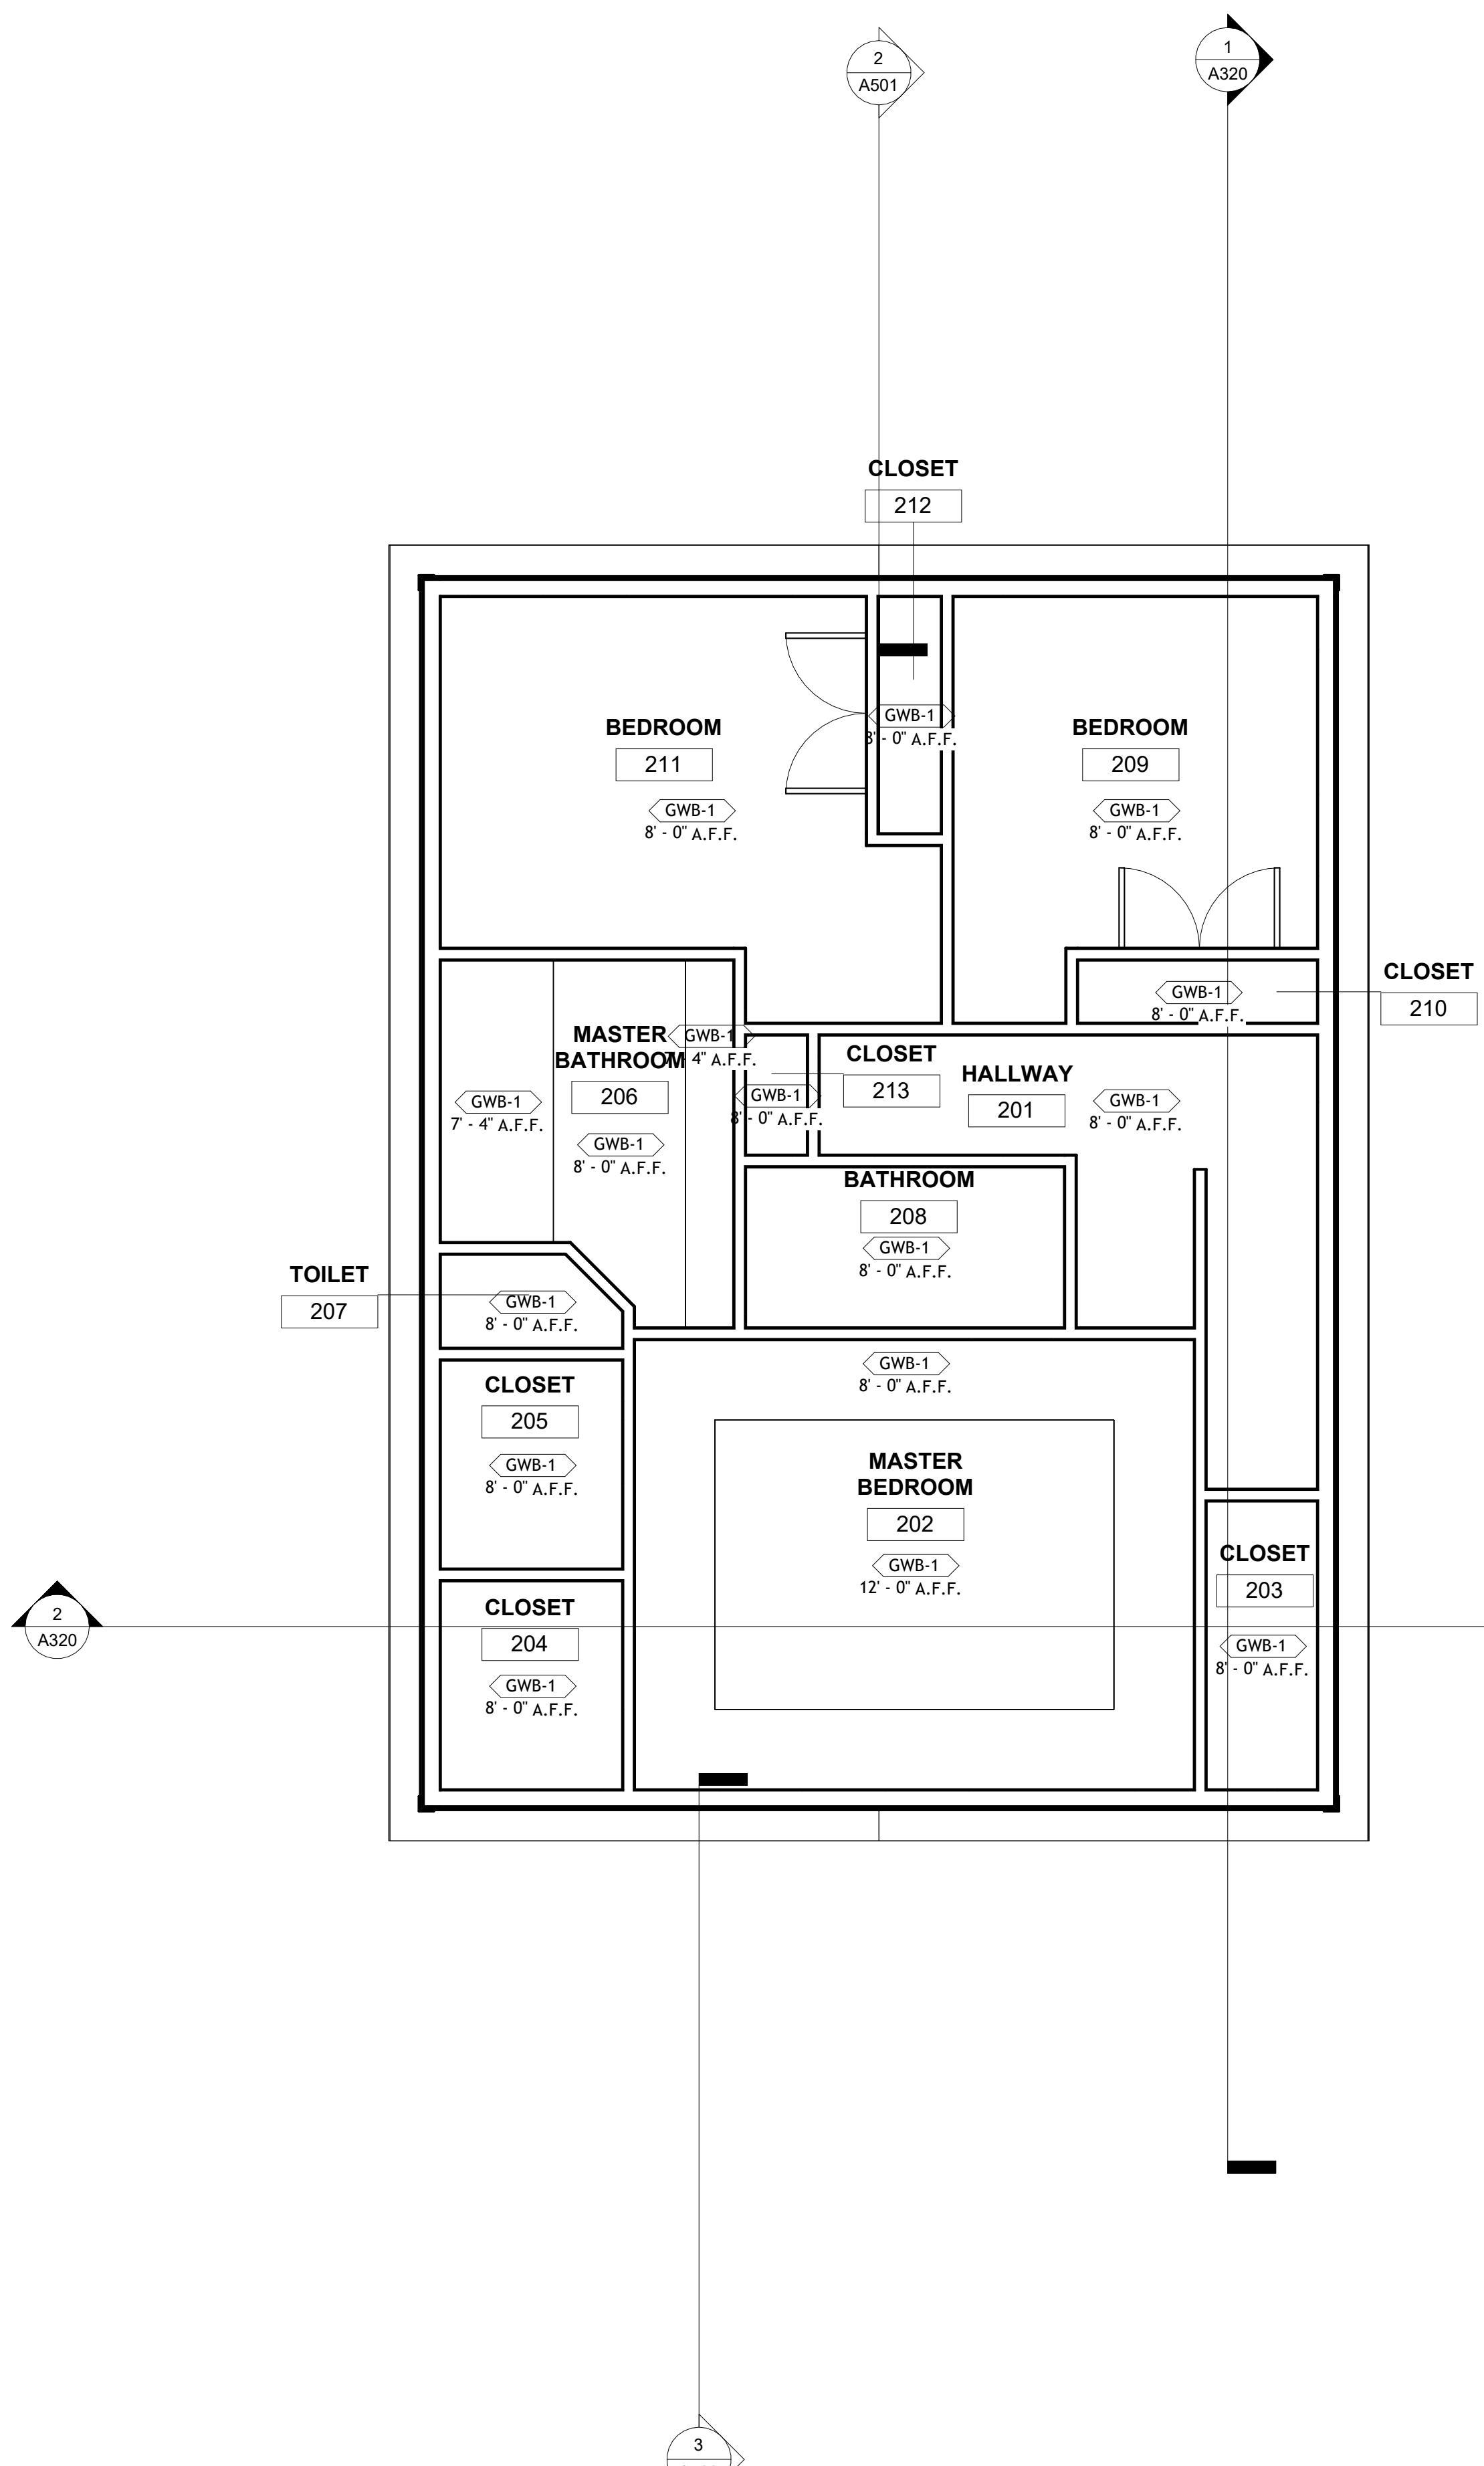
REFLECTED CEILING PLAN
GENERAL NOTES

- REFER TO A125 FOR FINISH SCHEDULE
- REFER TO DOOR DETAILS FOR SILL TRANSITIONS UNDER THE DOOR
- ALL FLOORING TRANSITIONS TO OCCUR BEHIND AND AT CENTER OF DOOR UNO


FINISH LEGEND

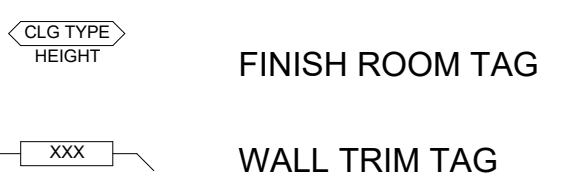

CEILING MATERIAL GRAPHICS

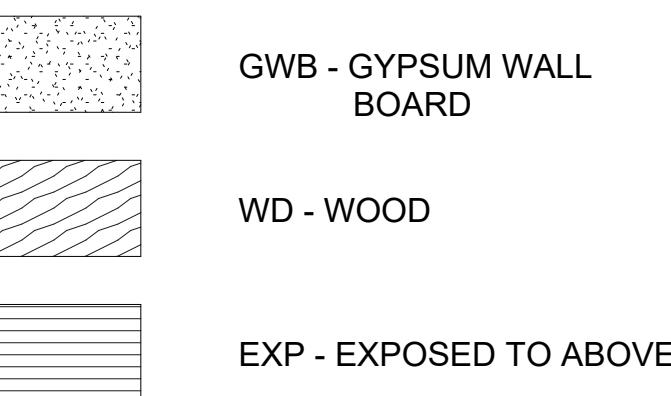

Architect Seal

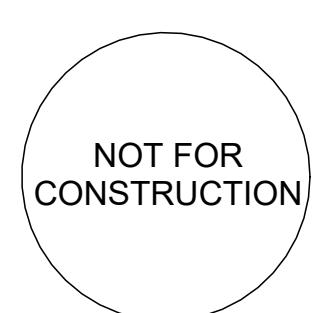**SINGLE FAMILY HOUSE
4 BEDROOM 3.5 BATH****CIOFFI FAMILY**404 PEACHTREE CIRCLE
ATLANTA, GA 30318

Project number 2023.001
Issue Date 09.06.23

CONSTRUCTION DOCUMENTS



Revisions	No.	Description	Date

**SECOND FLOOR
REFLECTED CEILING
PLAN****A202**

Scale

As Indicated

Architect: Will Cioffi, AIA
 770 Peachtree St NW
 Atlanta, GA 30308
 hey@willcioffi.com

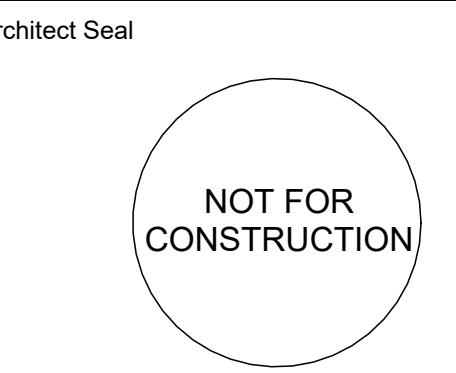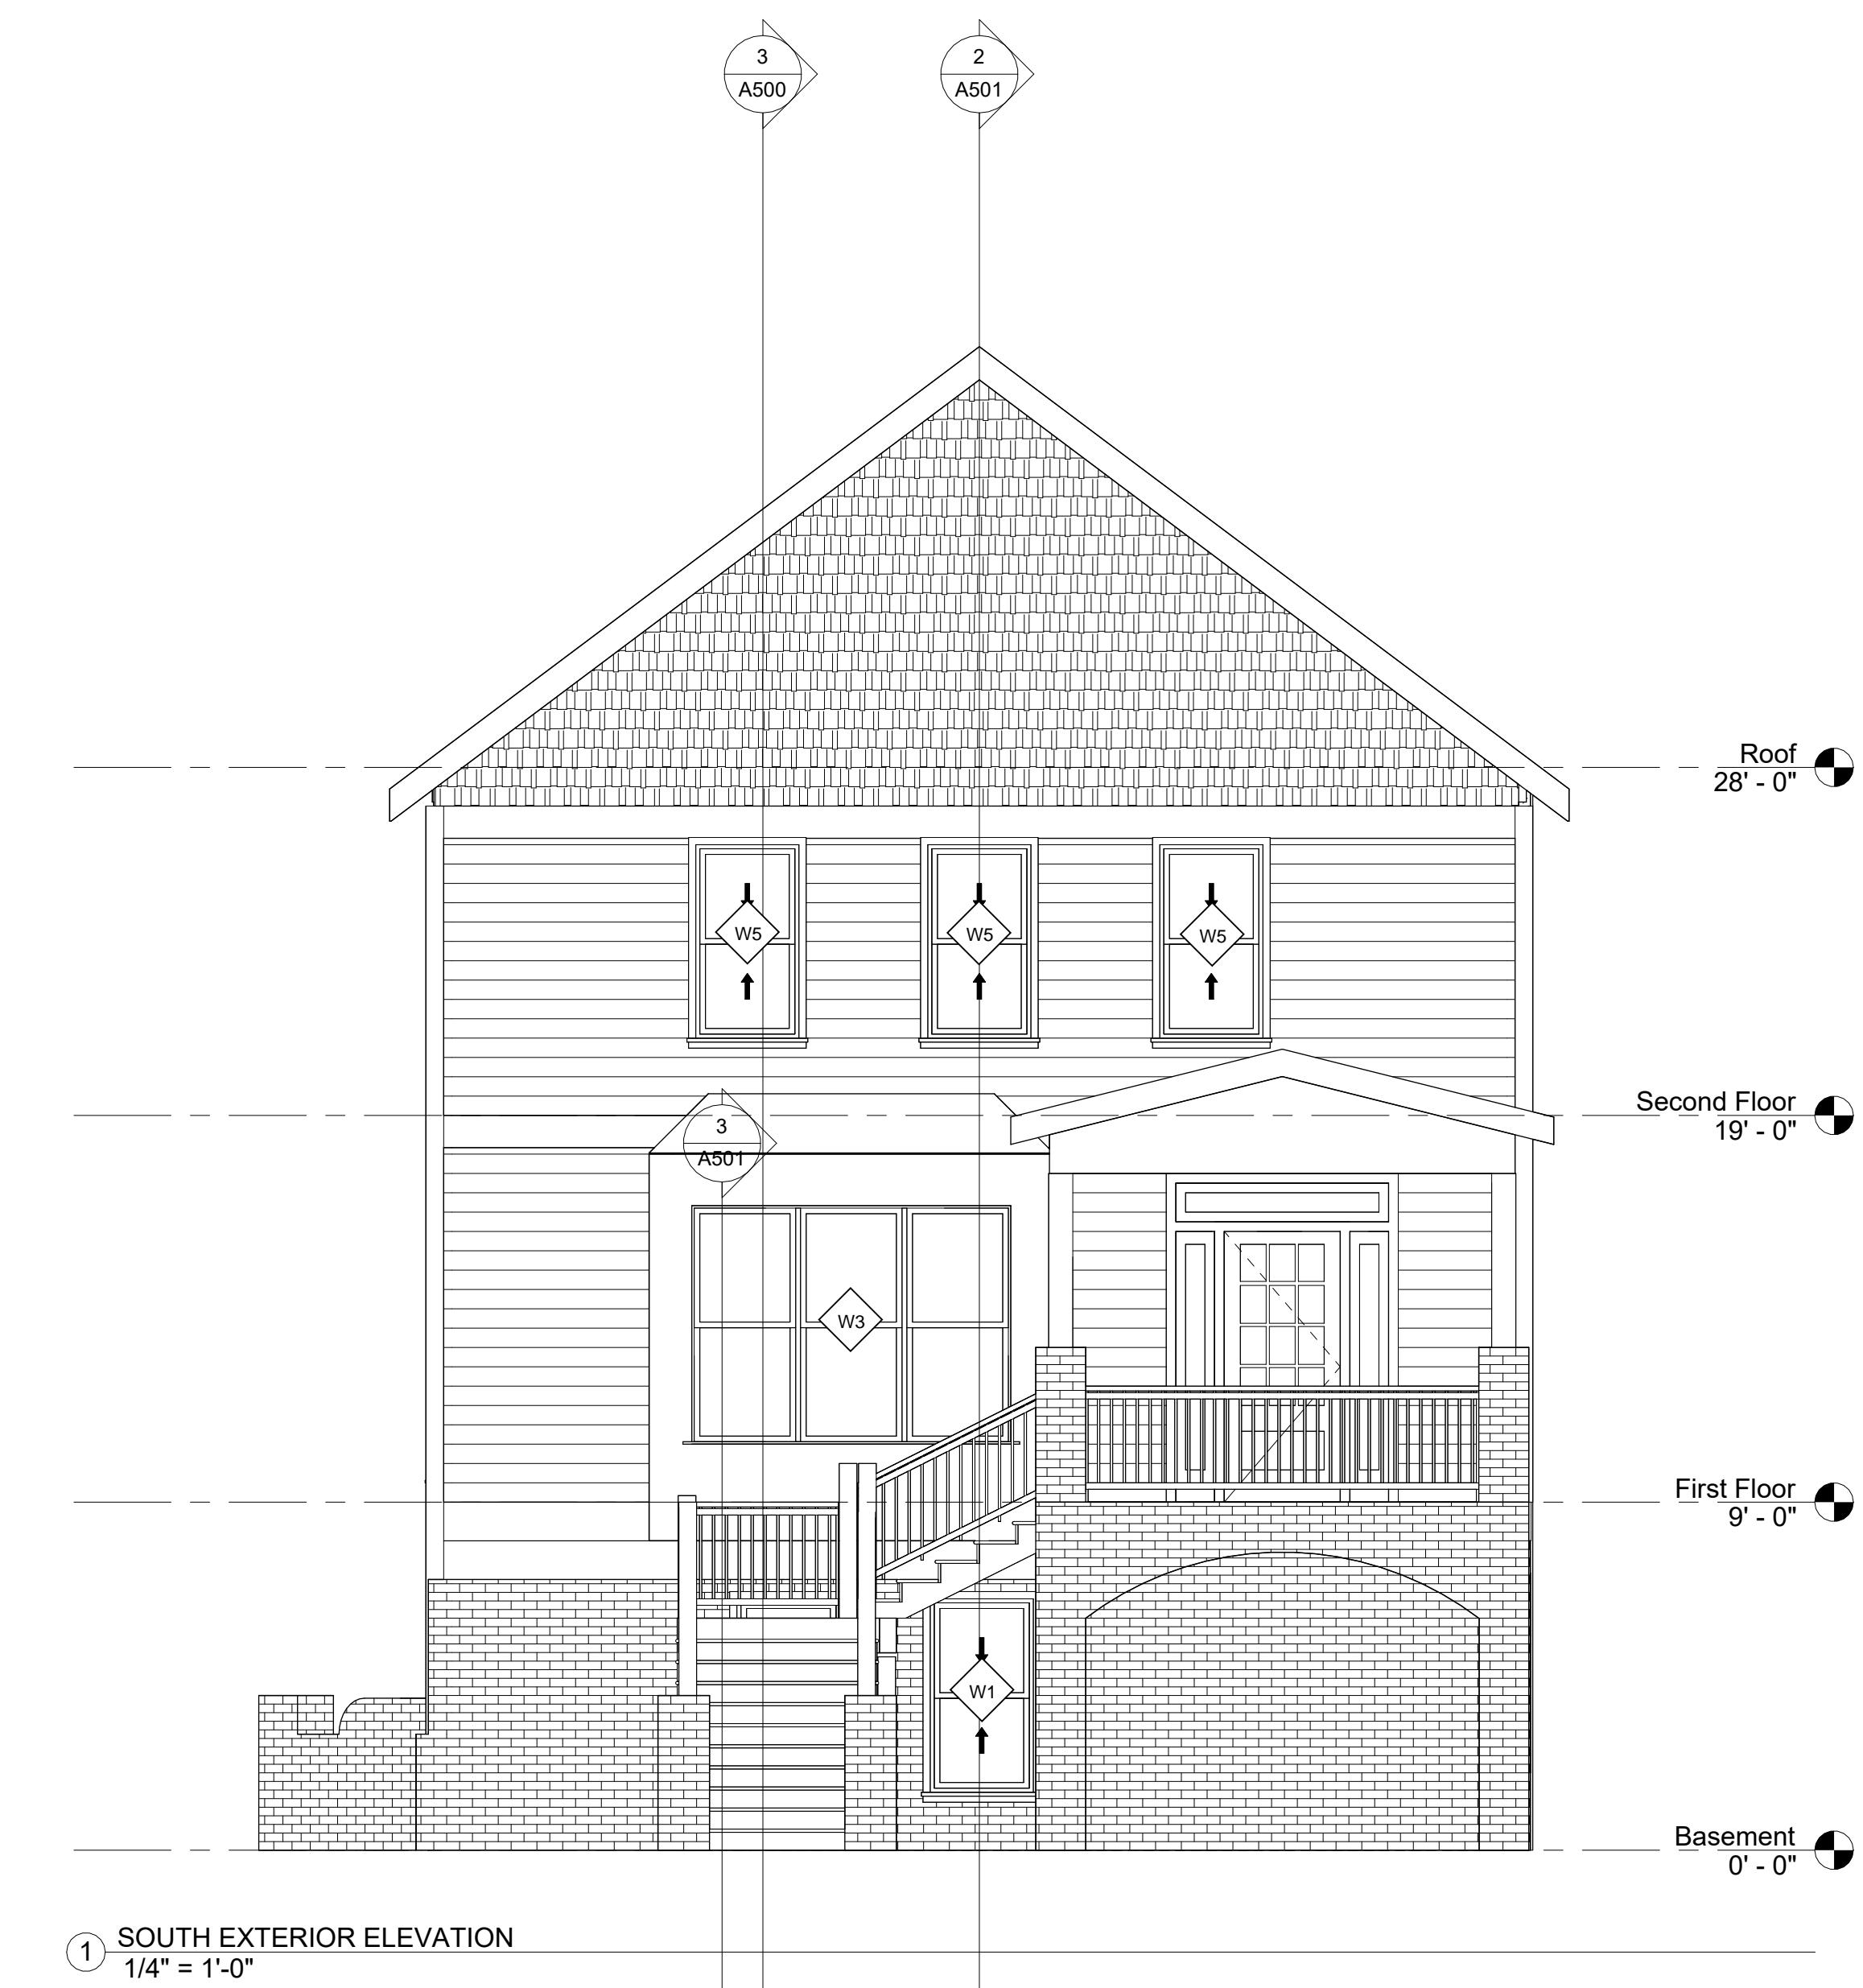

SINGLE FAMILY HOUSE 4 BEDROOM 3.5 BATH

CIOFFI FAMILY
 404 PEACHTREE CIRCLE
 ATLANTA, GA 30318

Project number 2023.001
 Issue Date 09.06.23

CONSTRUCTION DOCUMENTS


No.	Description	Date
-----	-------------	------

EXTERIOR ELEVATIONS


A300

Scale


As Indicated

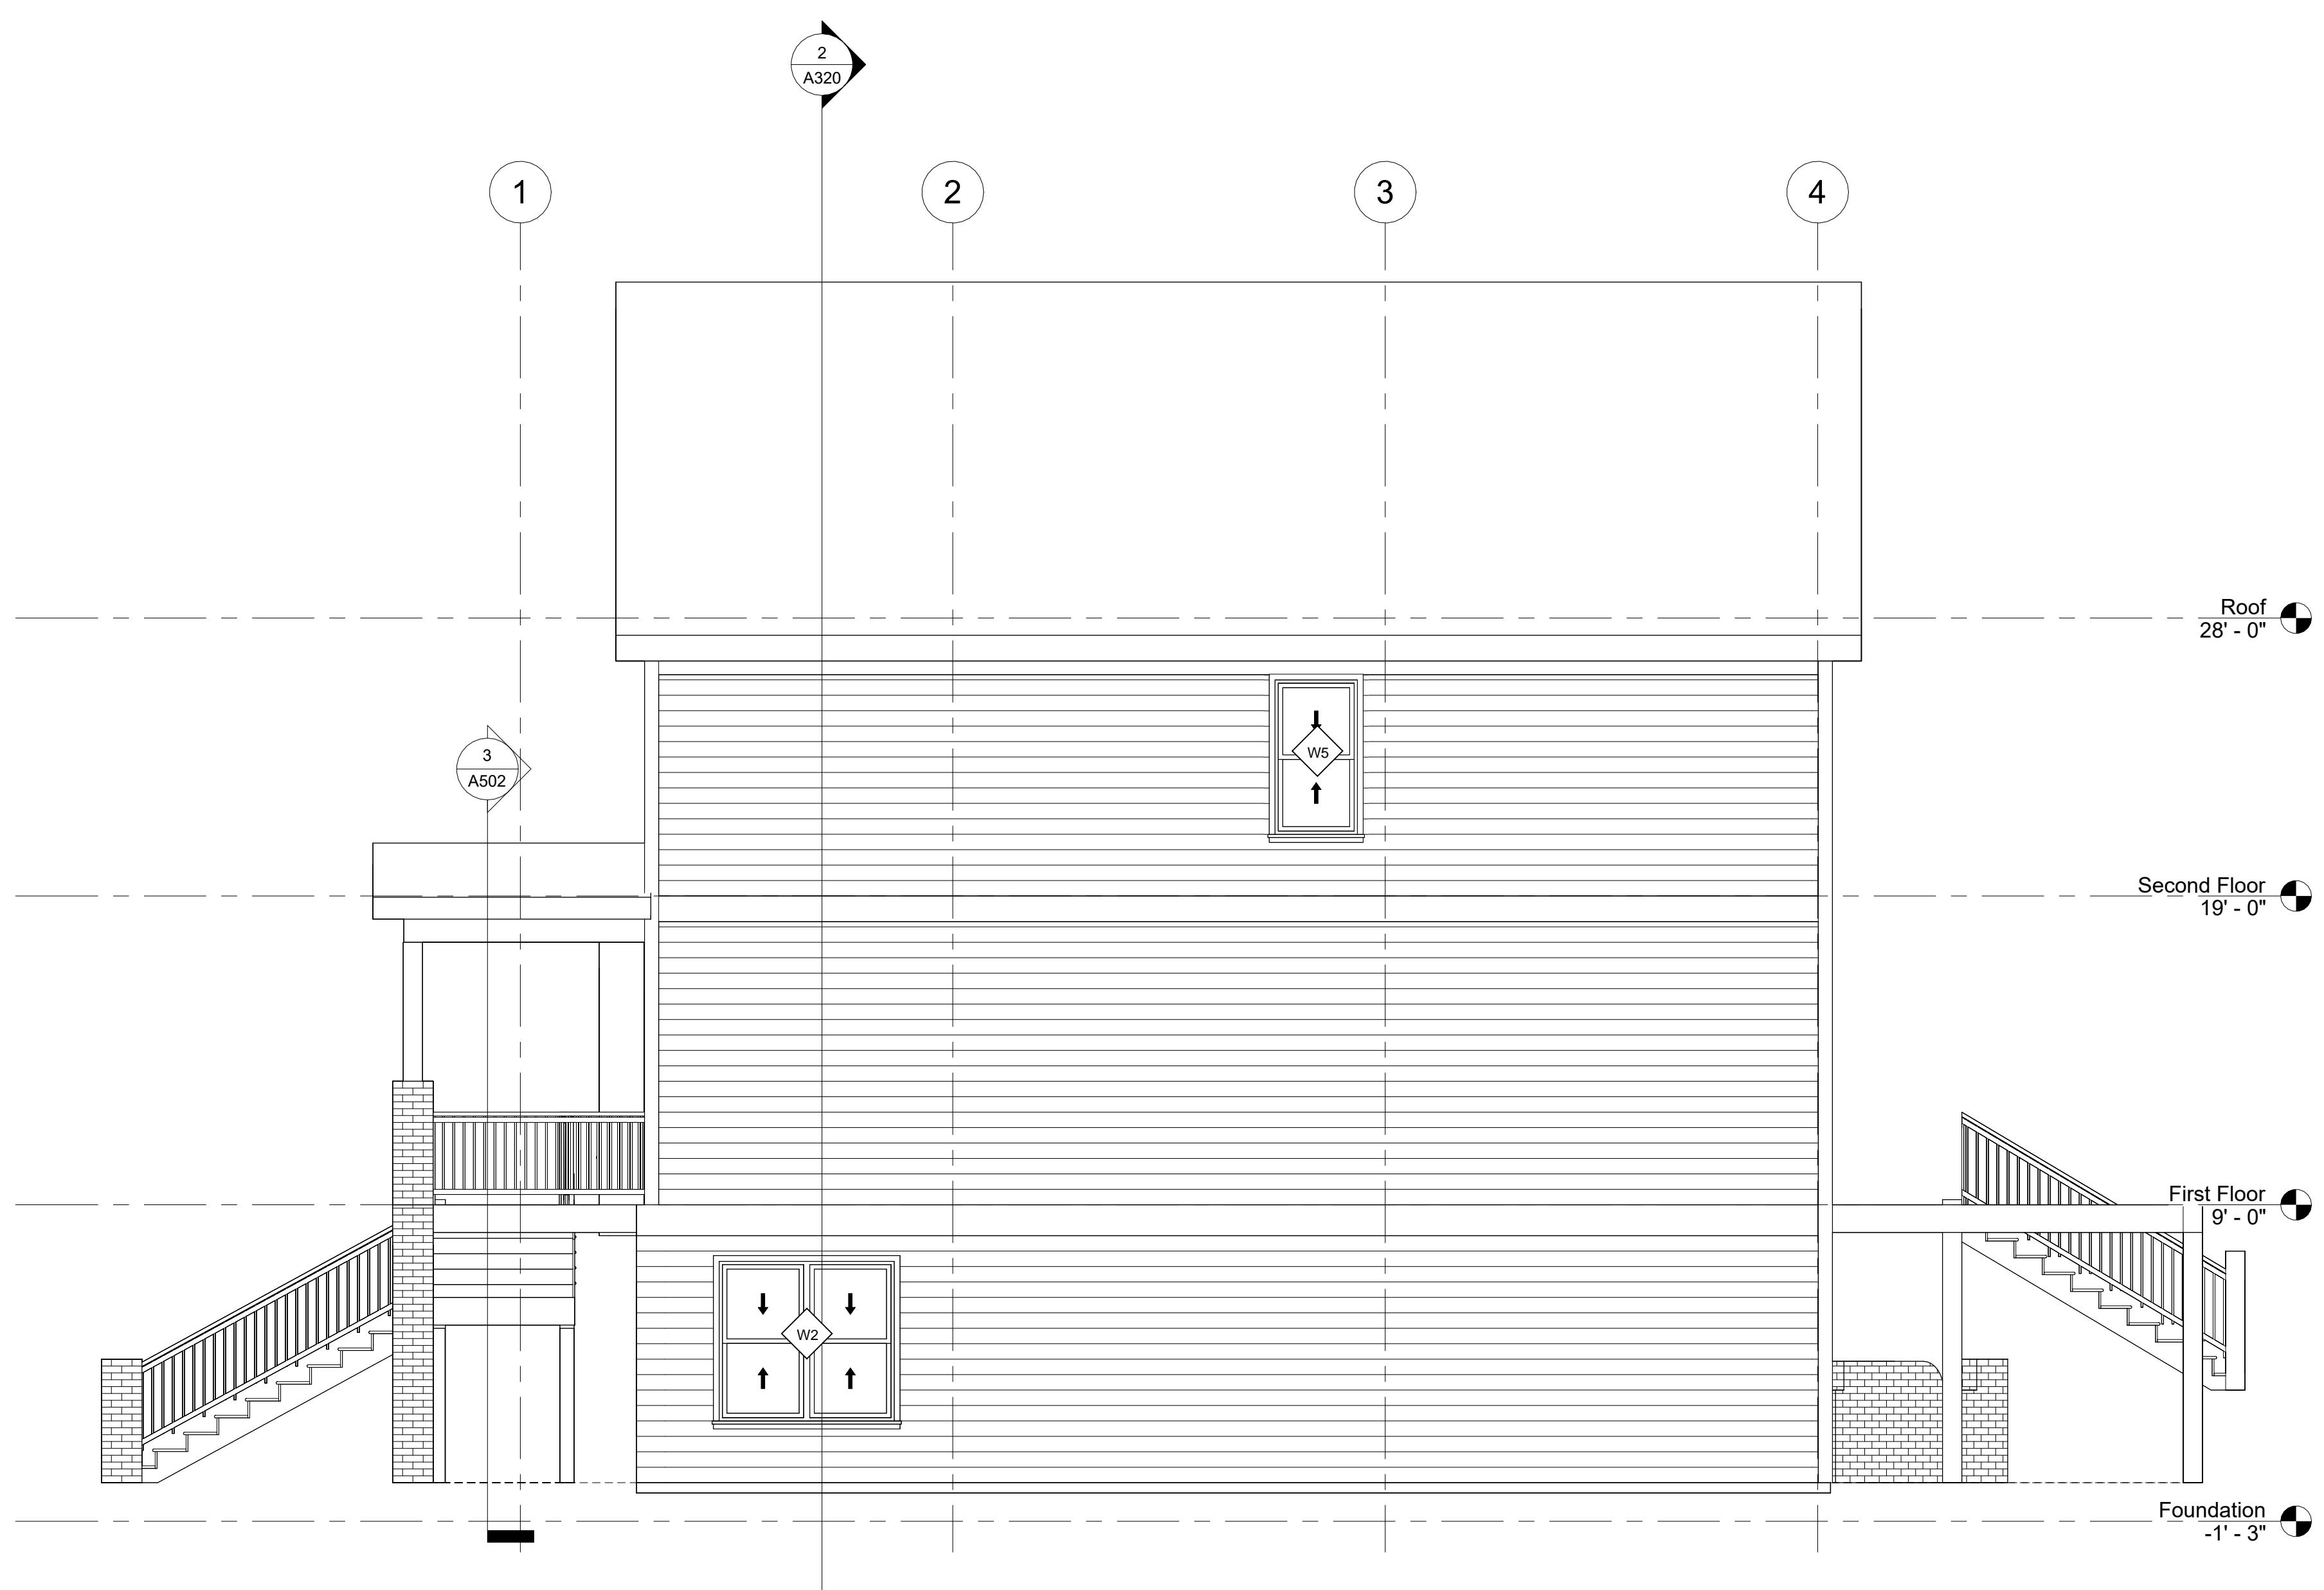

② EAST EXTERIOR ELEVATION
 $1/4'' = 1'-0''$

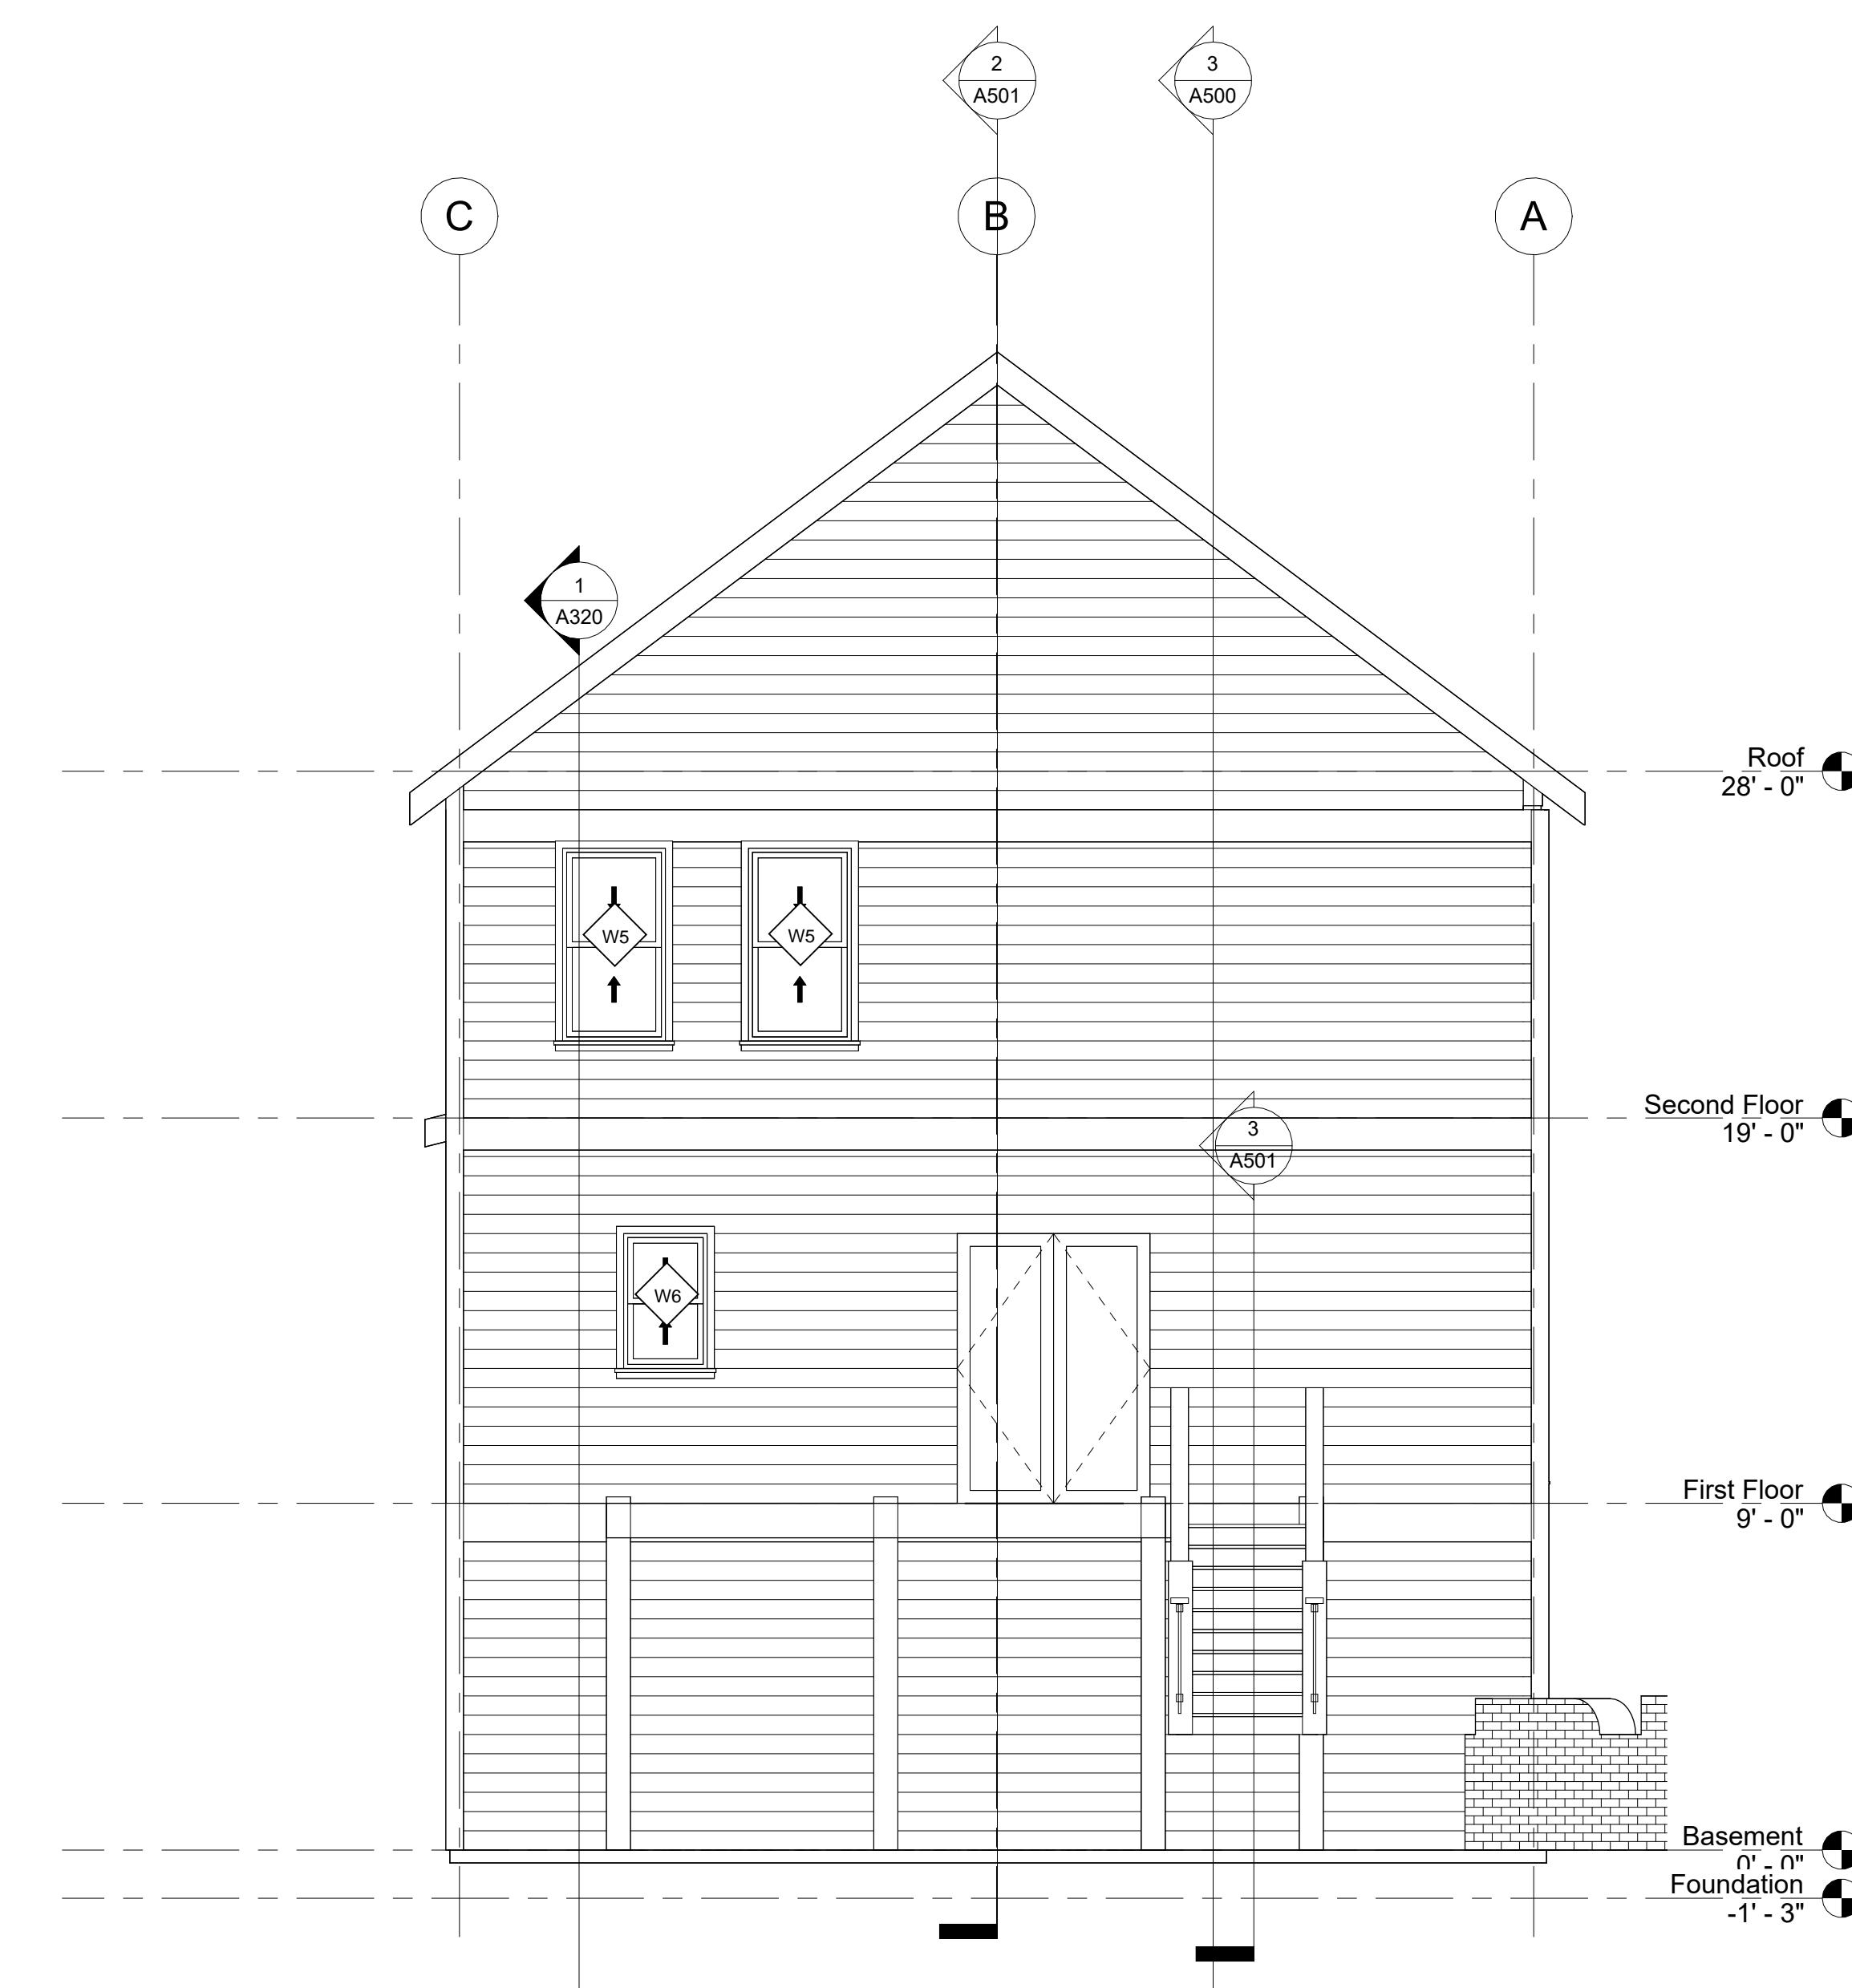

① NORTH EXTERIOR ELEVATION
 $1/4'' = 1'-0''$

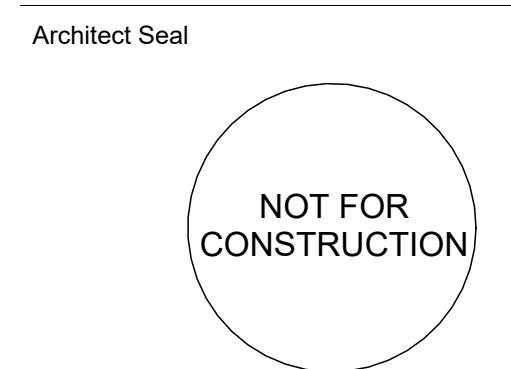

SINGLE FAMILY HOUSE 4 BEDROOM 3.5 BATH




CIOFFI FAMILY
 404 PEACHTREE CIRCLE
 ATLANTA, GA 30318

Project number 2023.001
 Issue Date 09.06.23

CONSTRUCTION DOCUMENTS

No.	Description	Date
-----	-------------	------

Architect: Will Cioffi, AIA
 770 Peachtree St NW
 Atlanta, GA 30308
 hey@willcioffi.com

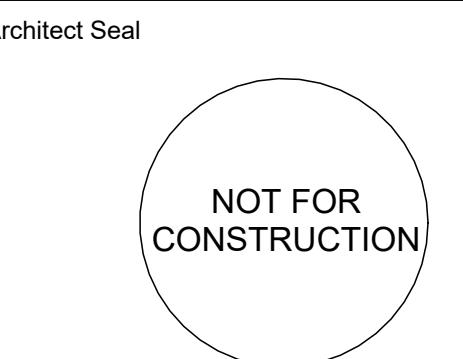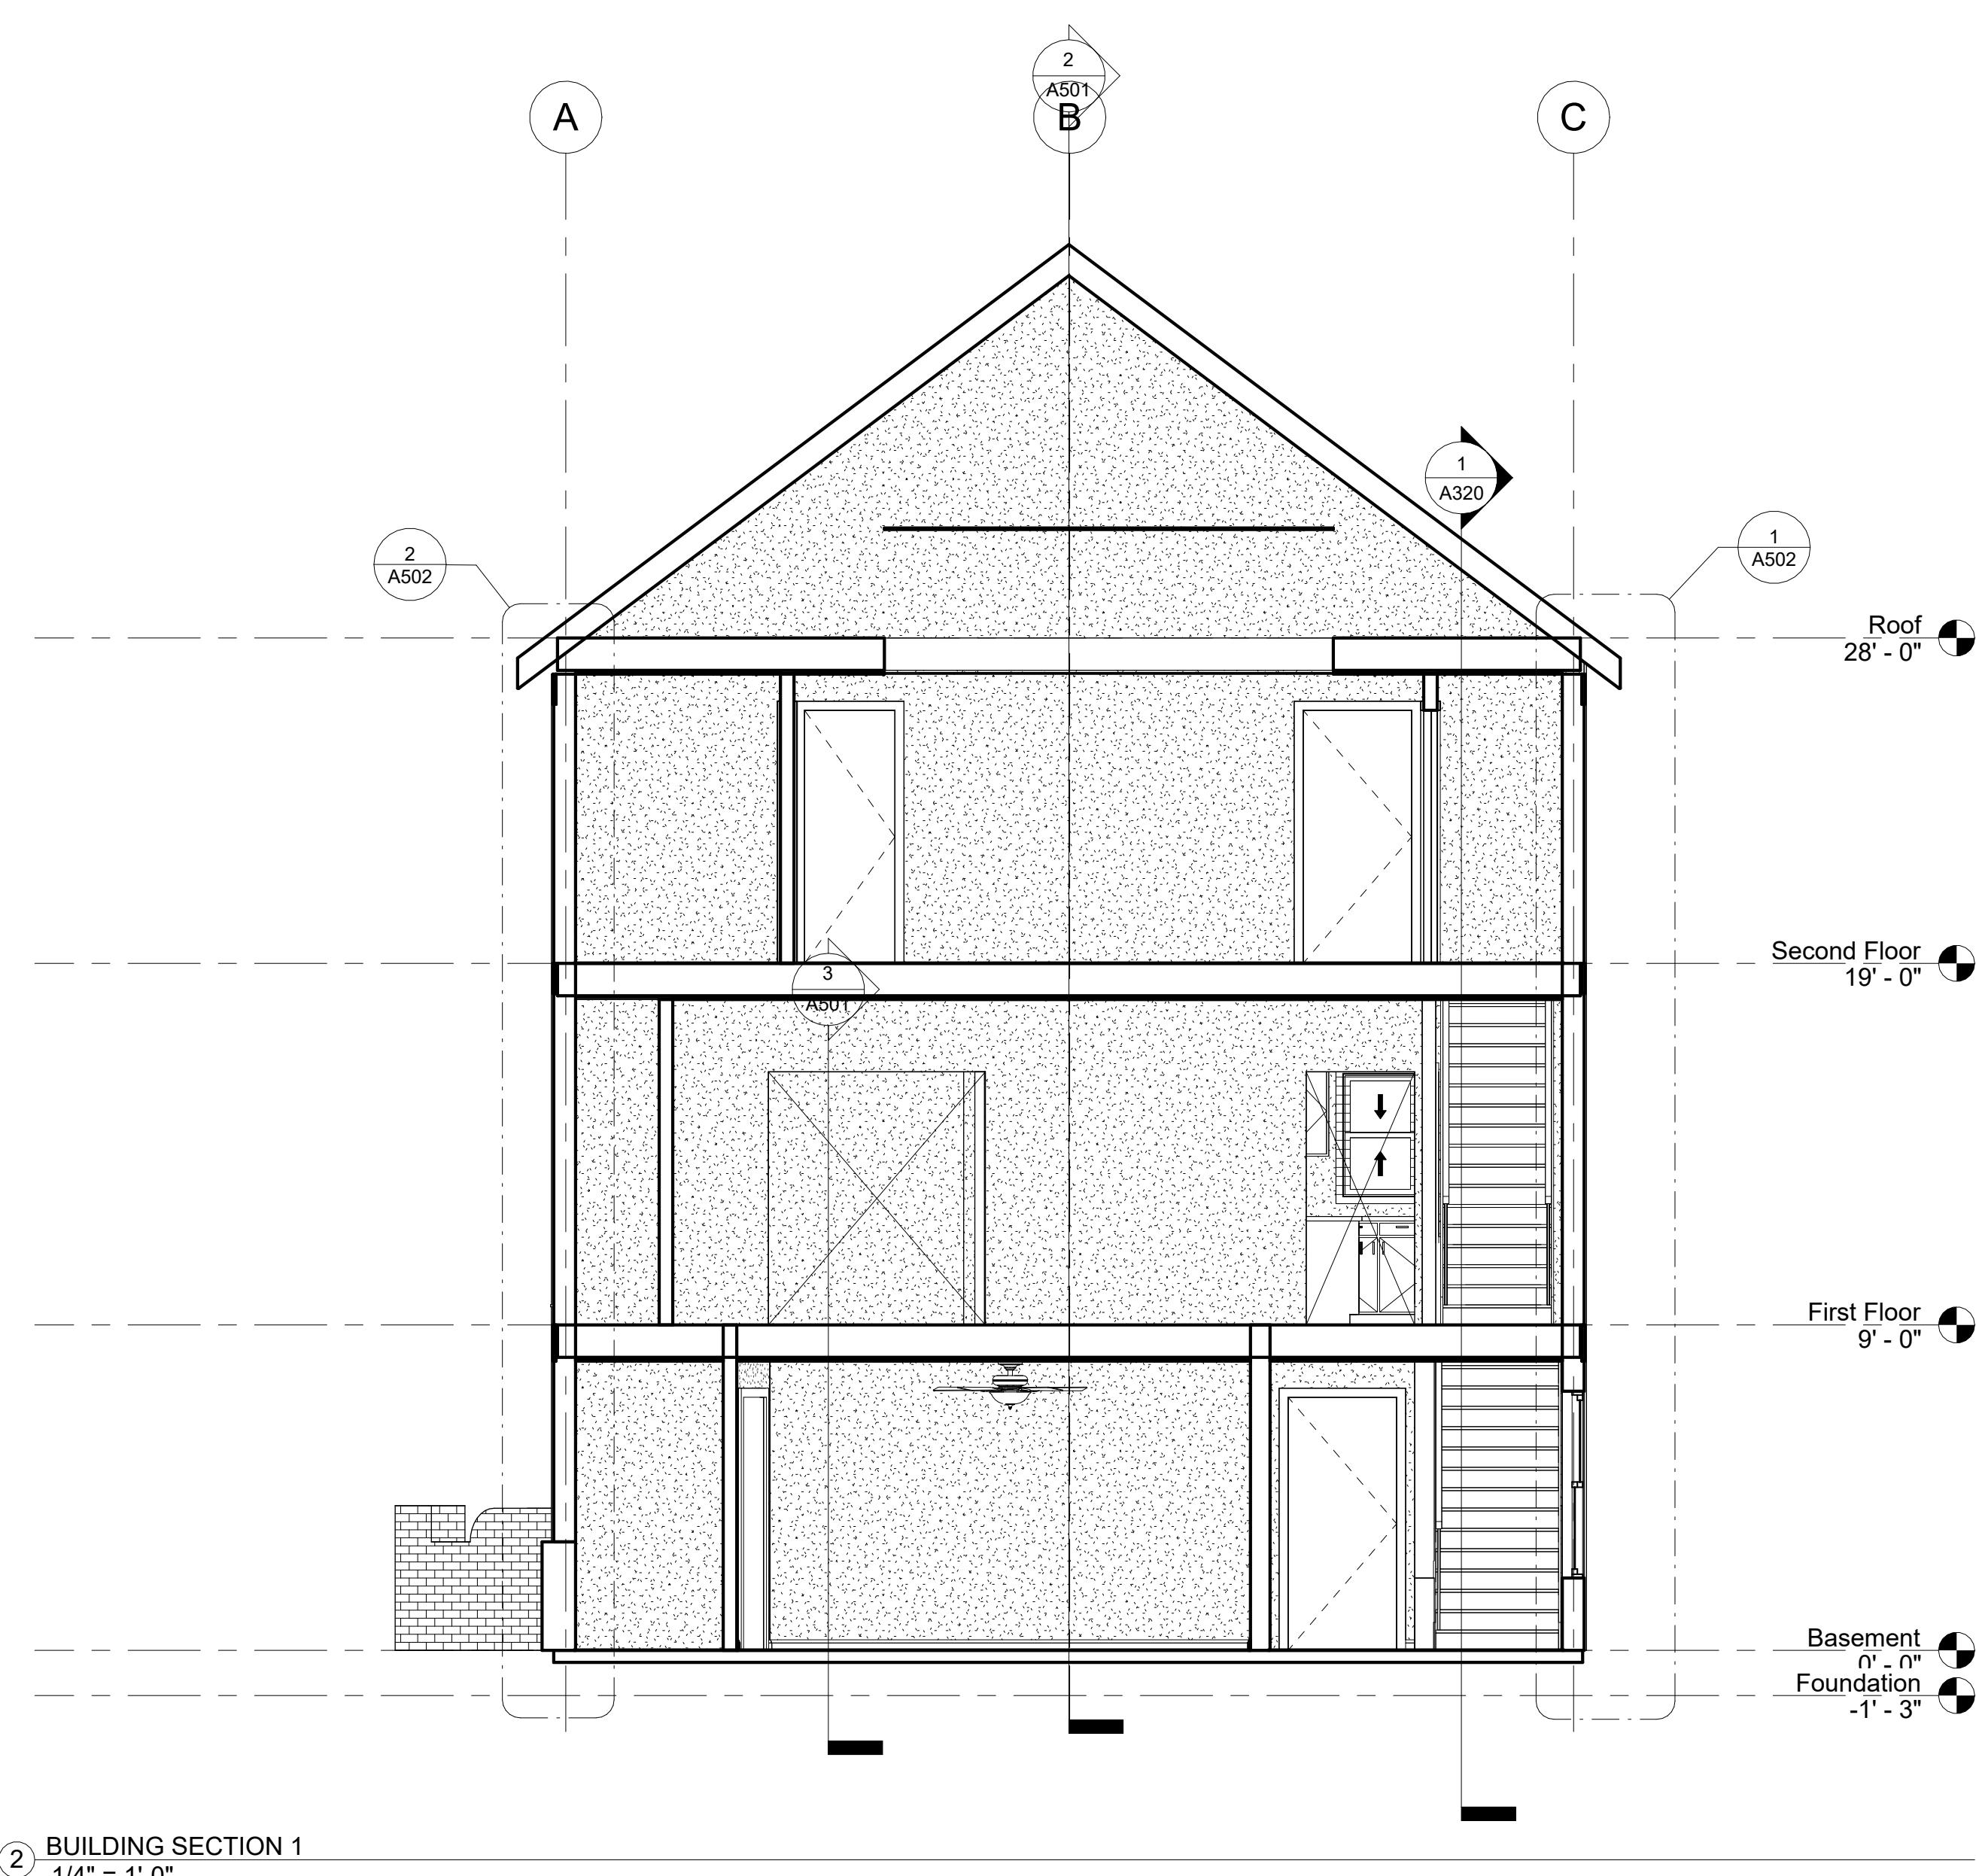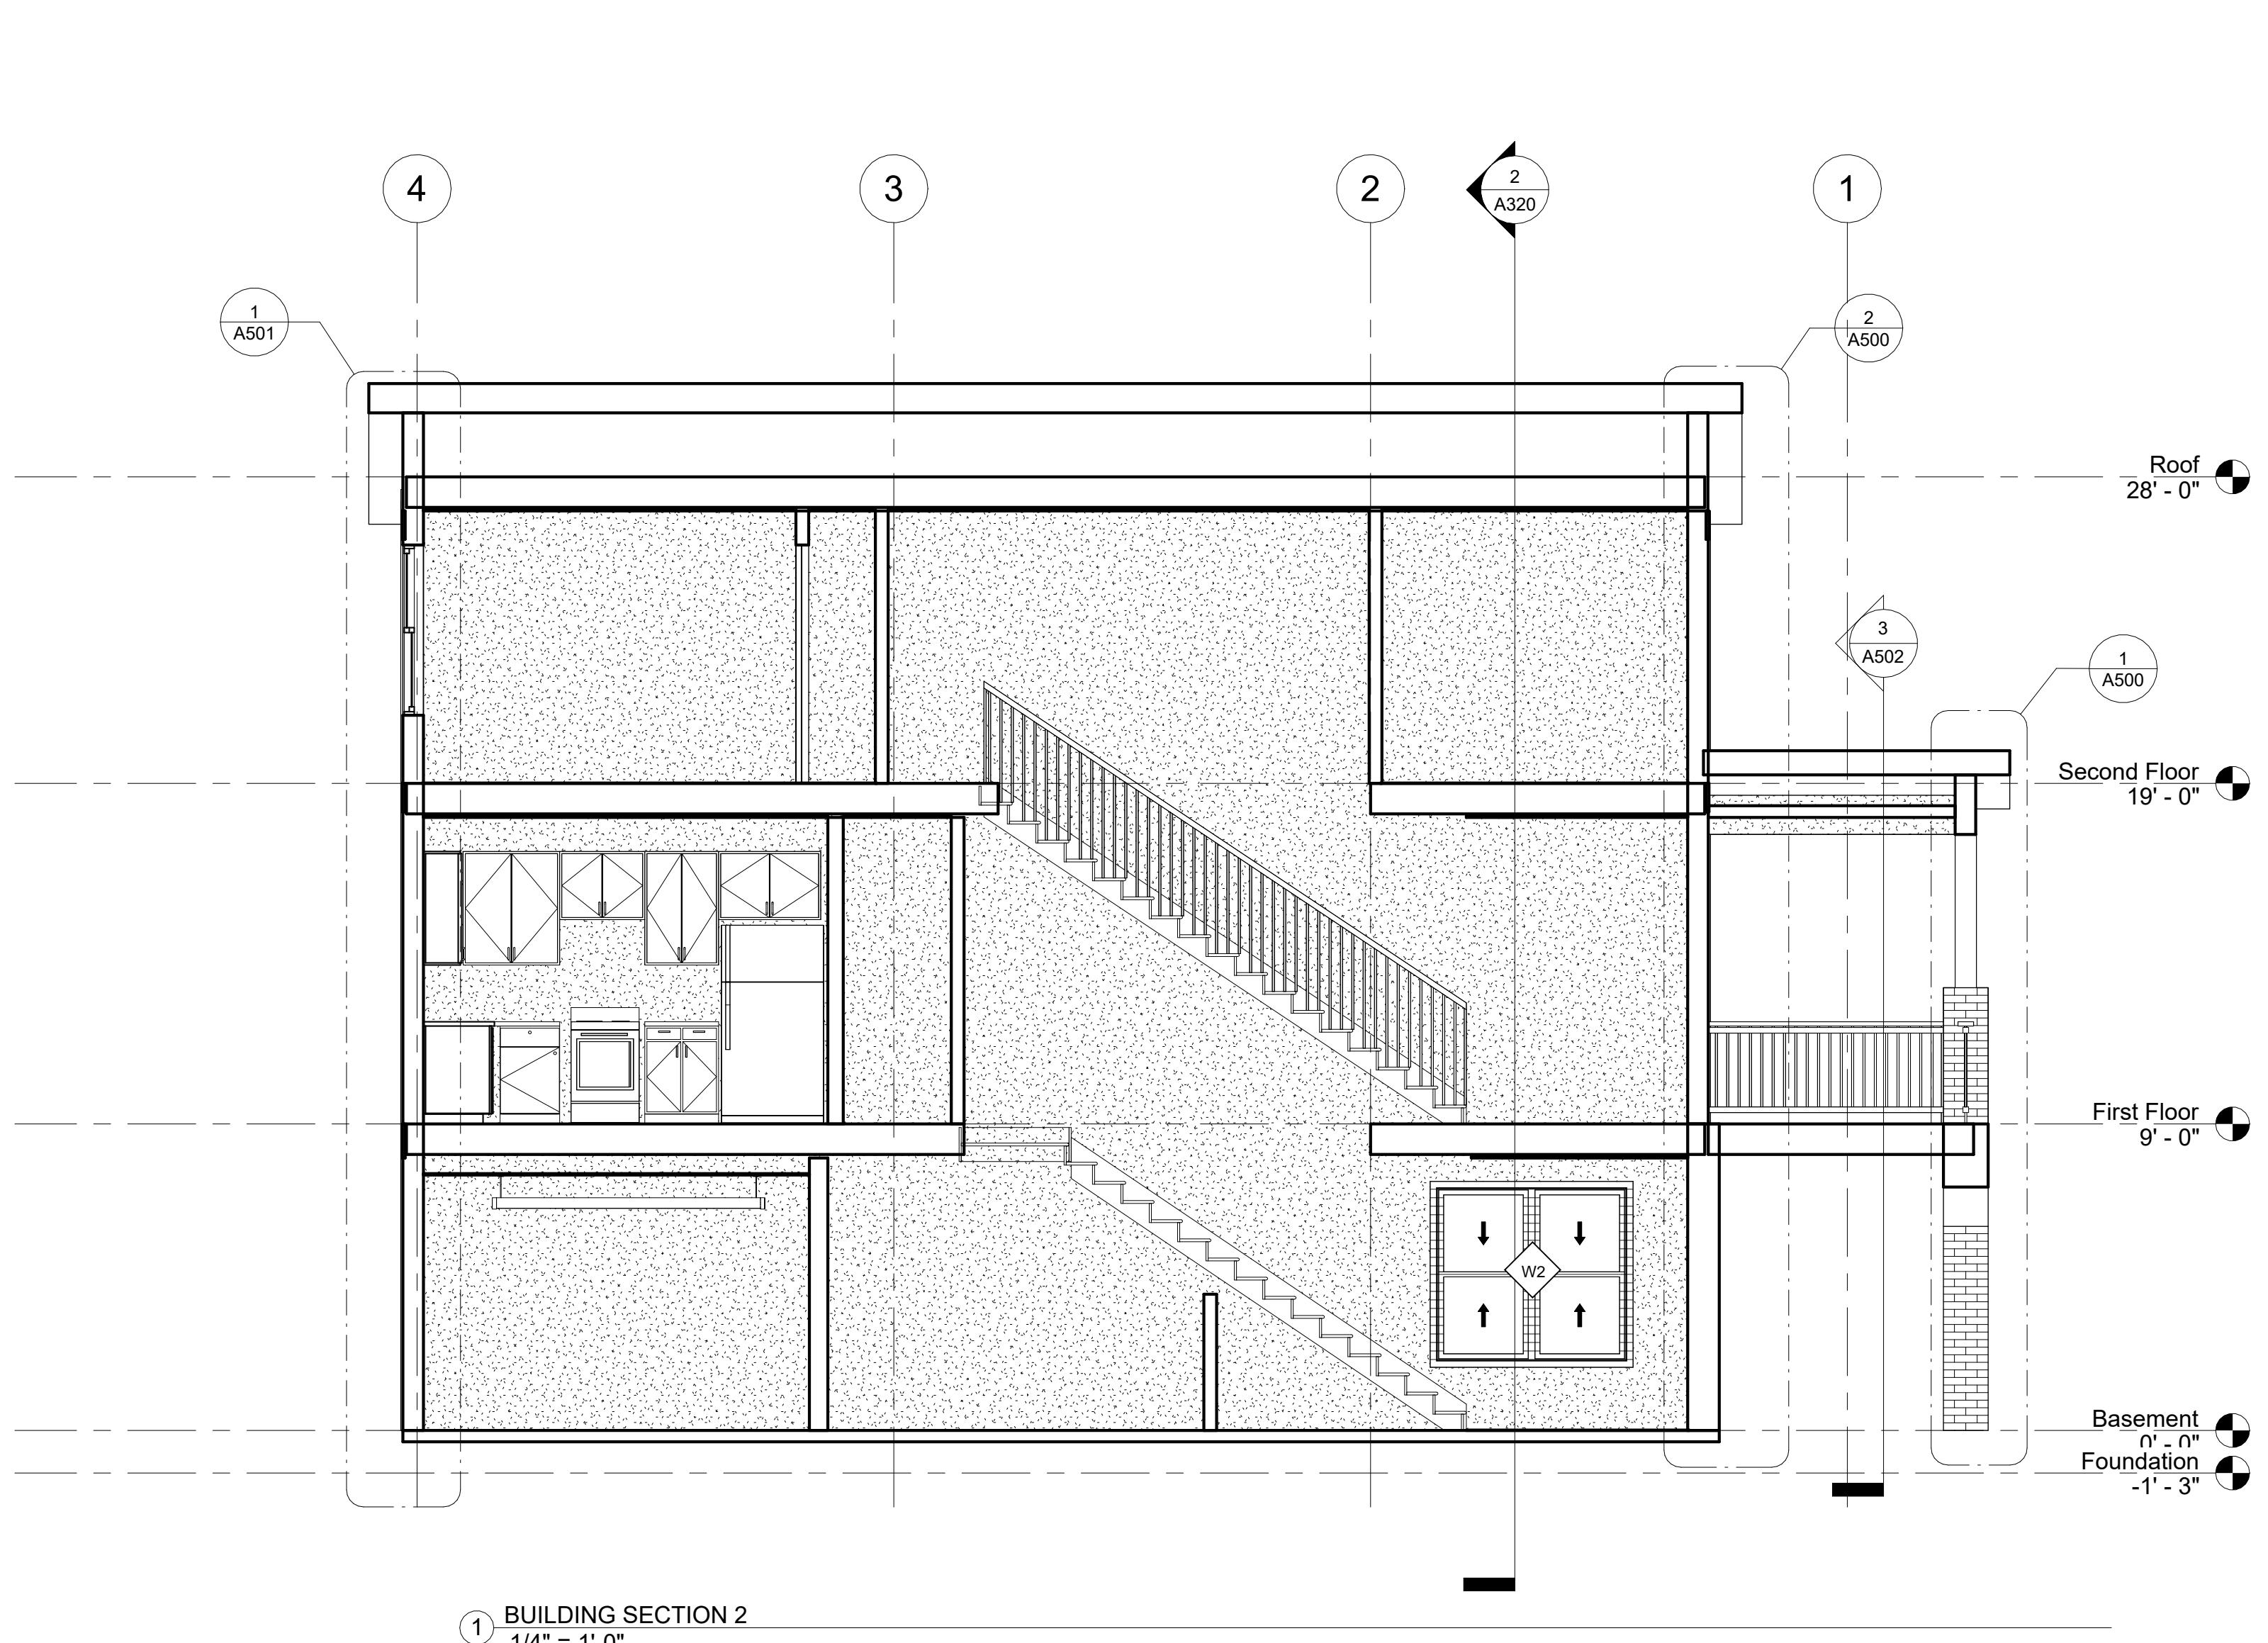

SINGLE FAMILY HOUSE 4 BEDROOM 3.5 BATH

CIOFFI FAMILY
 404 PEACHTREE CIRCLE
 ATLANTA, GA 30318


Project number 2023.001
 Issue Date 09.06.23

CONSTRUCTION DOCUMENTS


No.	Description	Date
-----	-------------	------

BUILDING SECTIONS

A320

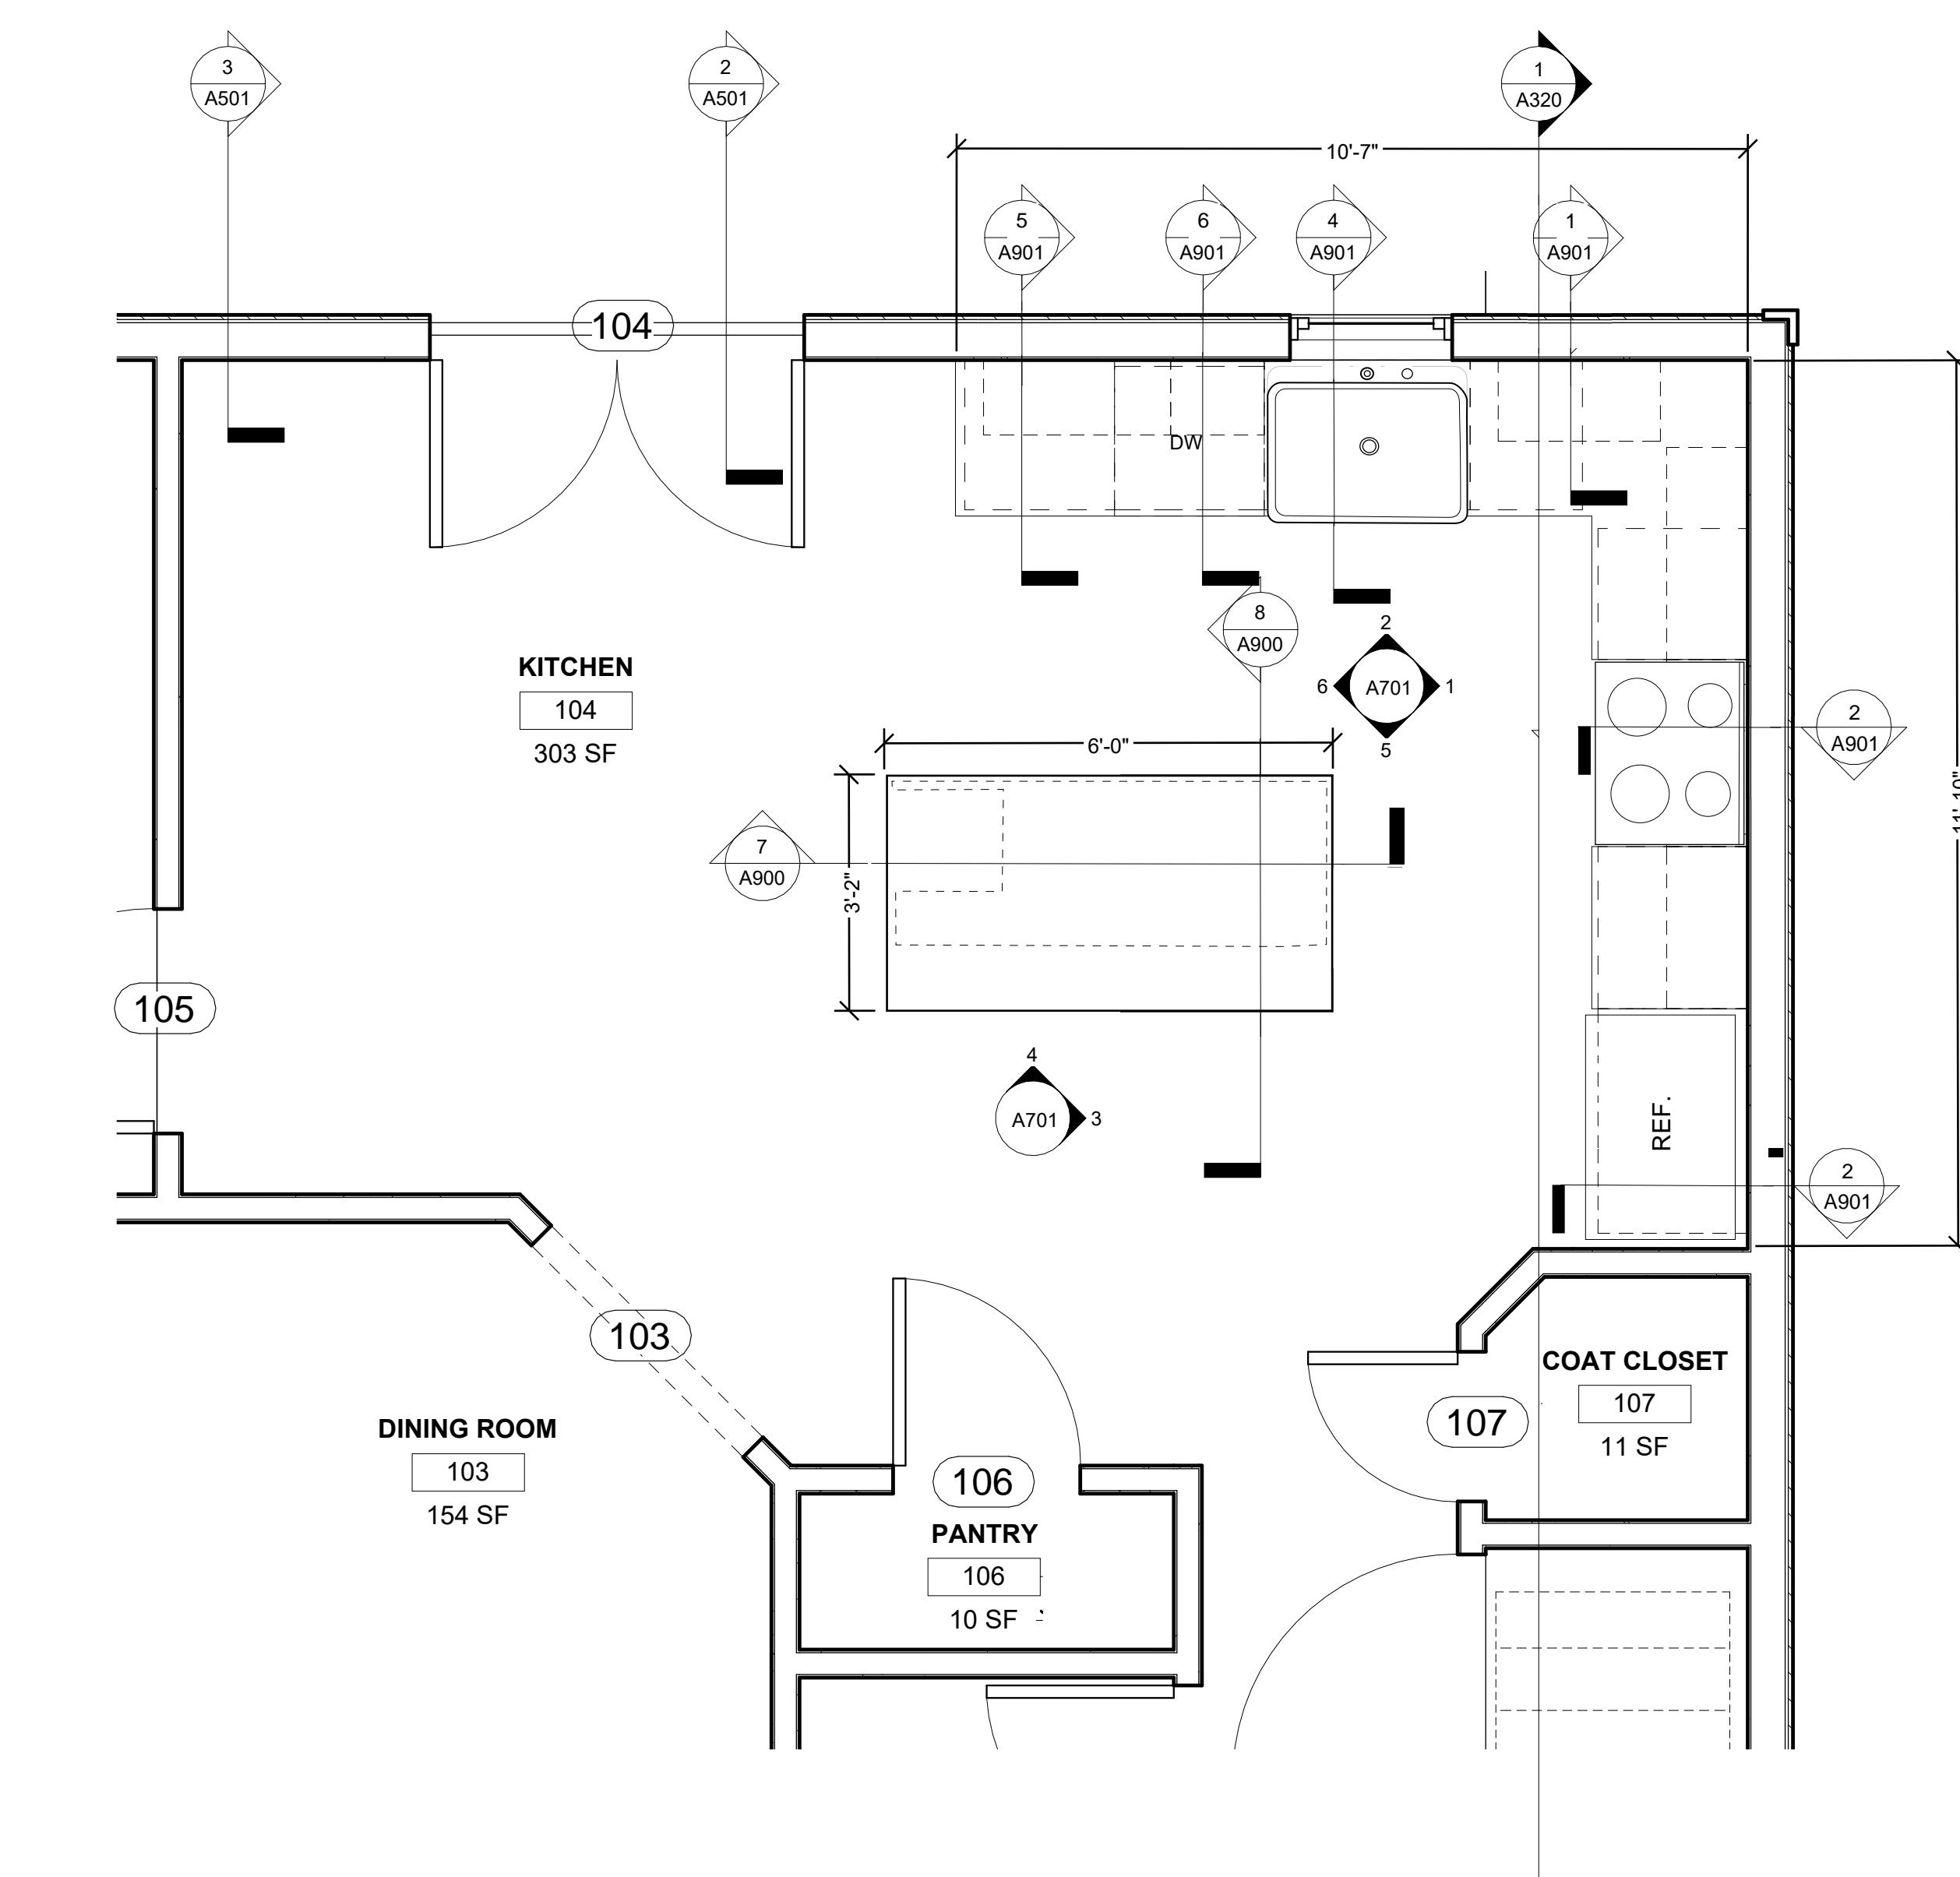

① ENLARGED PLAN - KITCHEN
1/2" = 1'-0"

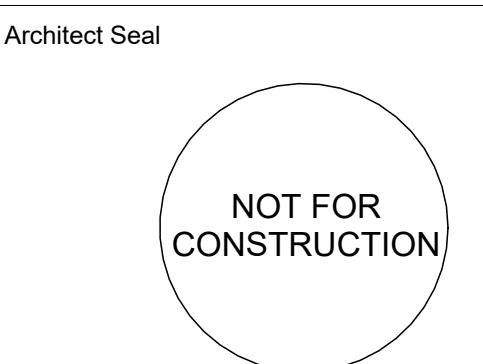

SINGLE FAMILY HOUSE 4 BEDROOM 3.5 BATH

CIOFFI FAMILY
404 PEACHTREE CIRCLE
ATLANTA, GA 30318


Project number 2023.001
Issue Date 09.06.23

CONSTRUCTION DOCUMENTS


Revisions
No. Description Date

ENLARGED FLOOR
PLANS

A400

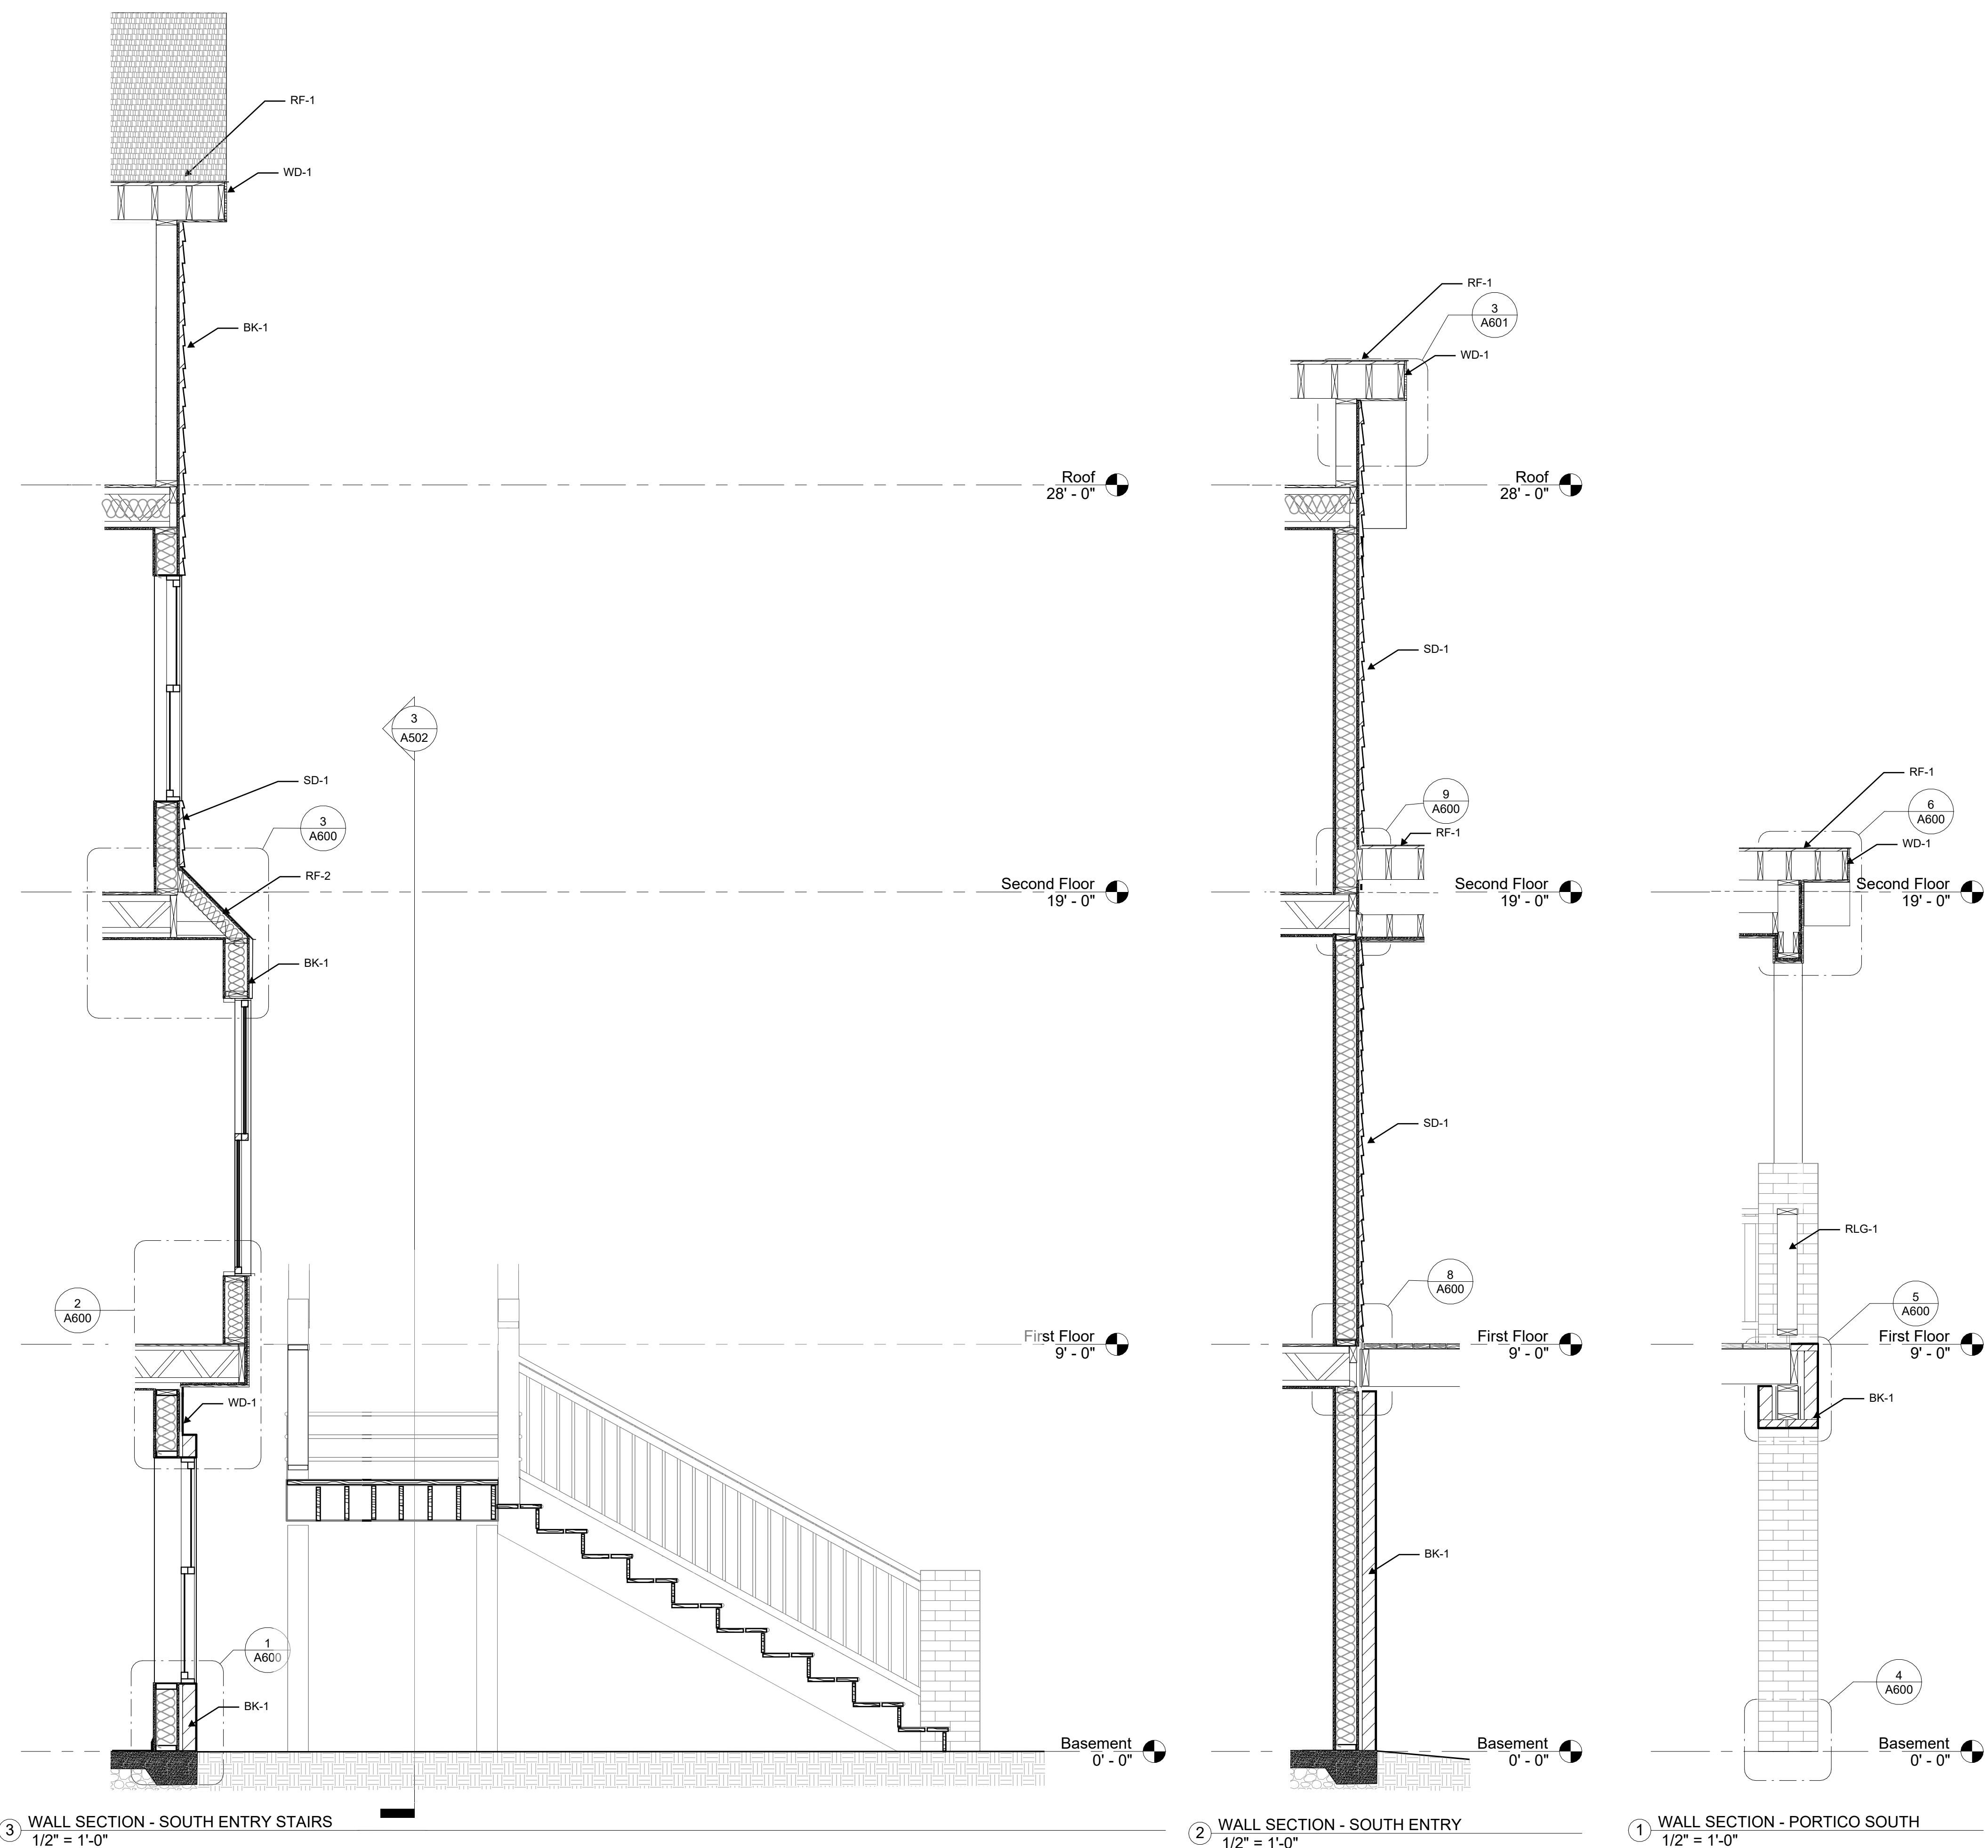


Architect: Will Cioffi, AIA
 770 Peachtree St NW
 Atlanta, GA 30308
 hey@willcioffi.com

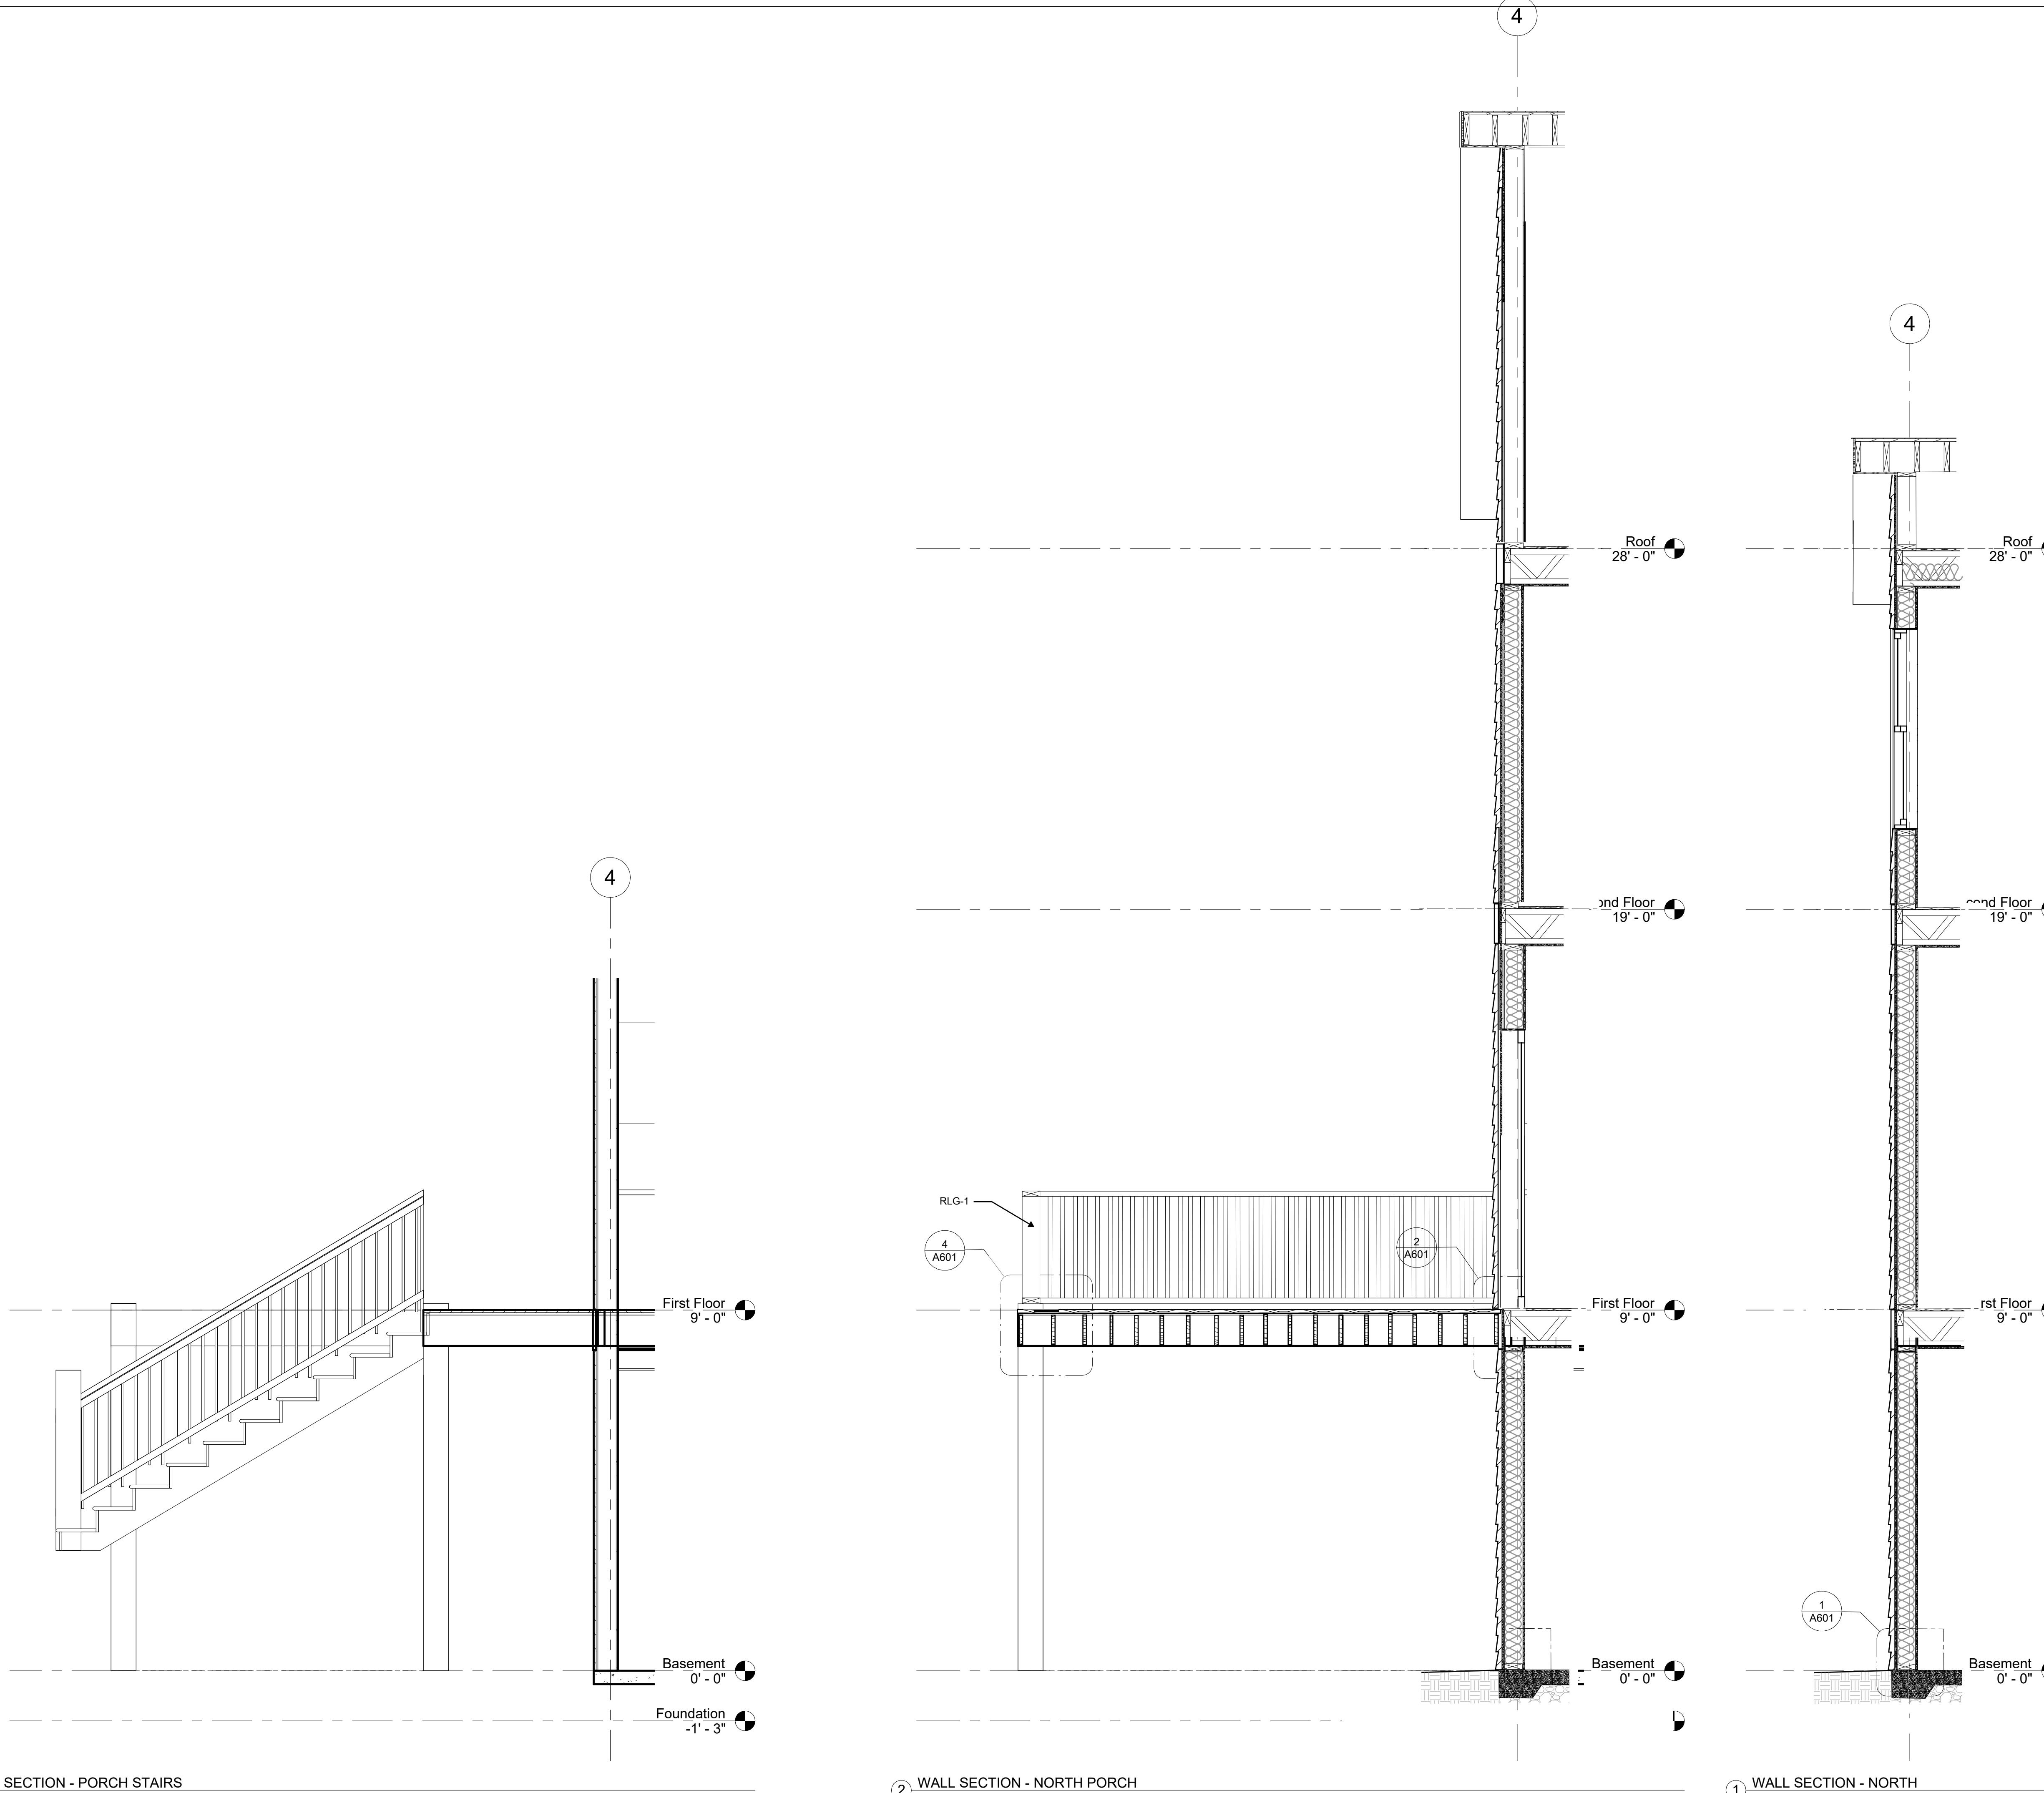

③ WALL SECTION - PORCH STAIRS
 $1/2'' = 1'-0''$

② WALL SECTION - NORTH PORCH
 $1/2'' = 1'-0''$

① WALL SECTION - NORTH
 $1/2'' = 1'-0''$

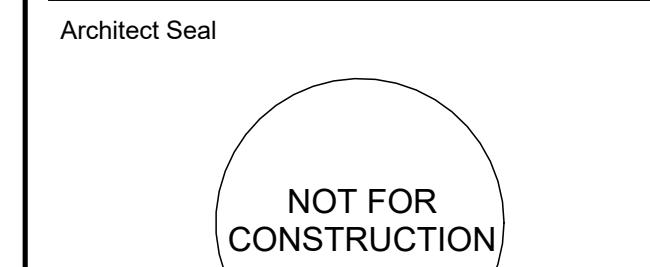

SINGLE FAMILY HOUSE 4 BEDROOM 3.5 BATH

CIOFFI FAMILY

404 PEACHTREE CIRCLE
 ATLANTA, GA 30318

Project number 2023.001
 Issue Date 09.06.23



CONSTRUCTION DOCUMENTS

No.	Description	Date
-----	-------------	------

Scale As Indicated

WALL SECTIONS

A501

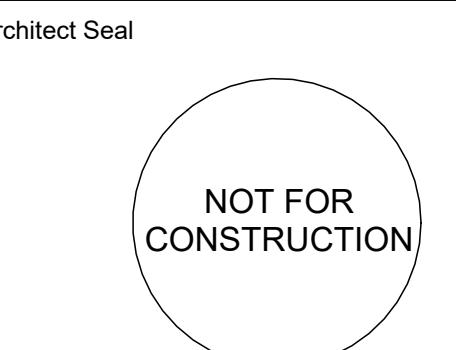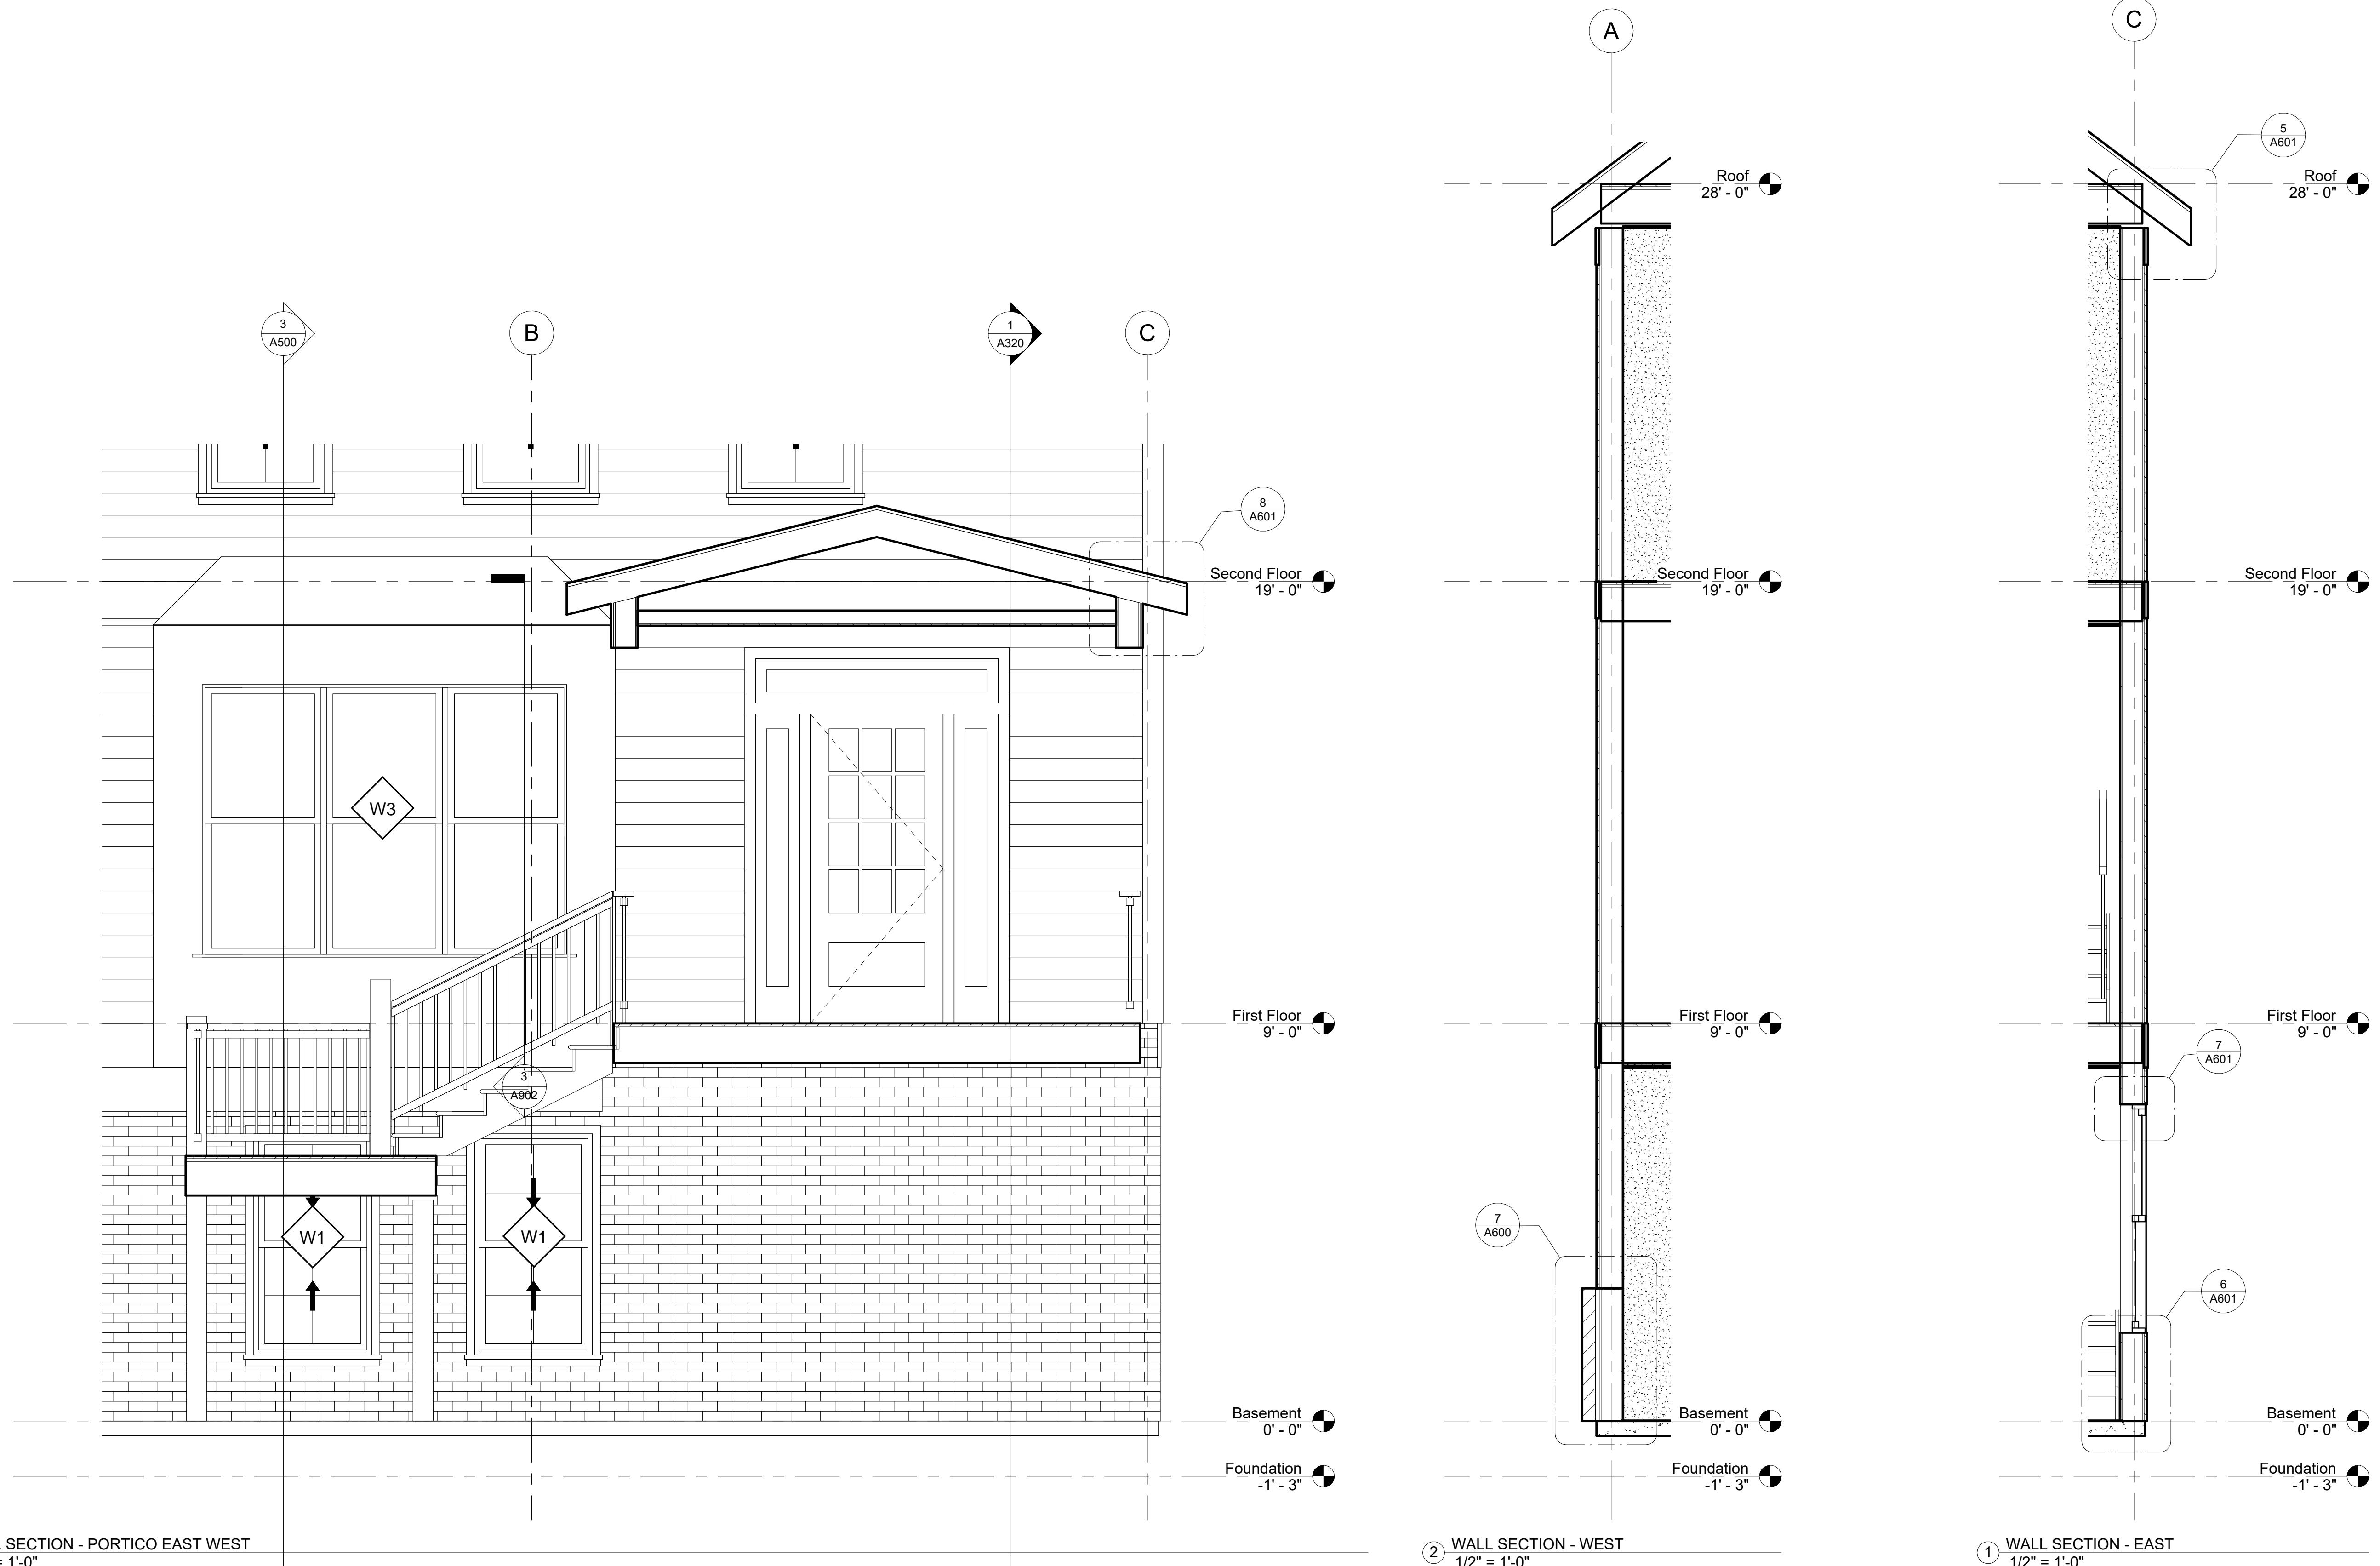

SINGLE FAMILY HOUSE 4 BEDROOM 3.5 BATH

CIOFFI FAMILY
404 PEACHTREE CIRCLE
ATLANTA, GA 30318


Project number 2023.001
Issue Date 09.06.23

CONSTRUCTION DOCUMENTS


No.	Description	Date
-----	-------------	------

WALL SECTIONS


A502

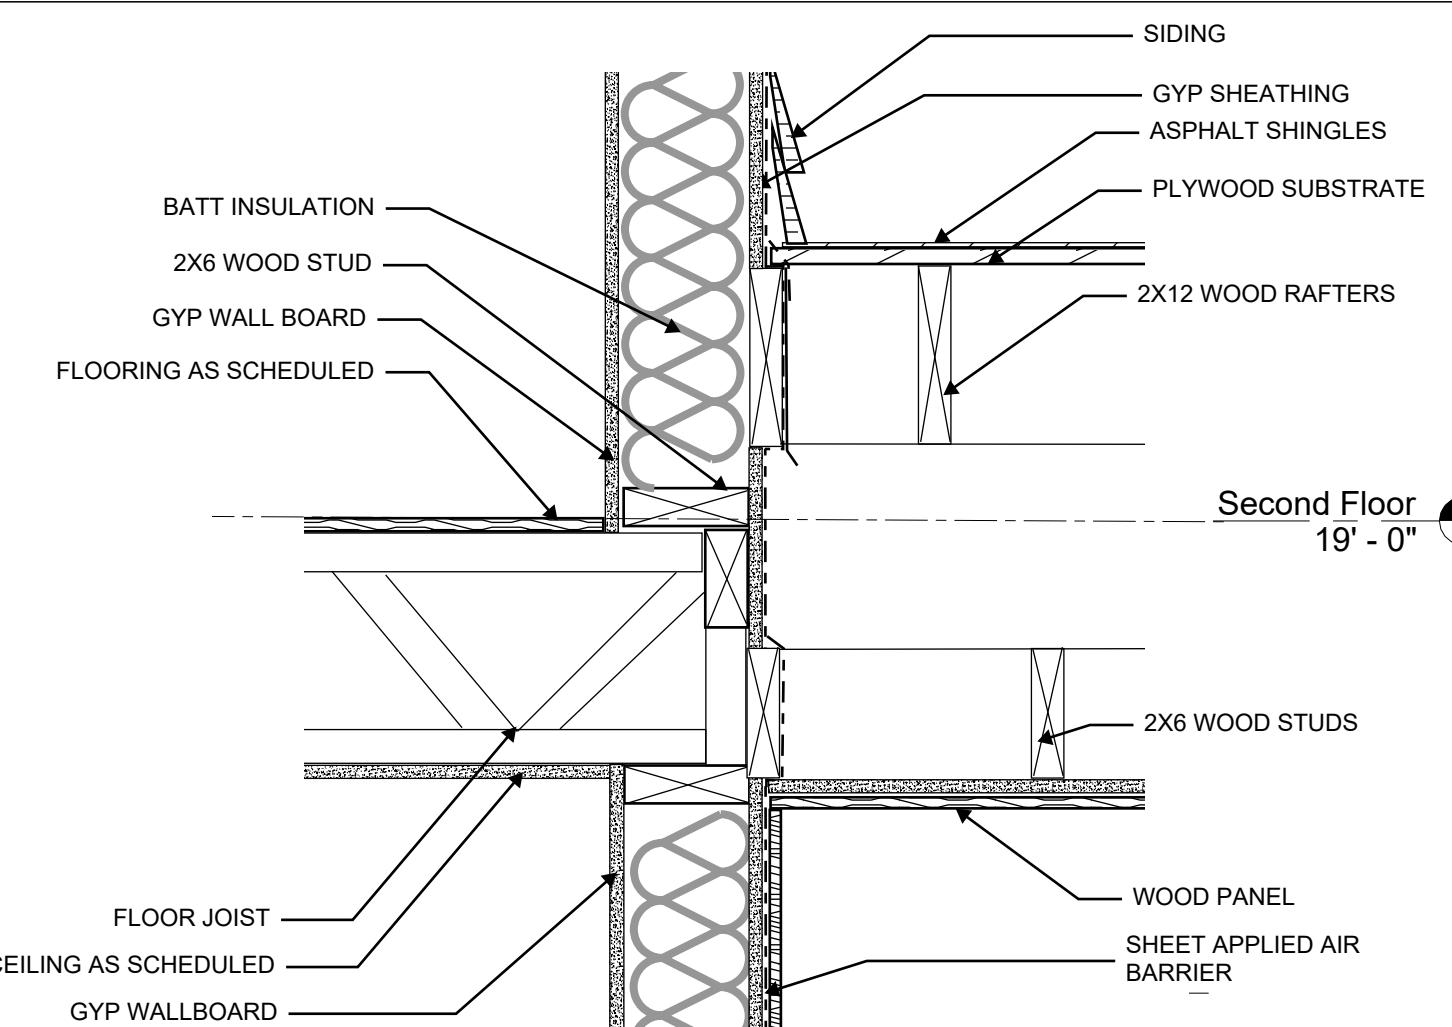


⑨ SECTION DETAIL - PORTICO ROOF CONNECTION
1 1/2" = 1'-0"

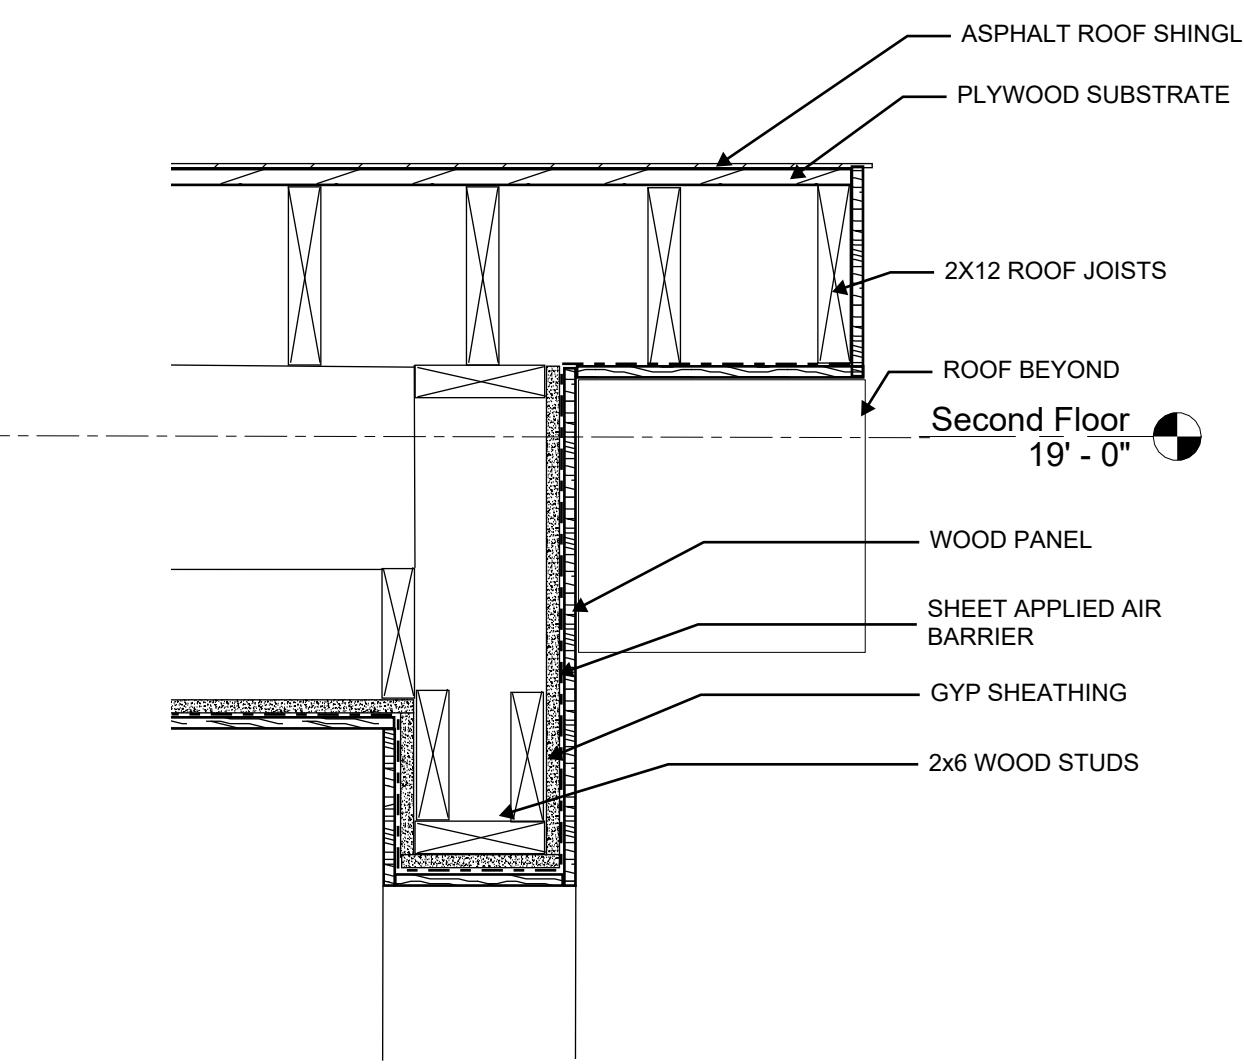


⑥ SECTION DETAIL - PORTICO ROOF
1 1/2" = 1'-0"

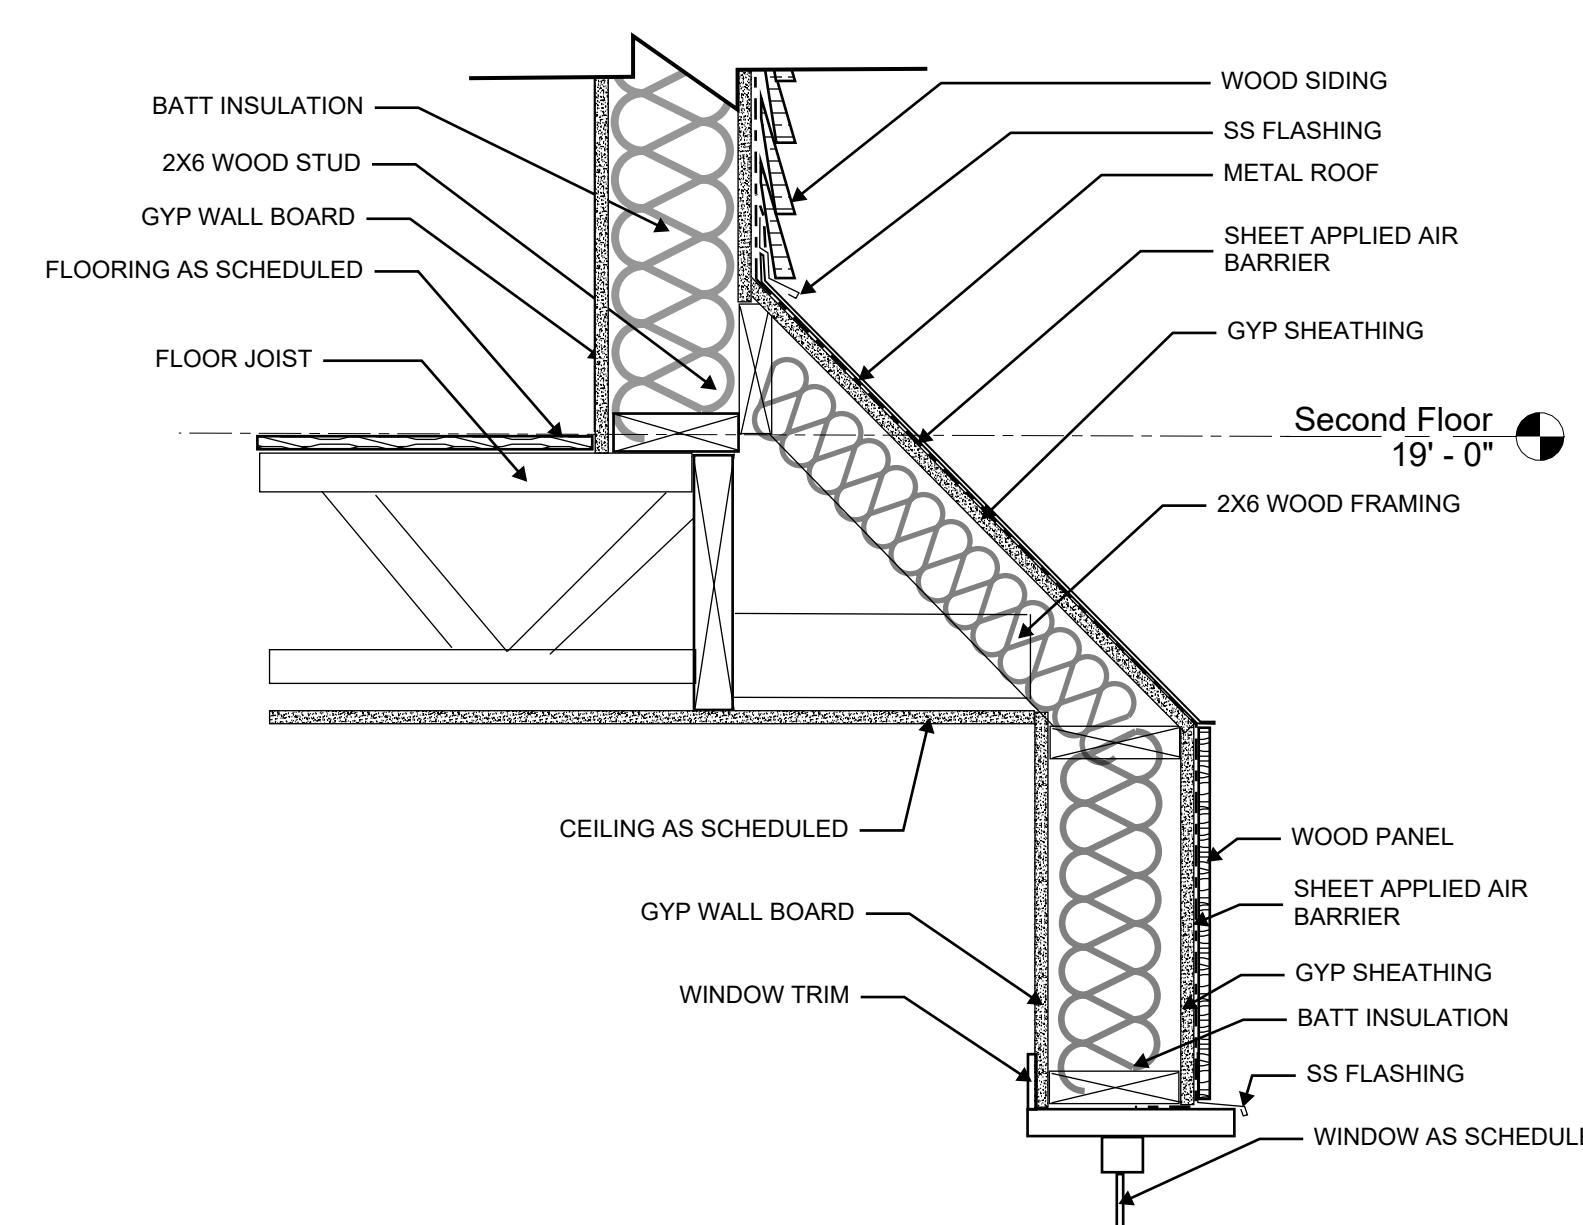


③ SECTION DETAIL - BAY WINDOW HEADER AND ROOF
1 1/2" = 1'-0"

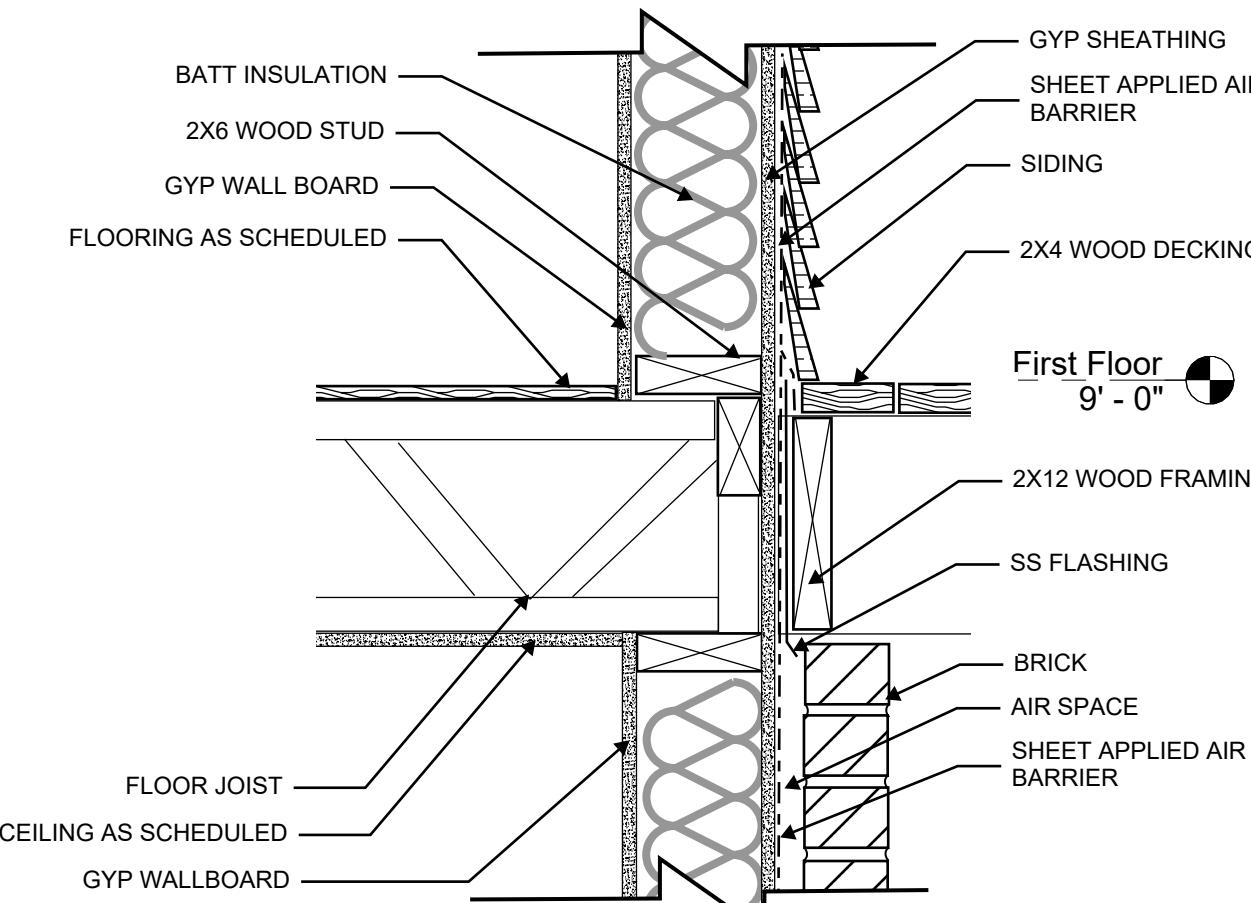


⑧ SECTION DETAIL - PORTICO FLOOR
1 1/2" = 1'-0"

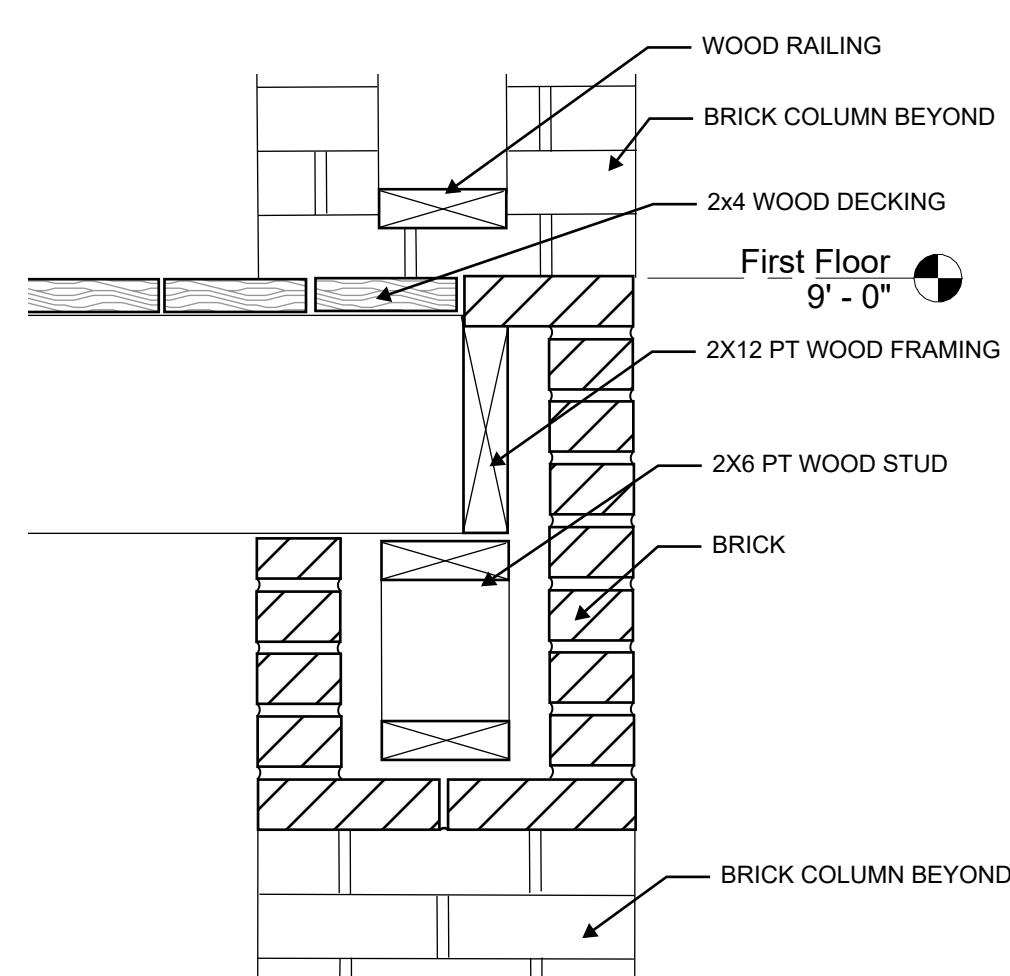


⑤ SECTION DETAIL - BRICK ARCH
1 1/2" = 1'-0"

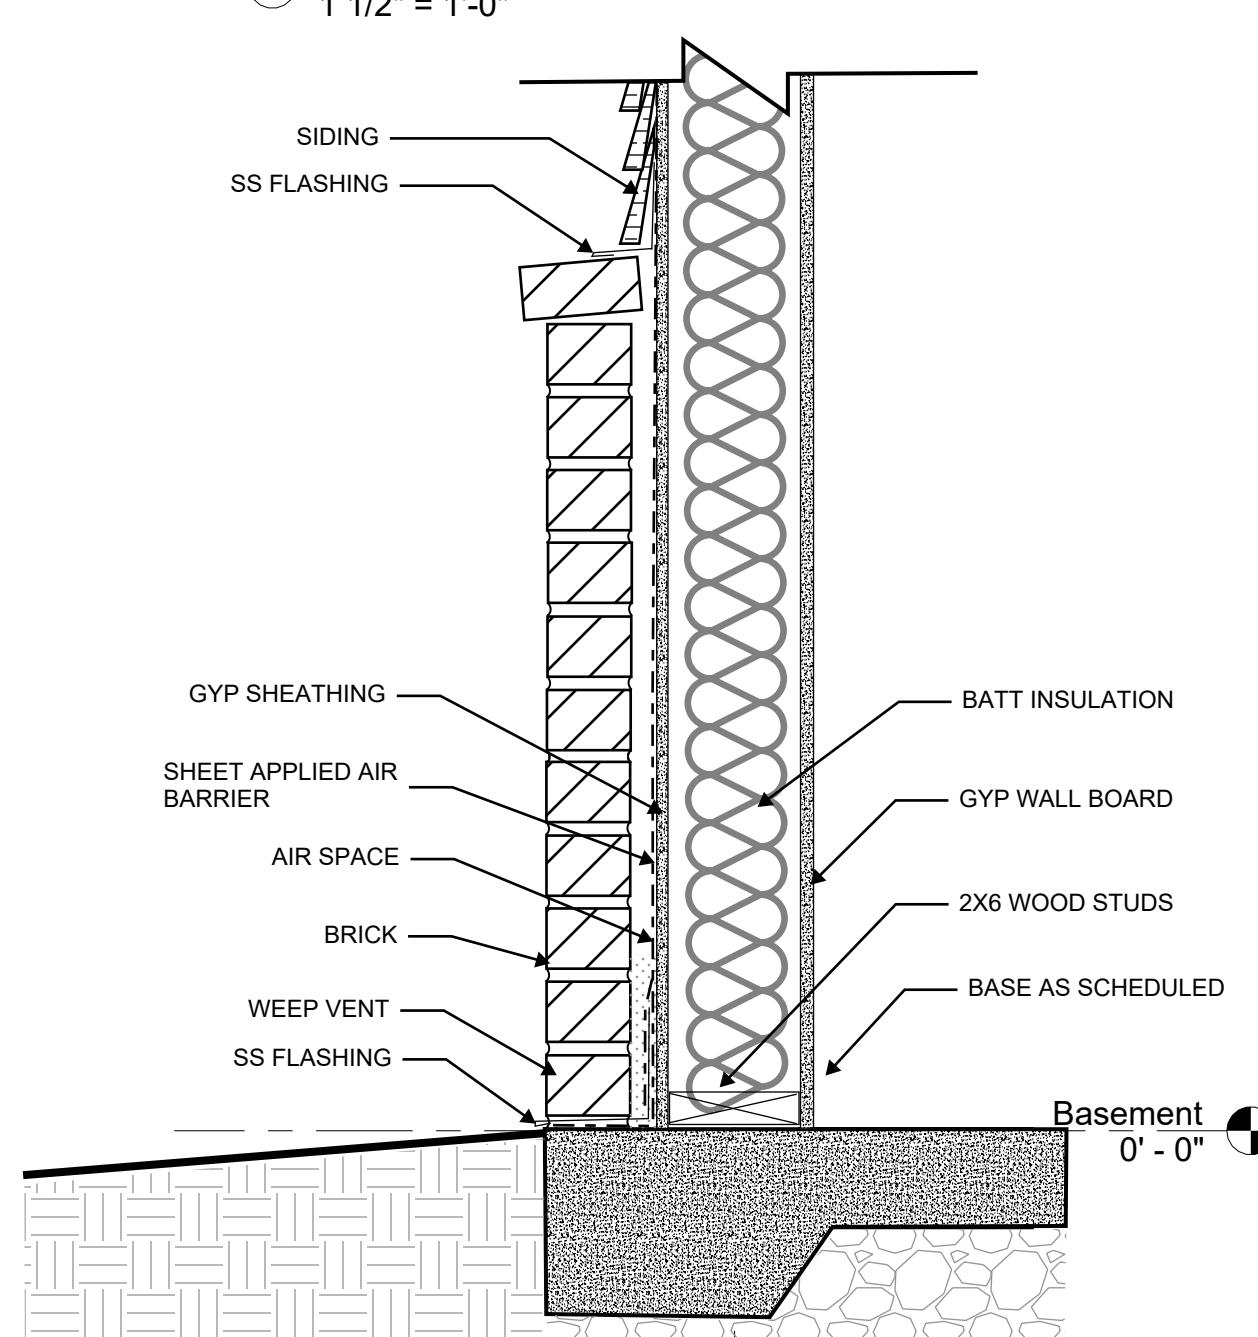


⑦ SECTION DETAIL - BRICK TO SIDING
1 1/2" = 1'-0"

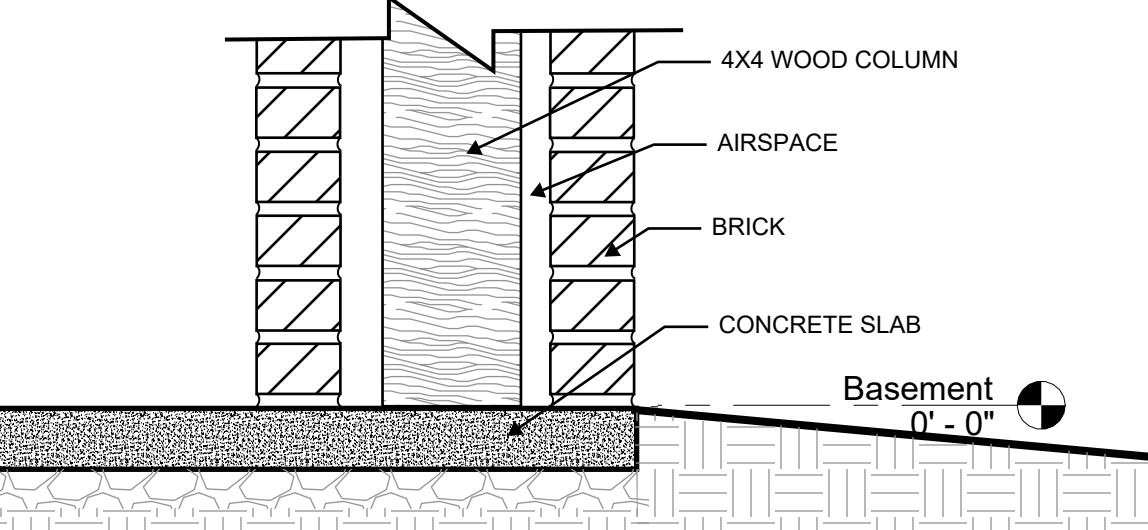

④ SECTION DETAIL - BRICK COLUMN AT GROUND
1 1/2" = 1'-0"

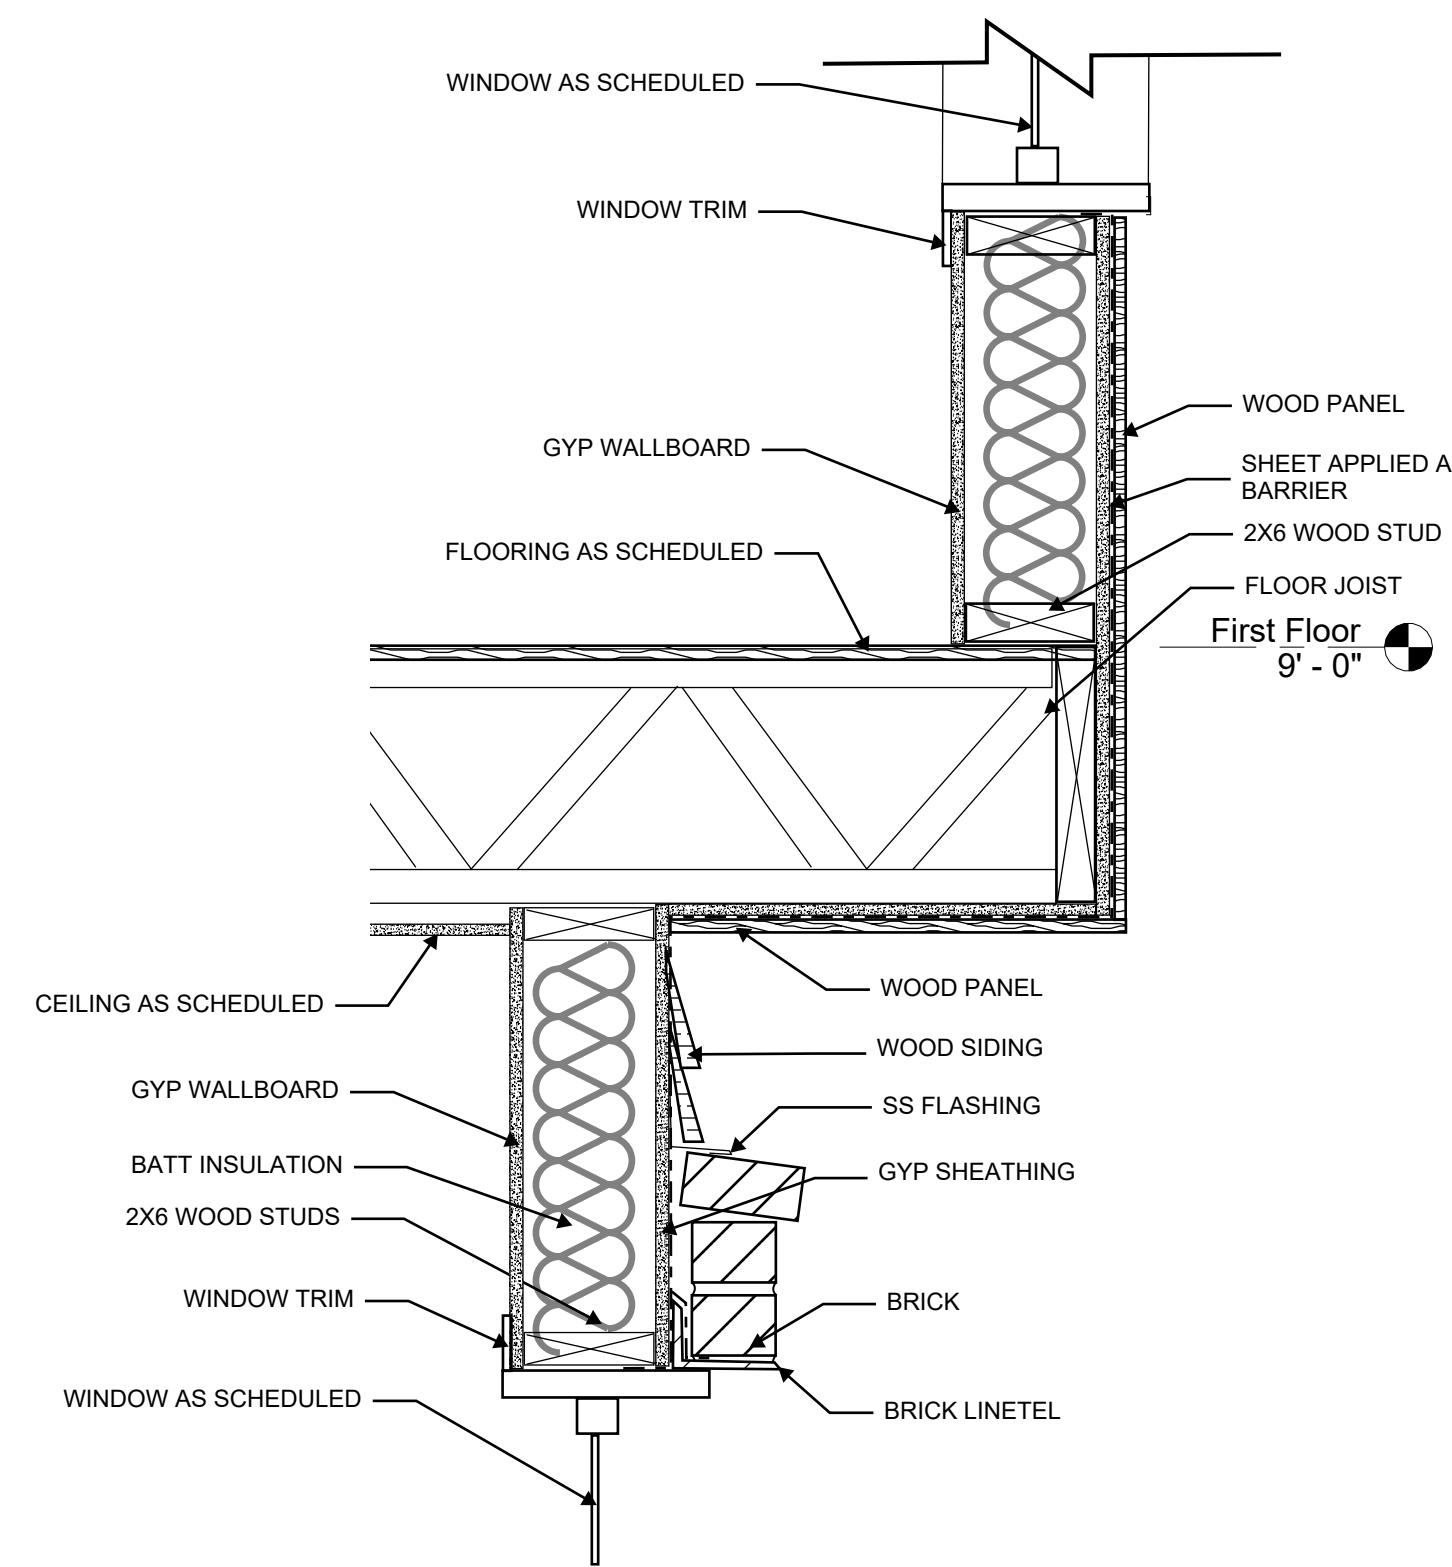

② SECTION DETAIL - WINDOW HEAD TO OVERHANG
1 1/2" = 1'-0"

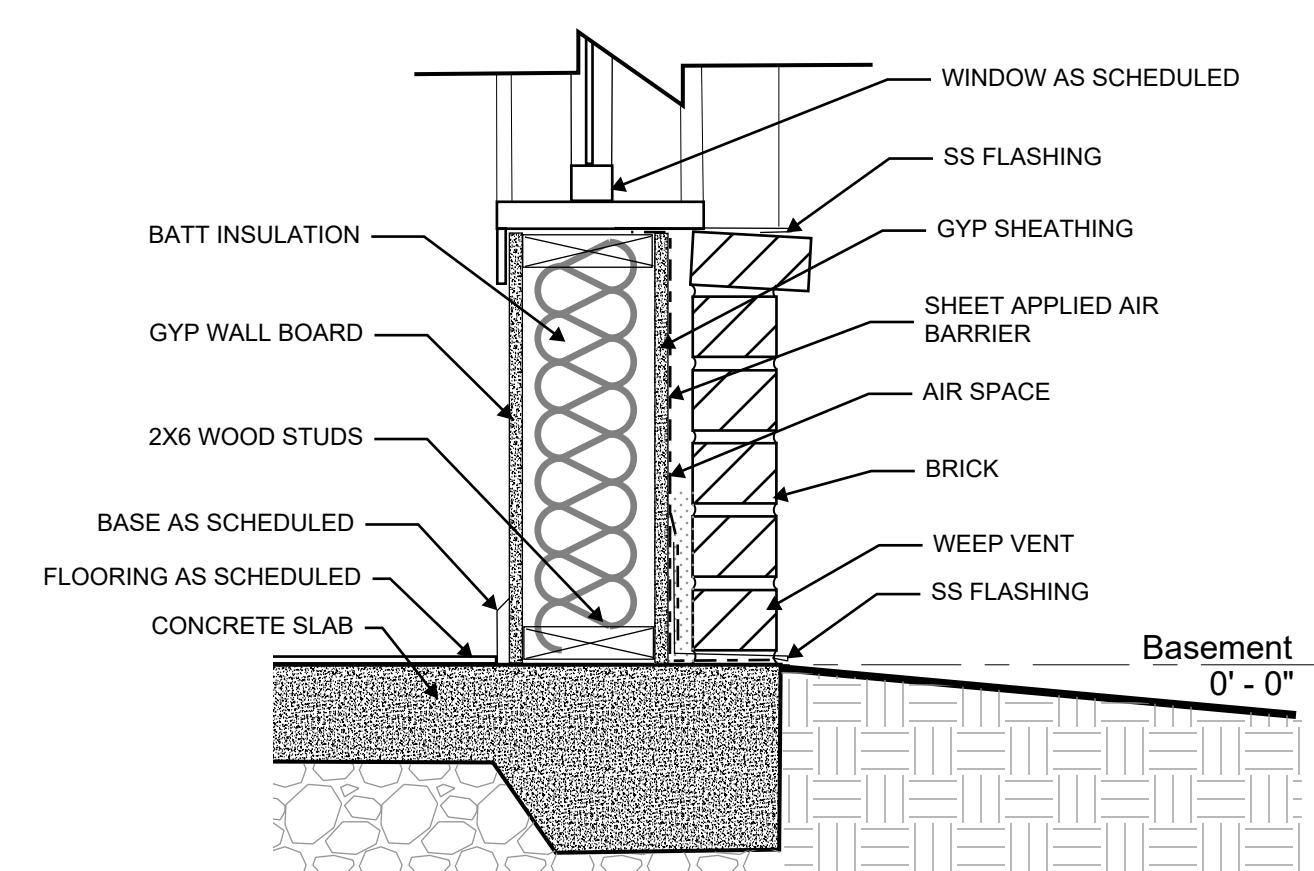

① SECTION DETAIL - WINDOW SILL BRICK
1 1/2" = 1'-0"

SINGLE FAMILY HOUSE 4 BEDROOM 3.5 BATH

CIOFFI FAMILY
404 PEACHTREE CIRCLE
ATLANTA, GA 30318

Project number 2023.001
Issue Date 09.06.23


CONSTRUCTION DOCUMENTS

Revisions
No. Description Date


SECTION DETAILS

A600


Architect: Will Cioffi, AIA
770 Peachtree St NW
Atlanta, GA 30308
hey@willcioffi.com

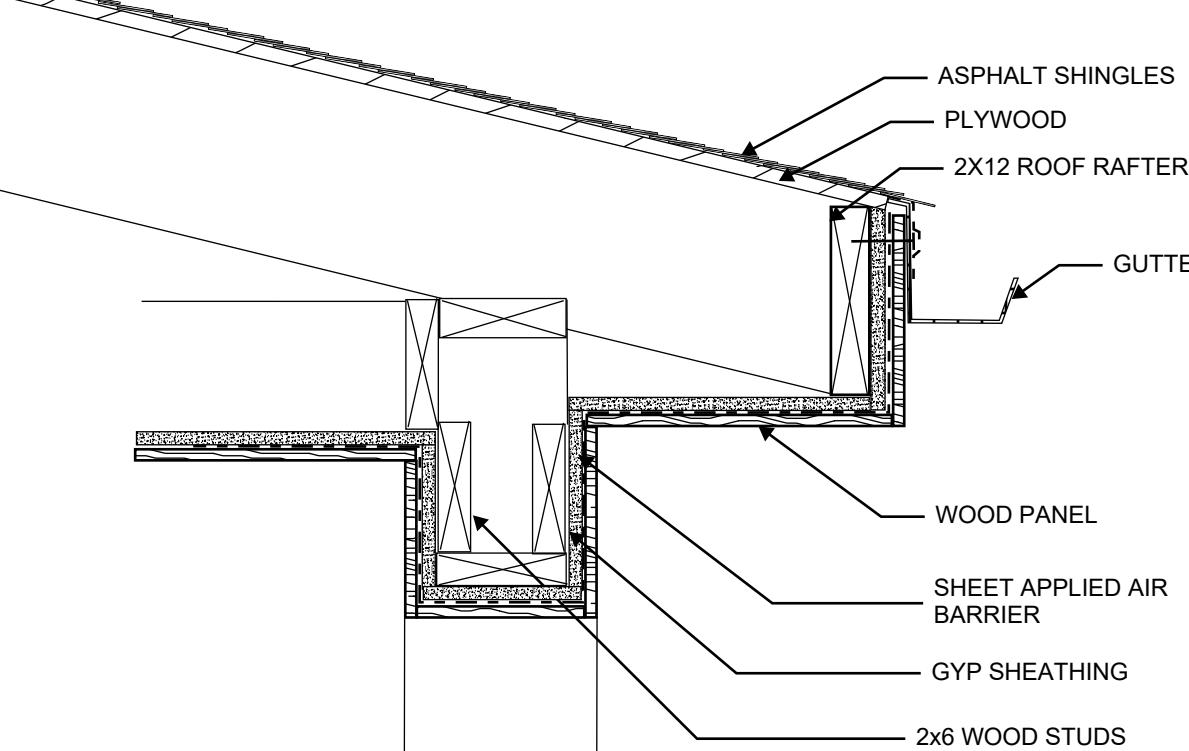

SECTION DETAIL - PORTICO ROOF GUTTER
⑨ 1 1/2" = 1'-0"

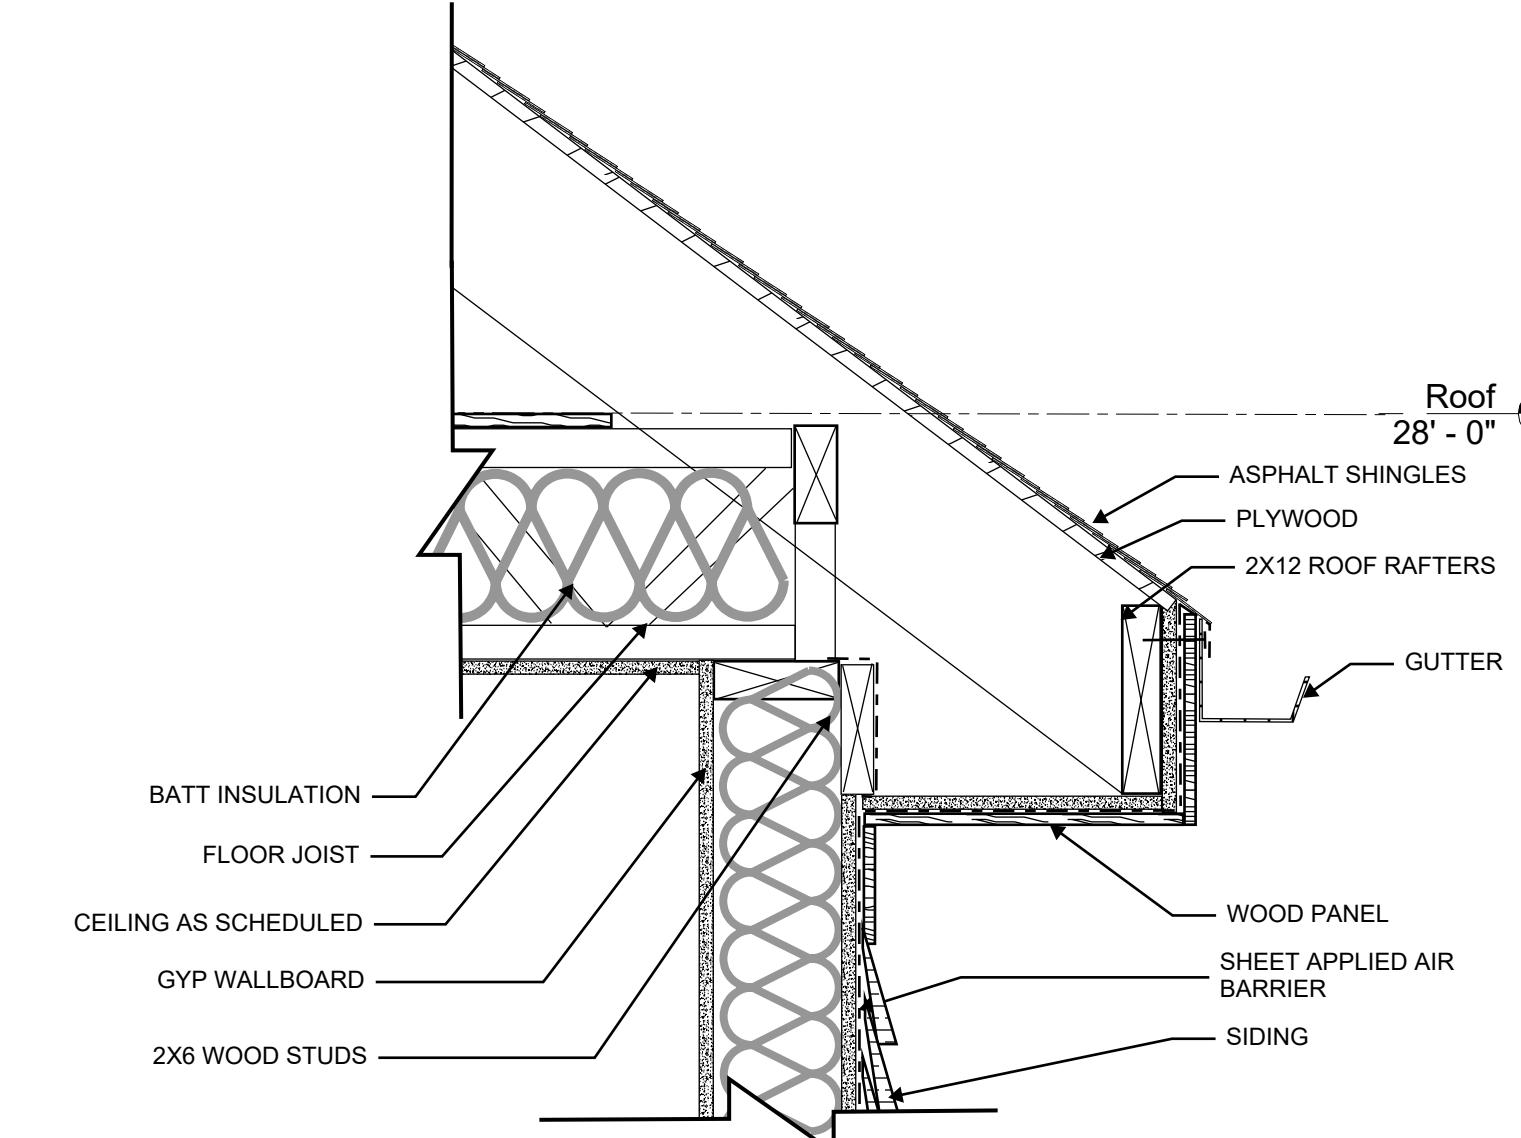


⑥ SECTION DETAIL - ROOF GUTTER
1 1/2" = 1'-0"

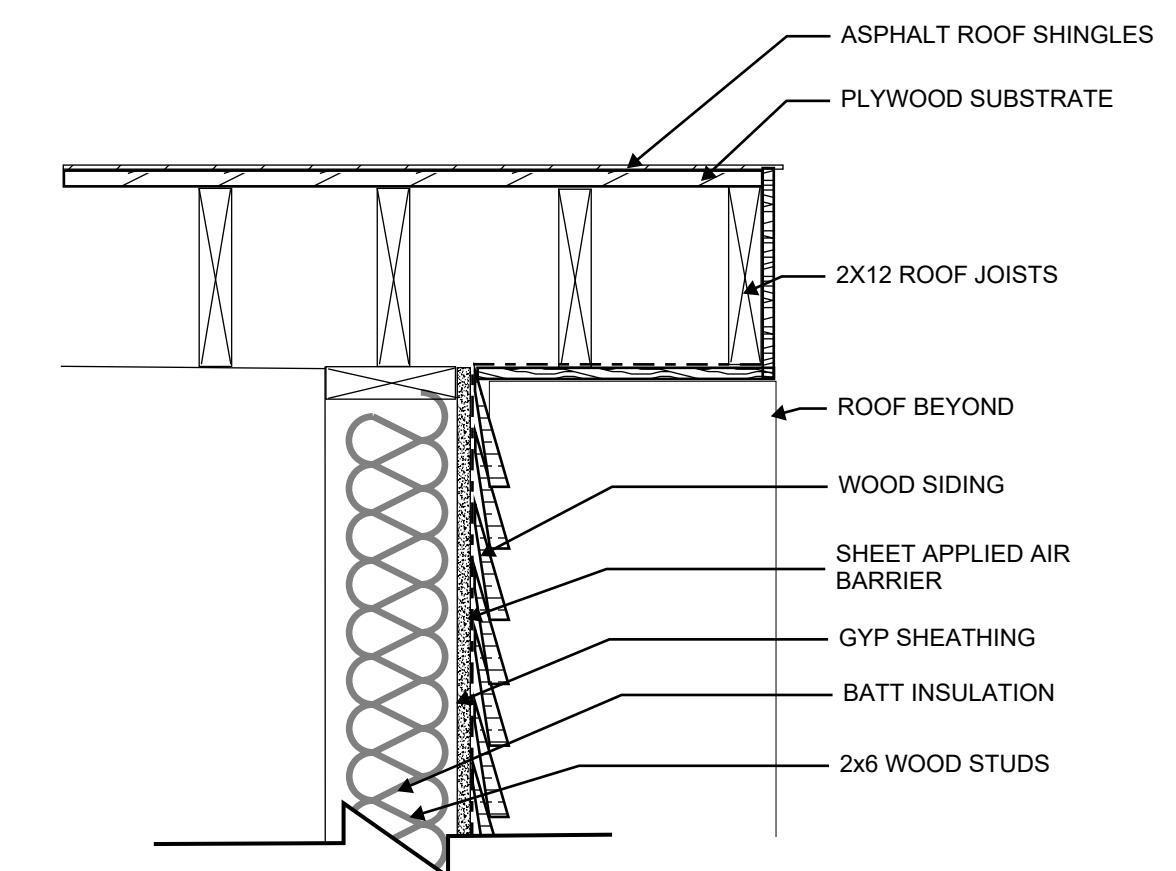


③ SECTION DETAIL - ROOF
1 1/2" = 1'-0"




SECTION DETAIL - WINDOW HEAD SIDING
⑧ 1 1/2" = 1'-0"

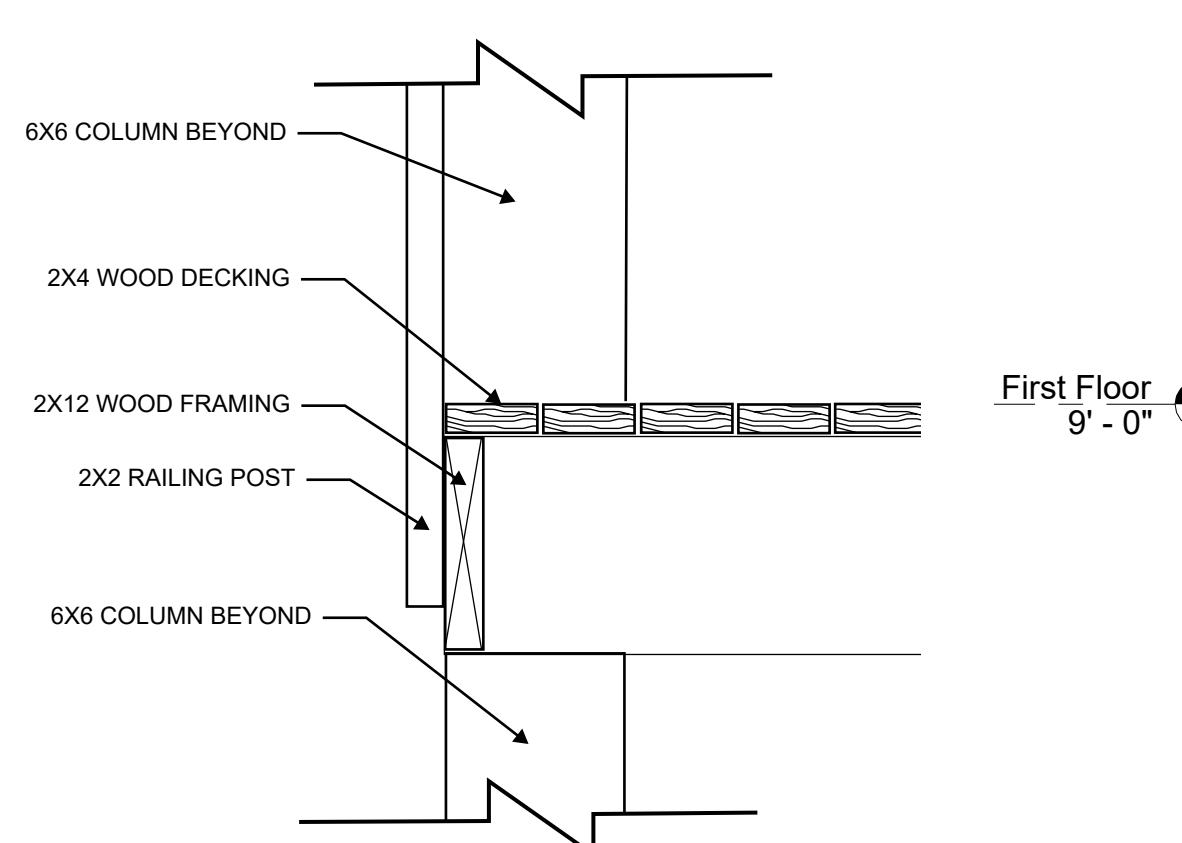


⑤ SECTION DETAIL - DECK EDGE
1 1/2" = 1'-0"

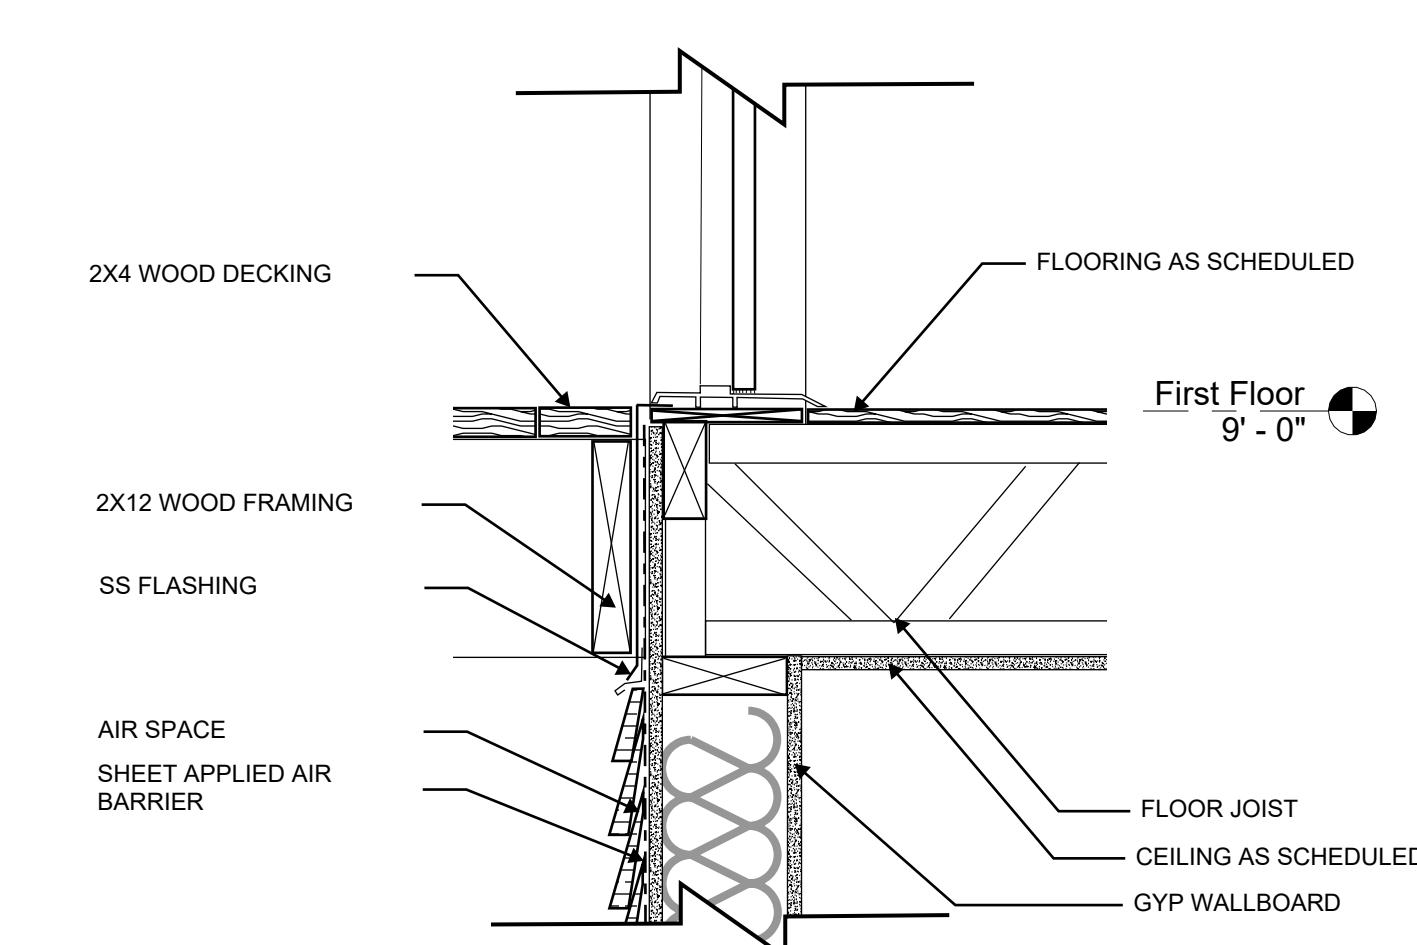

② SECTION DETAIL - DECK CONNECTION
1 1/2" = 1'-0"

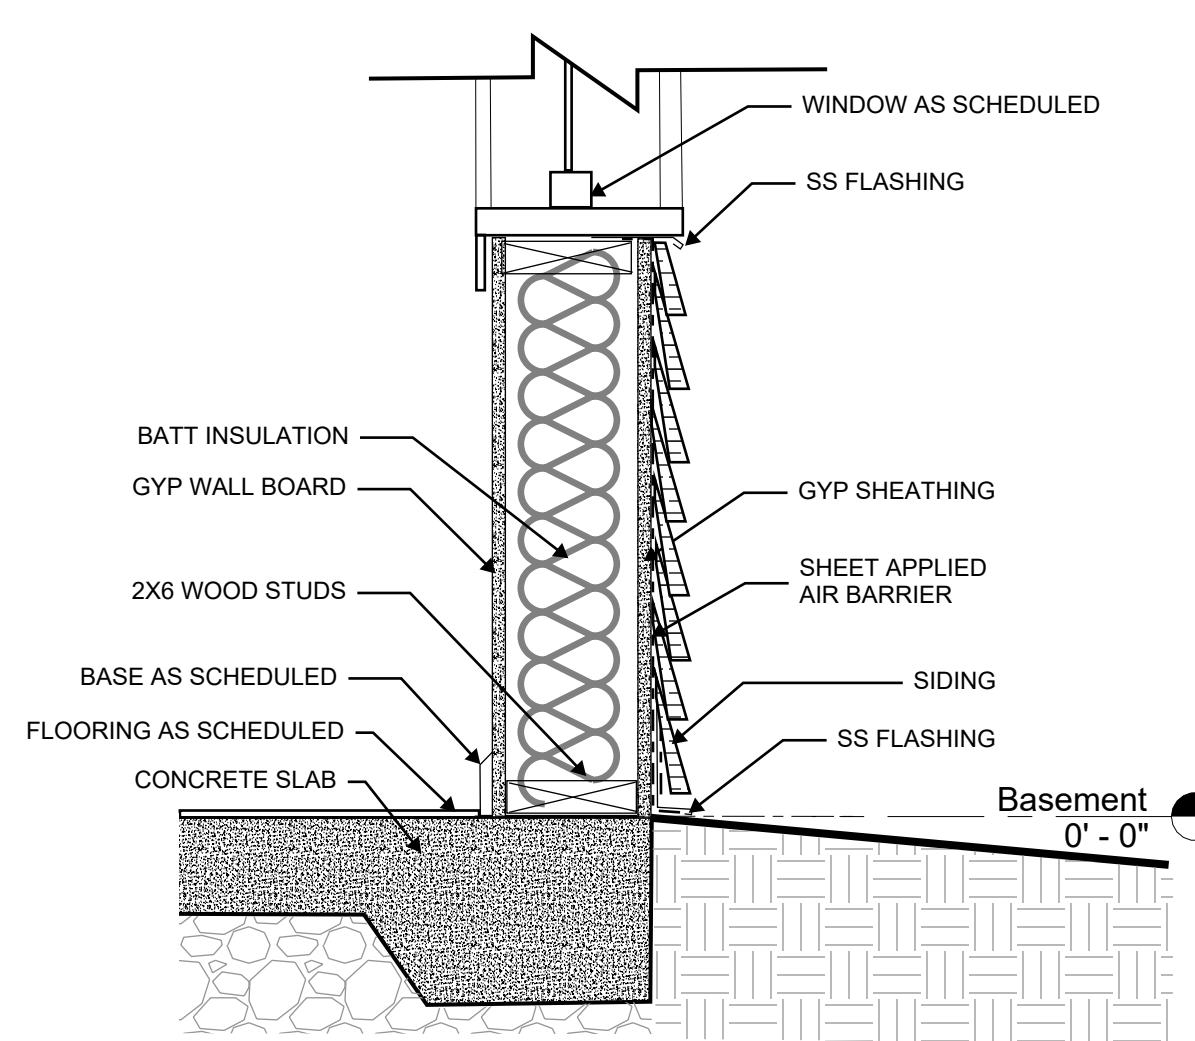

SECTION DETAIL - WINDOW SILL AT SIDING
⑦ 1 1/2" = 1'-0"

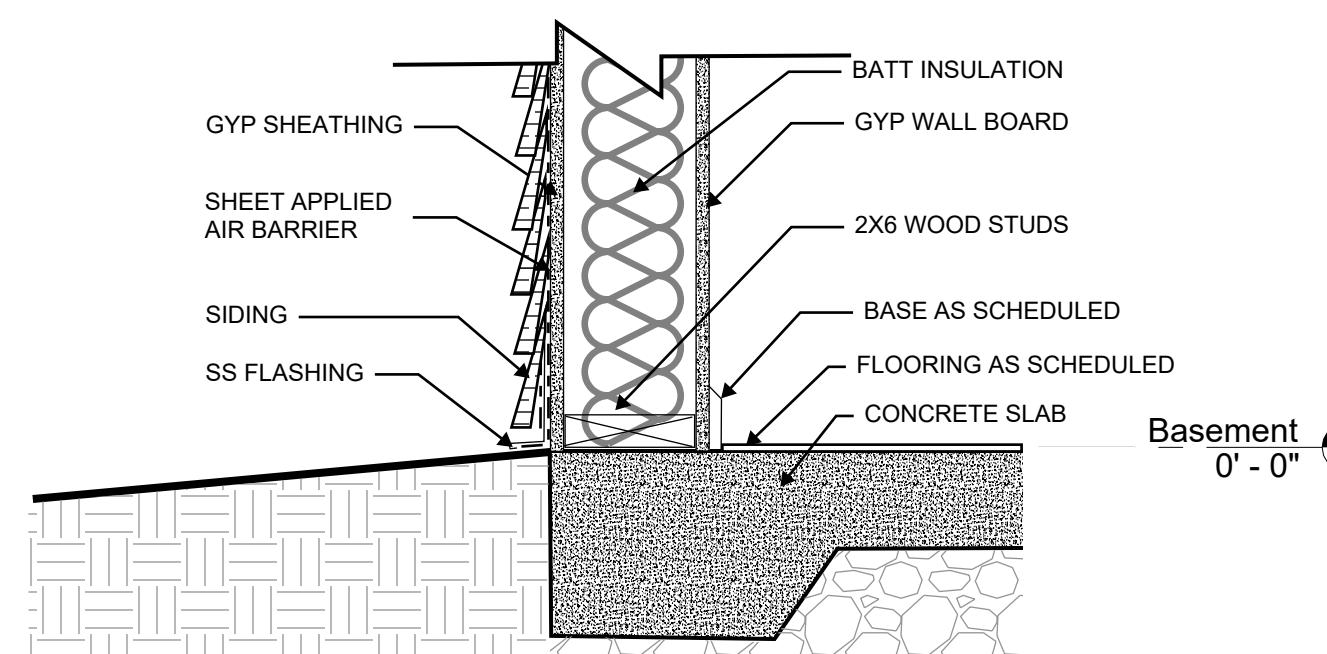

① SECTION DETAIL - SIDING AT GRADE
1 1/2" = 1'-0"

SINGLE FAMILY HOUSE 4 BEDROOM 3.5 BATH

CIOFFI FAMILY
404 PEACHTREE CIRCLE
ATLANTA, GA 30318


Project number 2023.001
Issue Date 09.06.23

CONSTRUCTION DOCUMENTS


Revisions
No. Description Date

SECTION DETAILS


A601

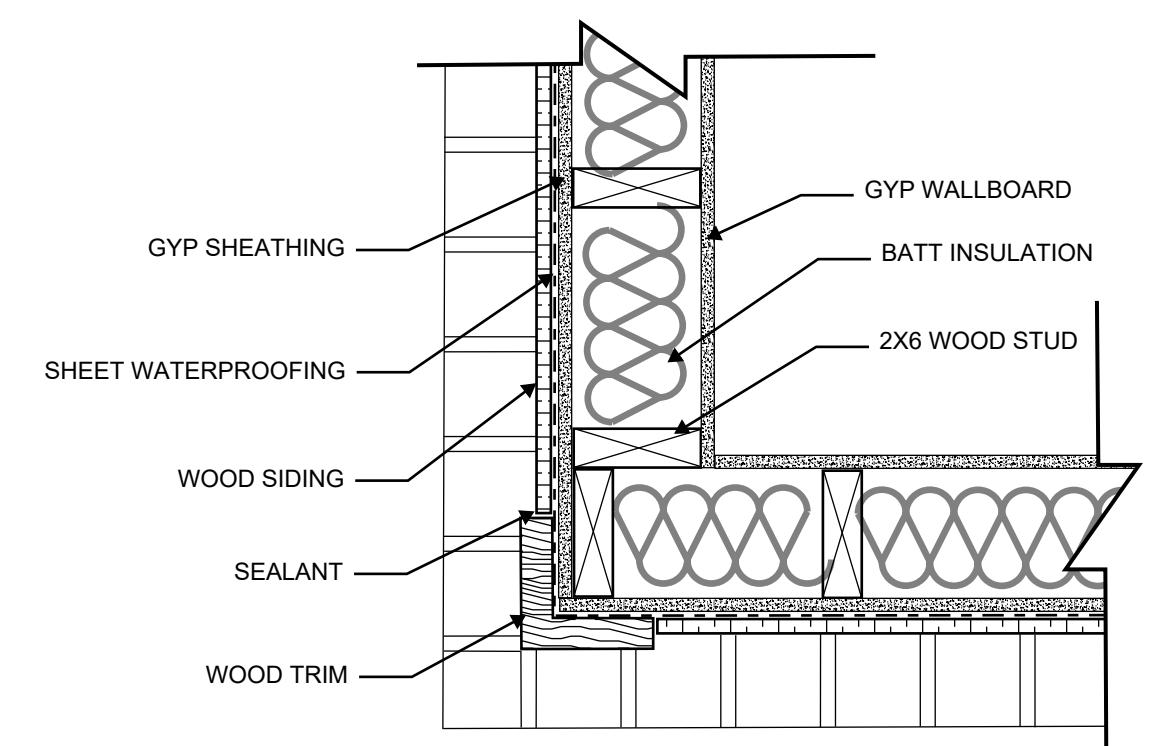


④ PLAN DETAIL - SIDING CORNER
1 1/2" = 1'-0"

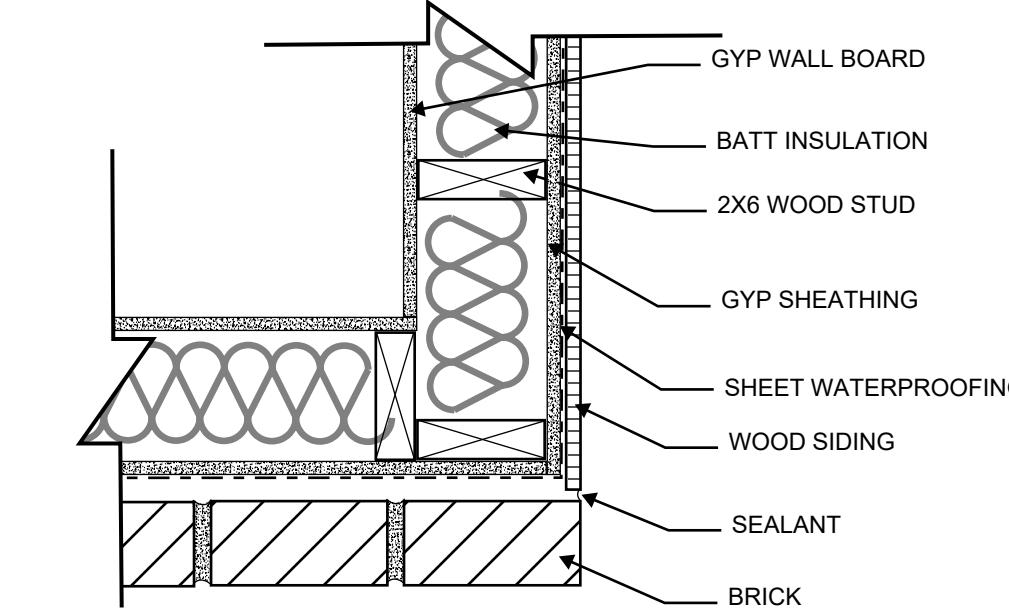

PLAN DETAIL - BRICK TO SIDING CORNER
1 1/2" = 1'-0"

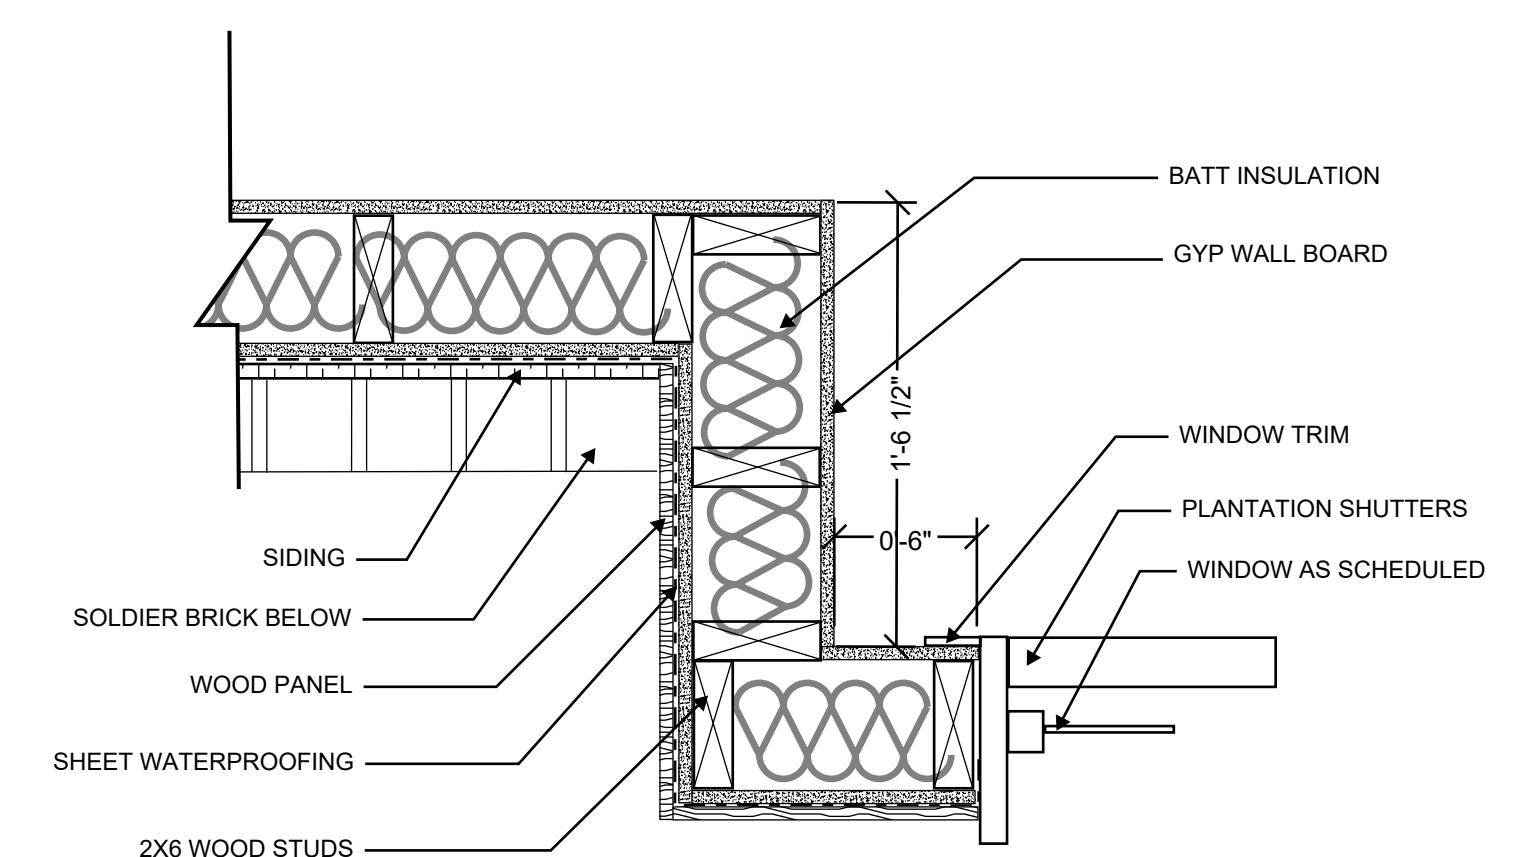

③ PLAN DETAIL - BAY WINDOW JAMB
1 1/2" = 1'-0"

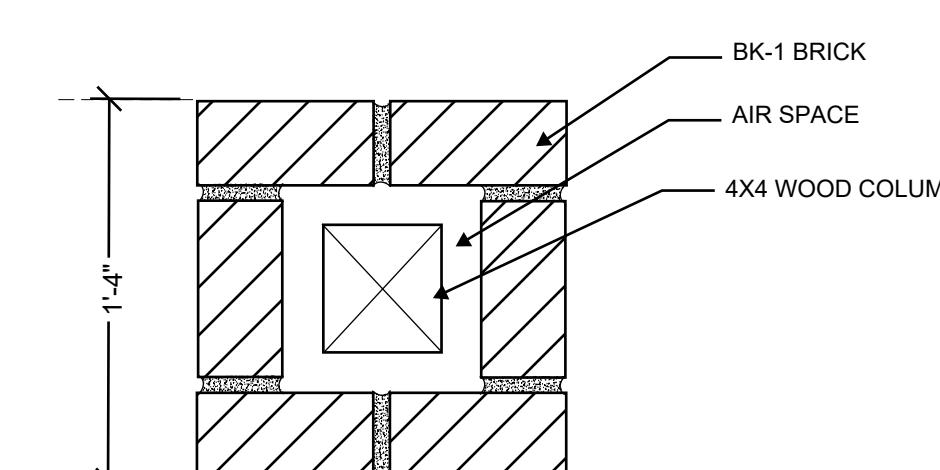

① PLAN DETAIL - BRICK COLUMN
1 1/2" = 1'-0"

NOT FOR CONSTRUCTION

SINGLE FAMILY HOUSE 4 BEDROOM 3.5 BATH

CIOFFI FAMILY

404 PEACHTREE CIRCLE
ATLANTA, GA 30318






Project number 2023.001
Issue Date 09.06.23

CONSTRUCTION DOCUMENTS

Revisions
No. Description Date

PLAN DETAILS

A620

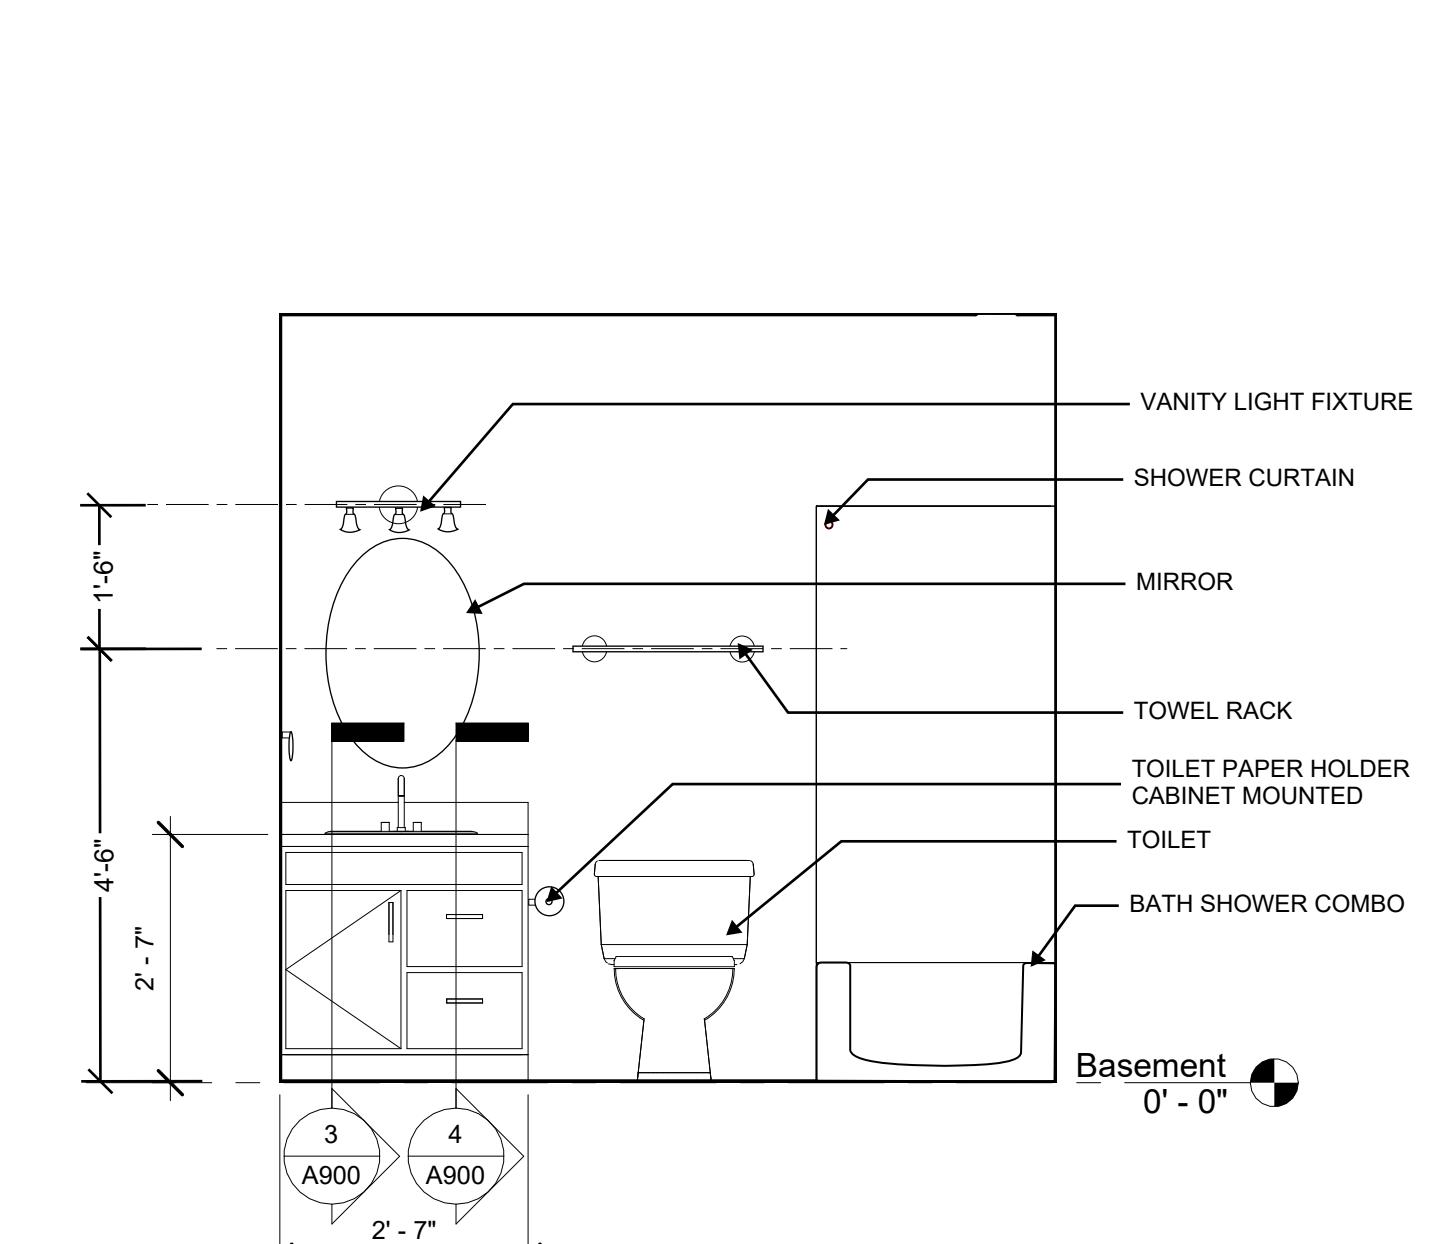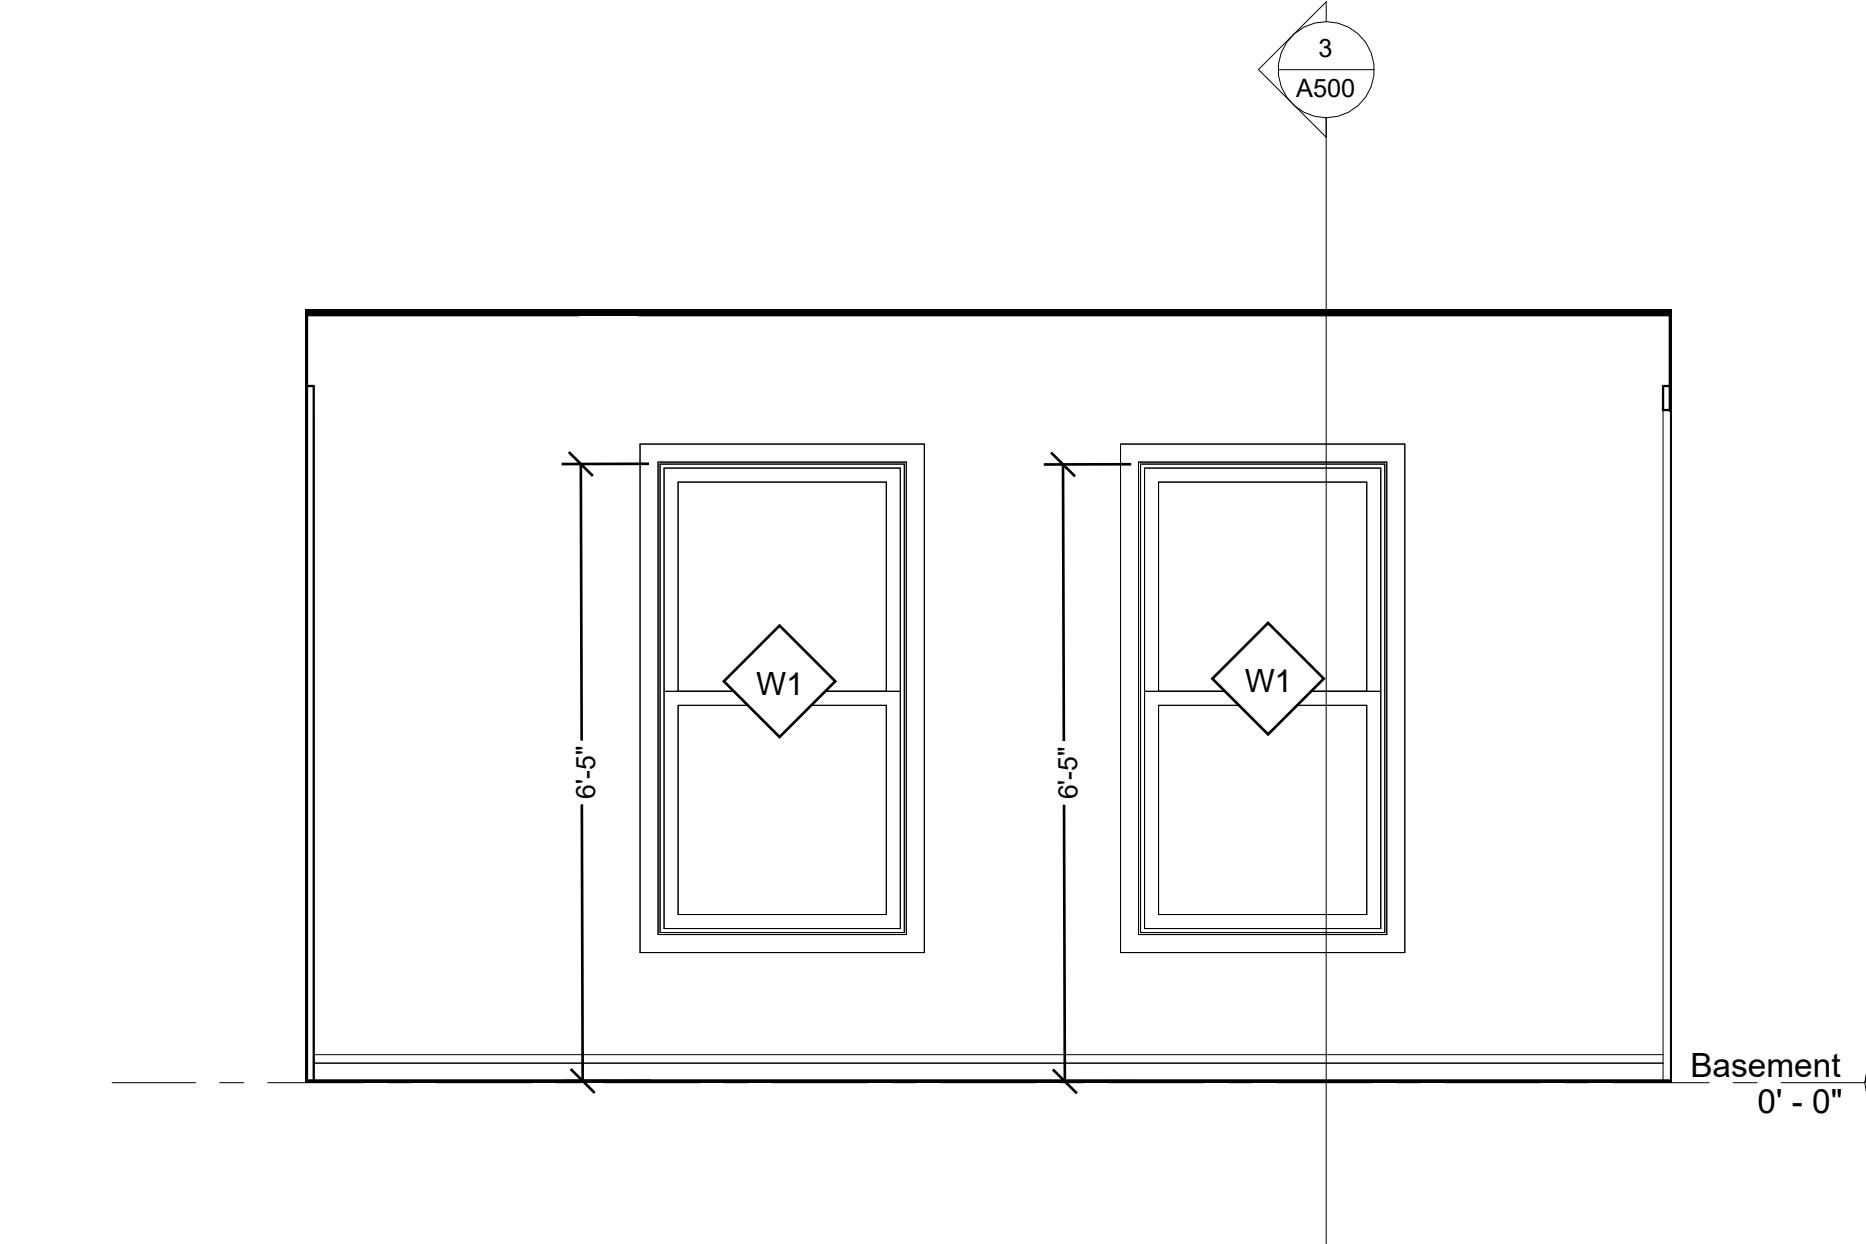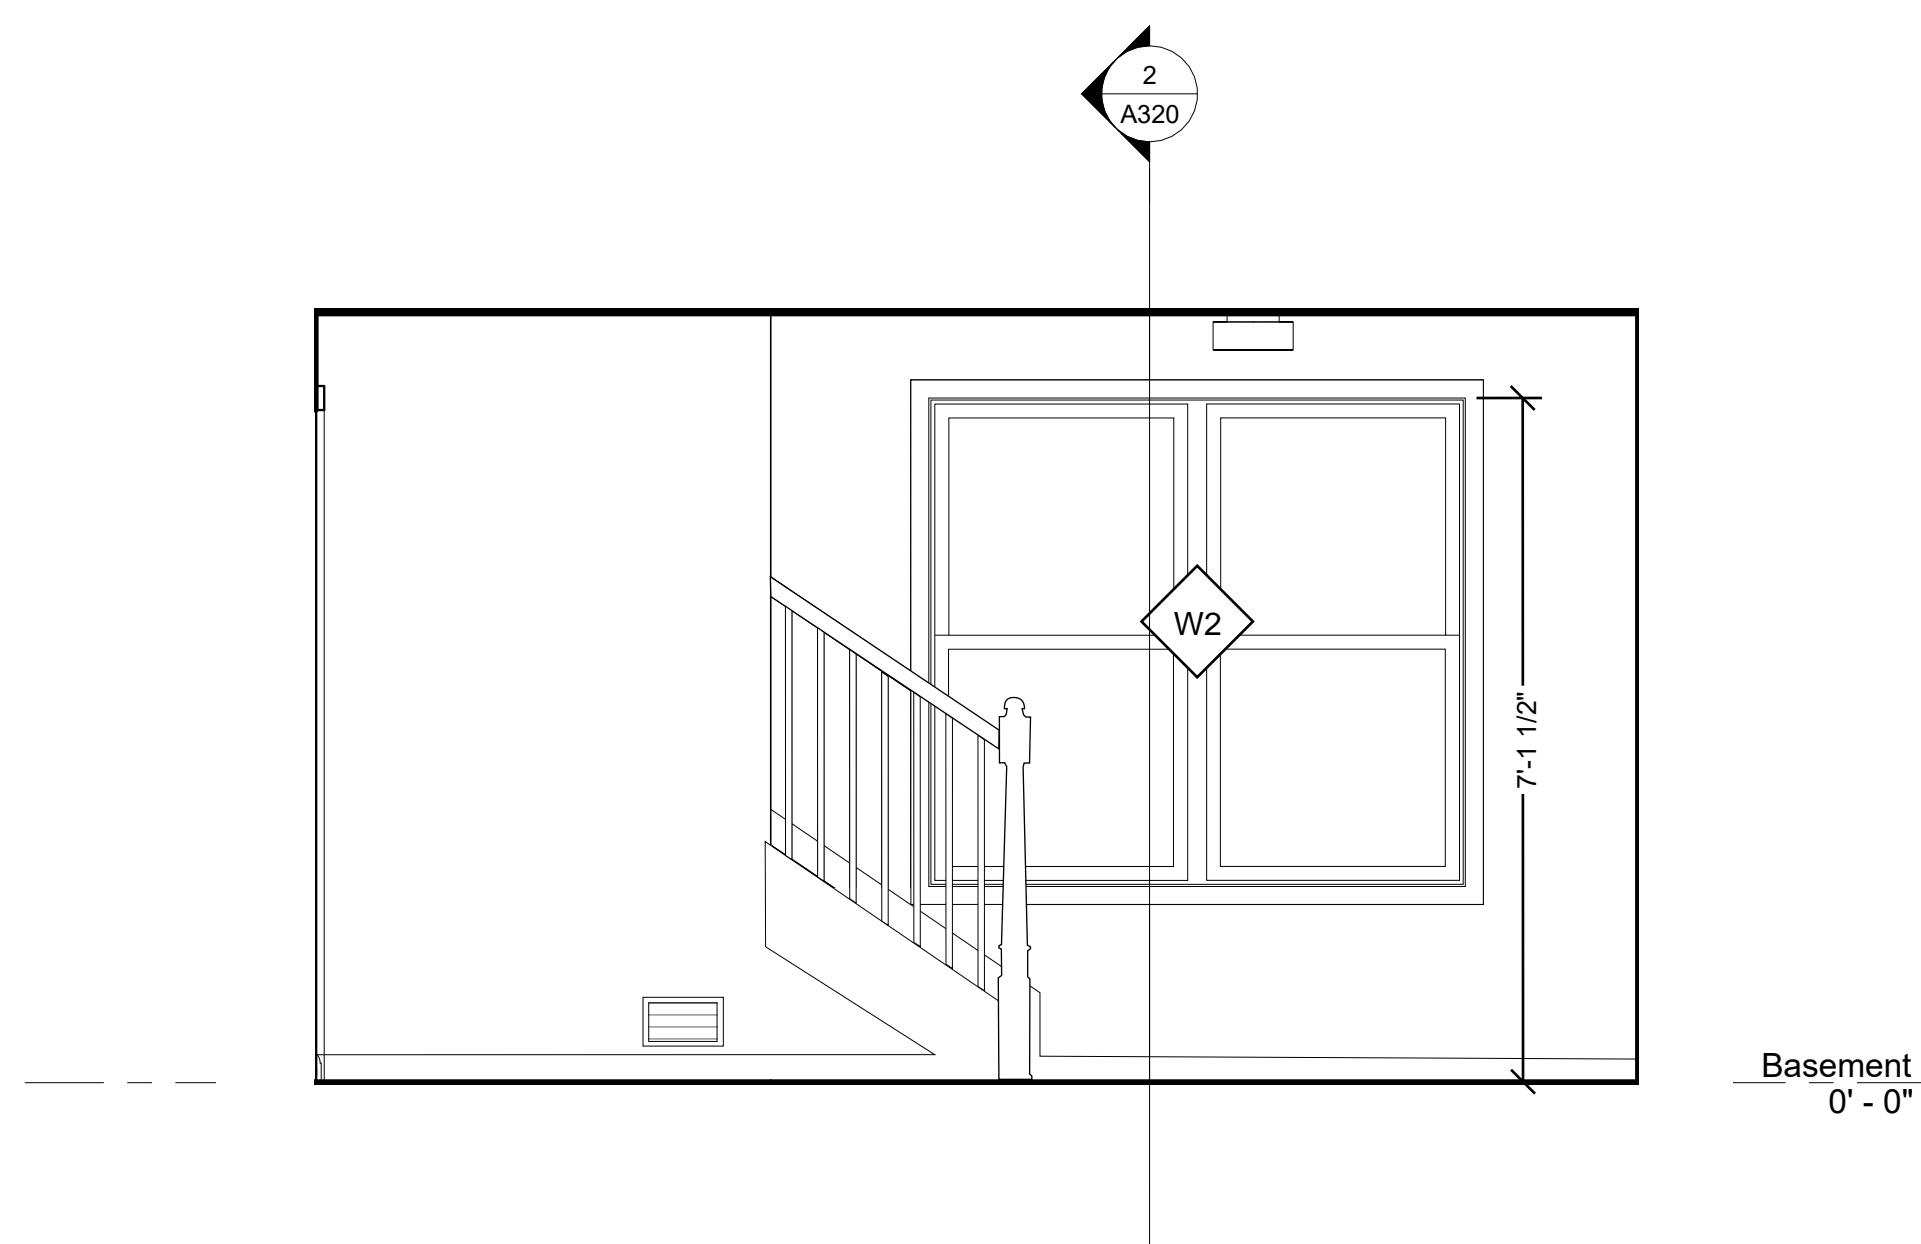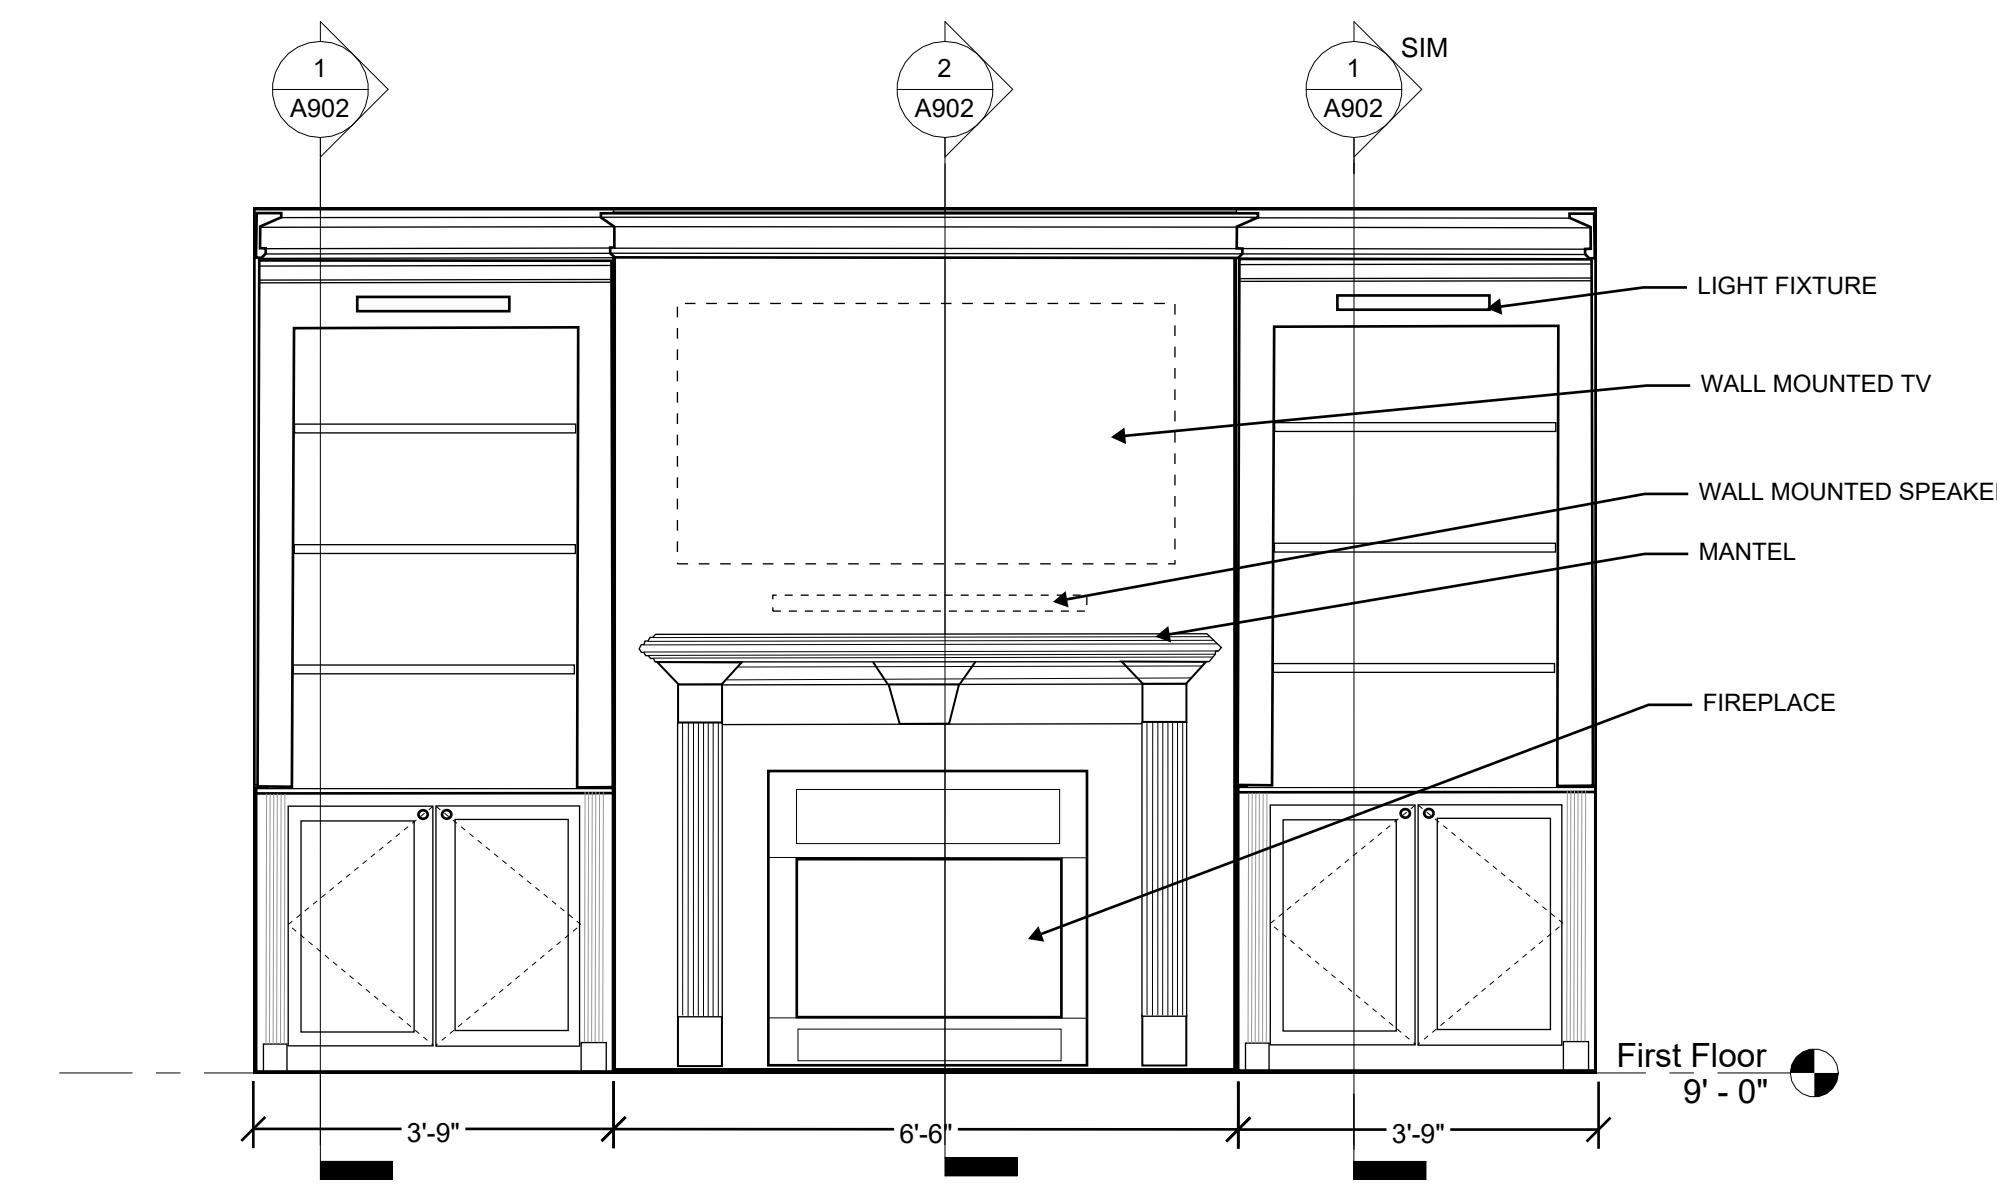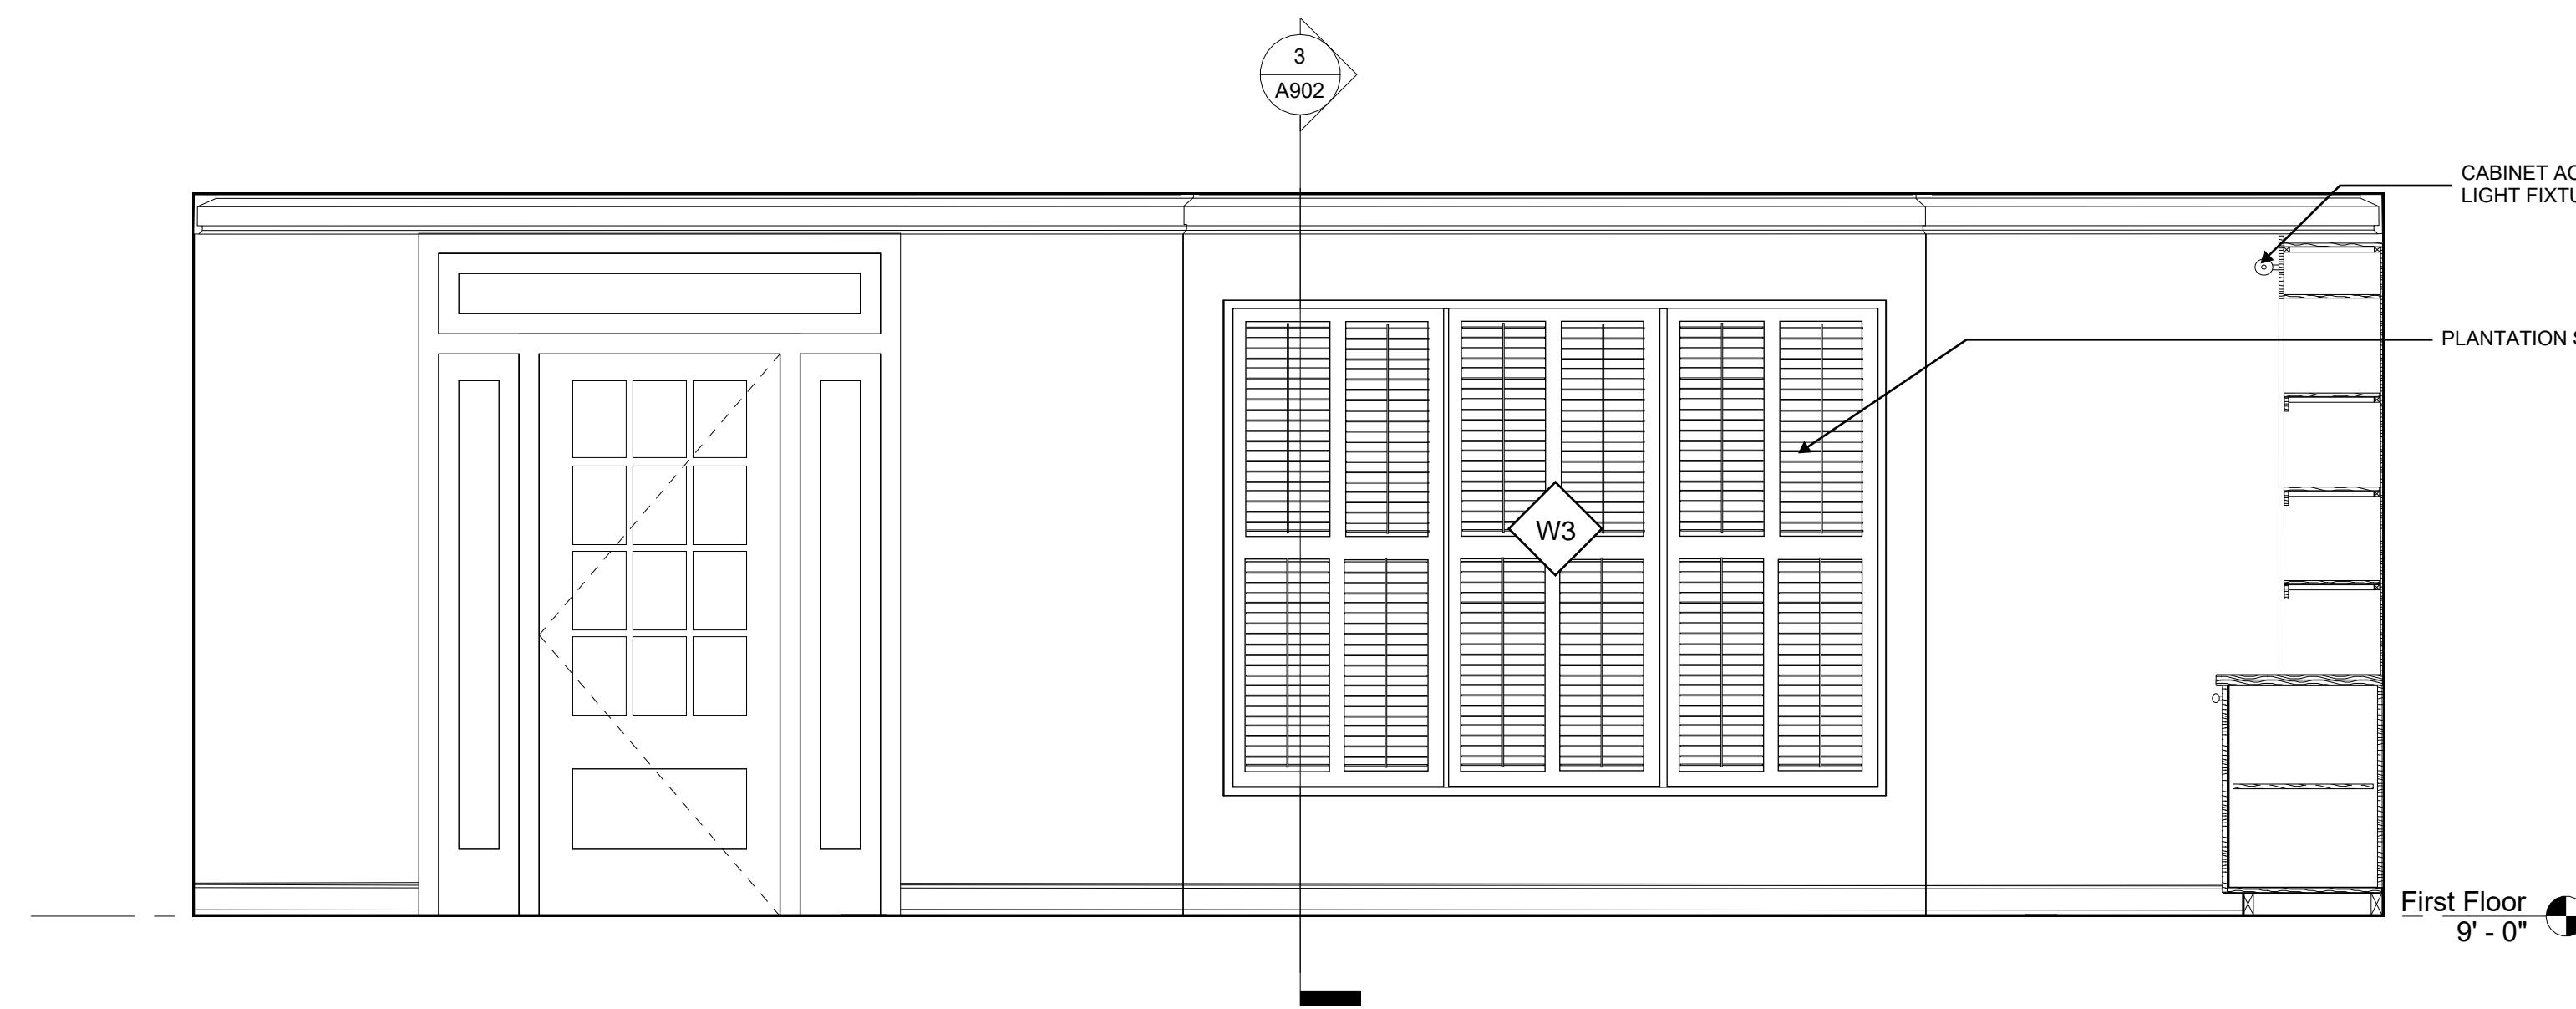

SINGLE FAMILY HOUSE 4 BEDROOM 3.5 BATH

CIOFFI FAMILY
404 PEACHTREE CIRCLE
ATLANTA, GA 30318

Project number 2023.001
Issue Date 09.06.23


CONSTRUCTION DOCUMENTS

Revisions
No. Description Date

INTERIOR ELEVATIONS

A700


Architect: Will Cioffi, AIA
770 Peachtree St NW
Atlanta, GA 30308
hey@willcioffi.com

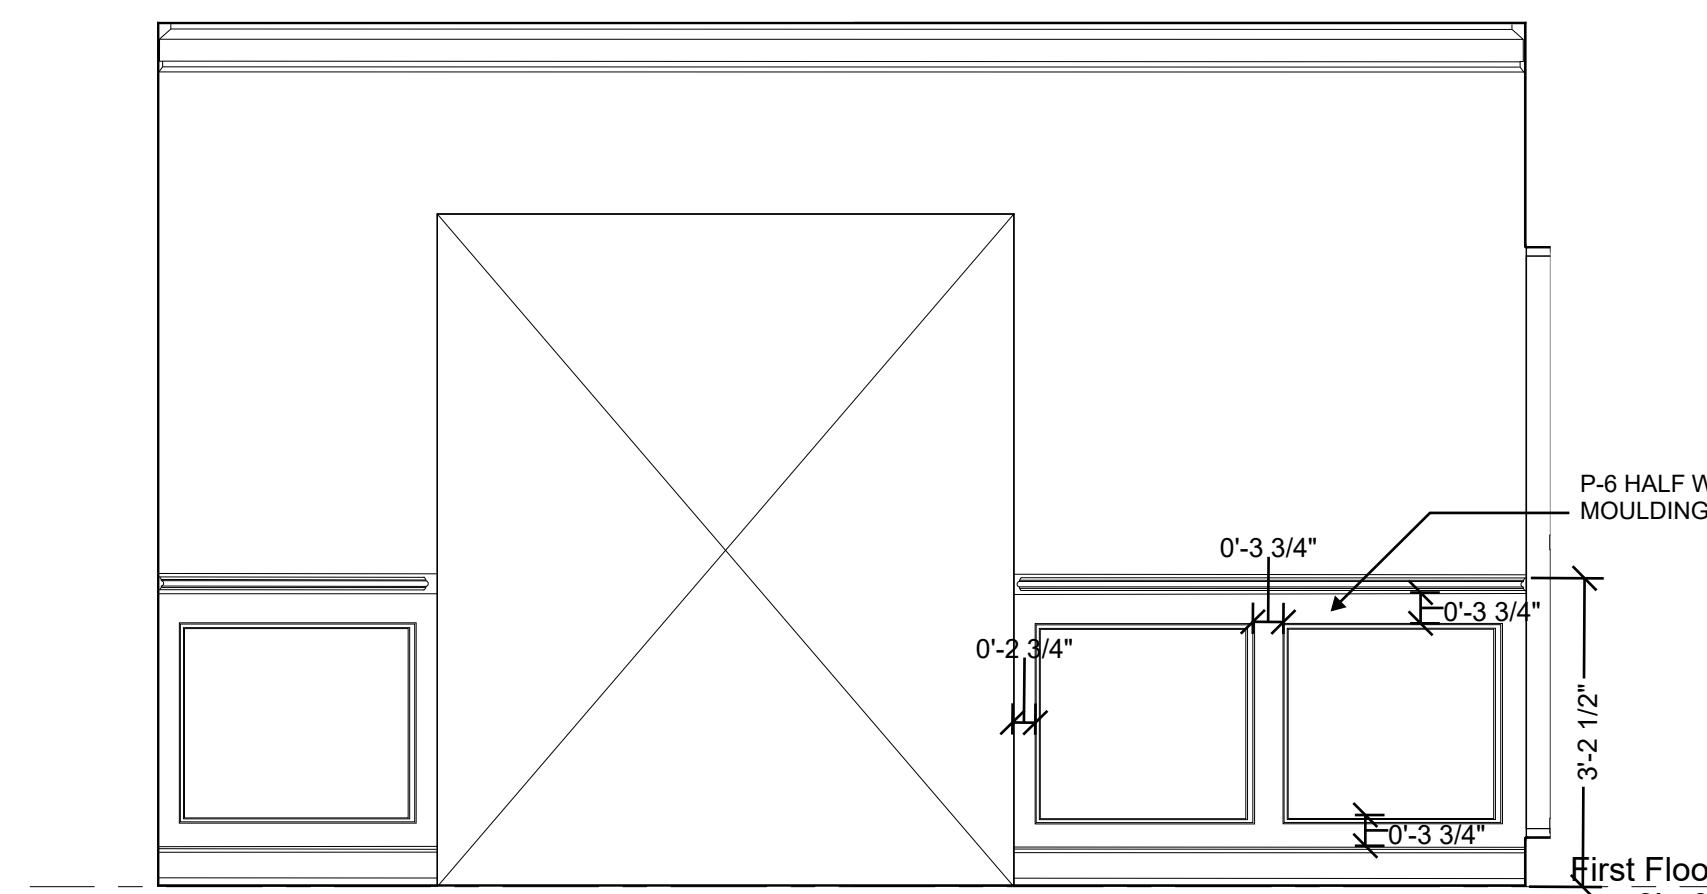

INTERIOR ELEVATION - DINING ROOM

SOUTH


1/2" = 1'-0"

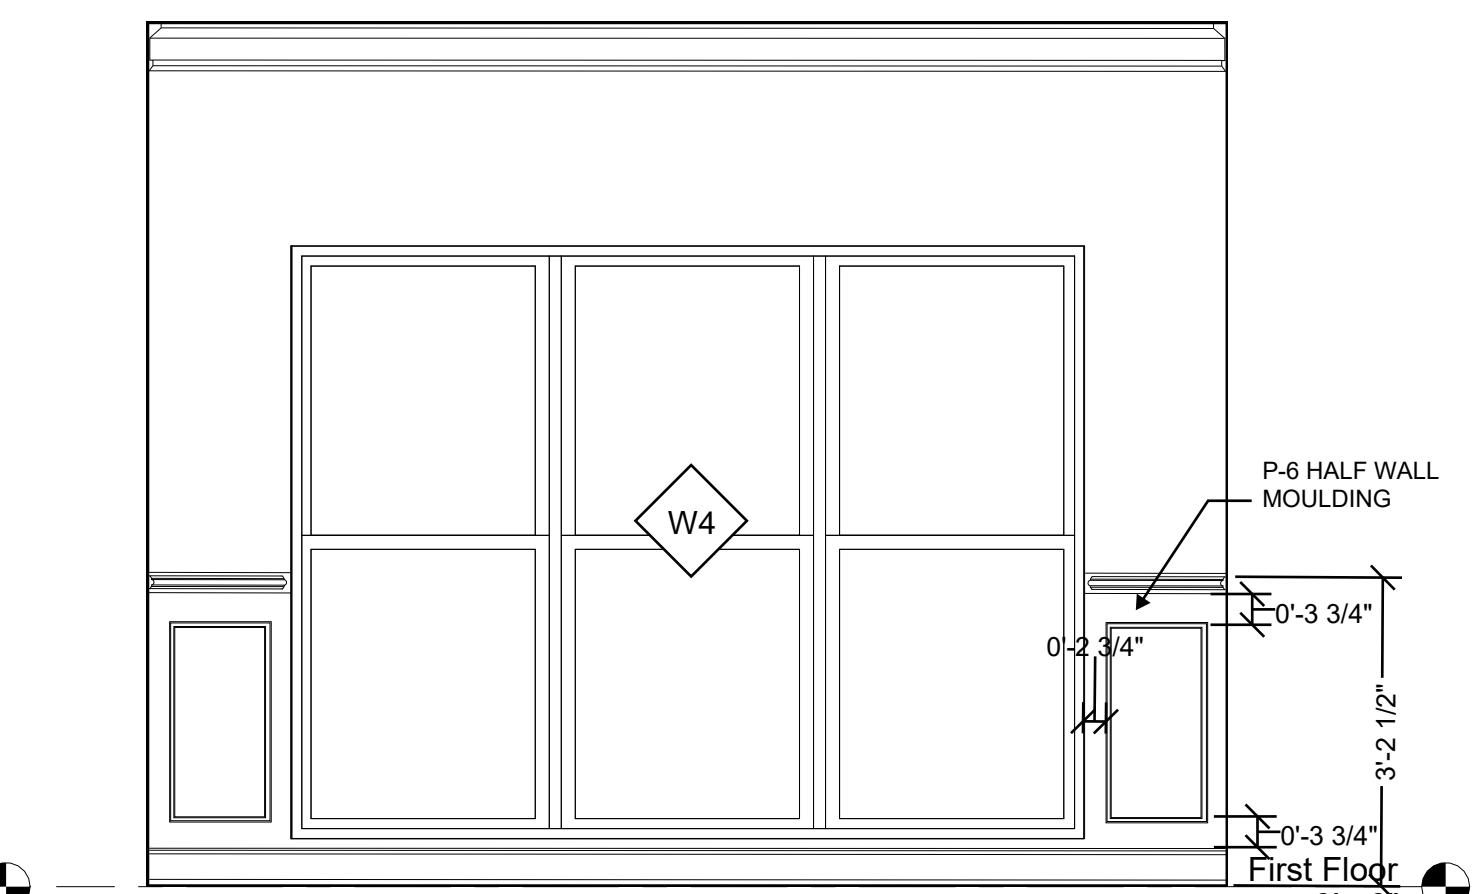

INTERIOR ELEVATION - DINING ROOM

WEST


1/2" = 1'-0"

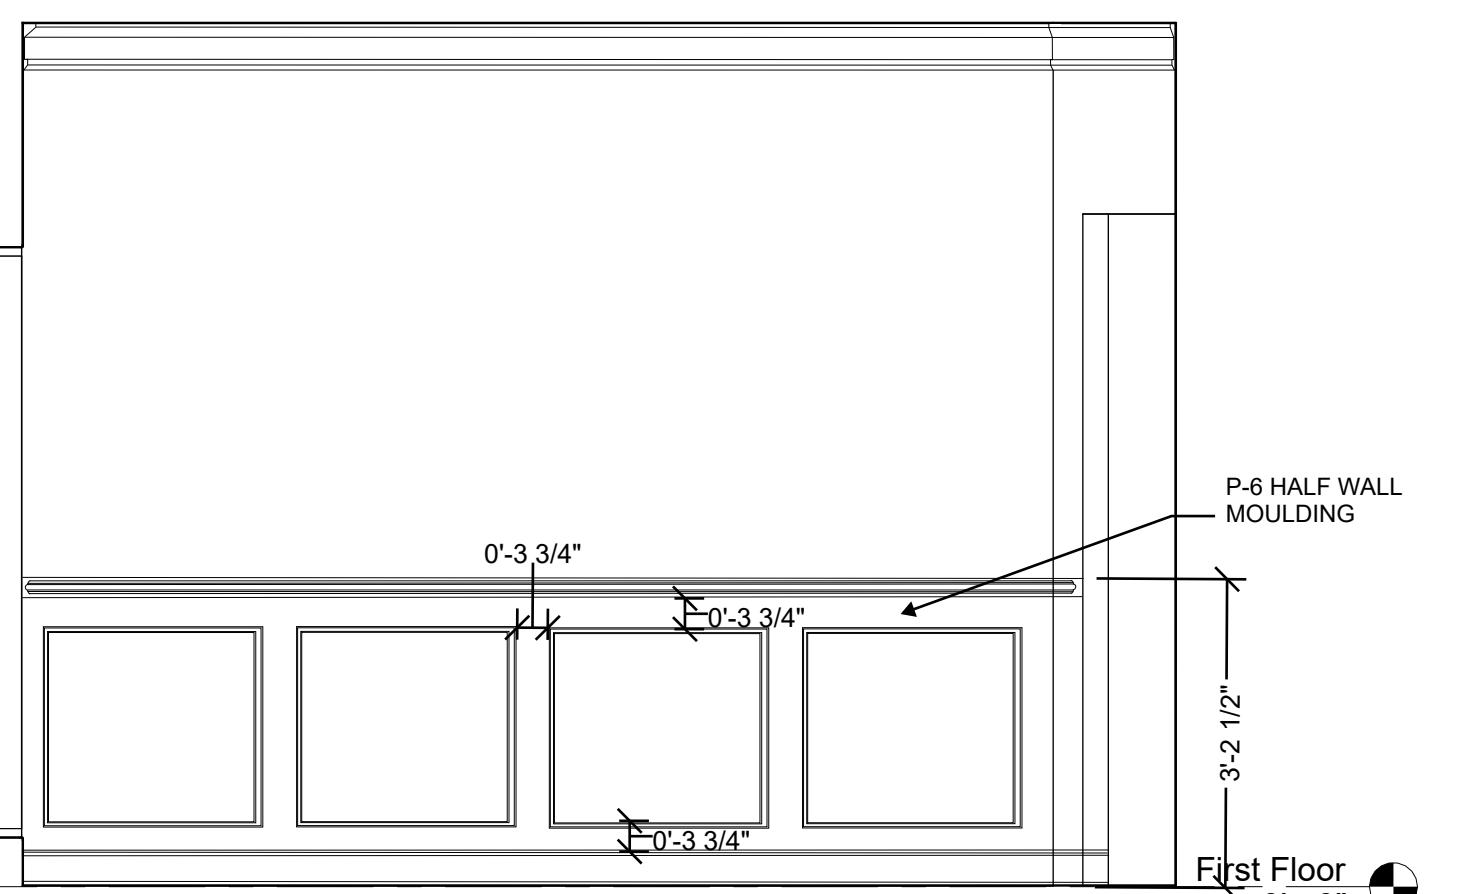

INTERIOR ELEVATION - DINING ROOM

NORTH


1/2" = 1'-0"

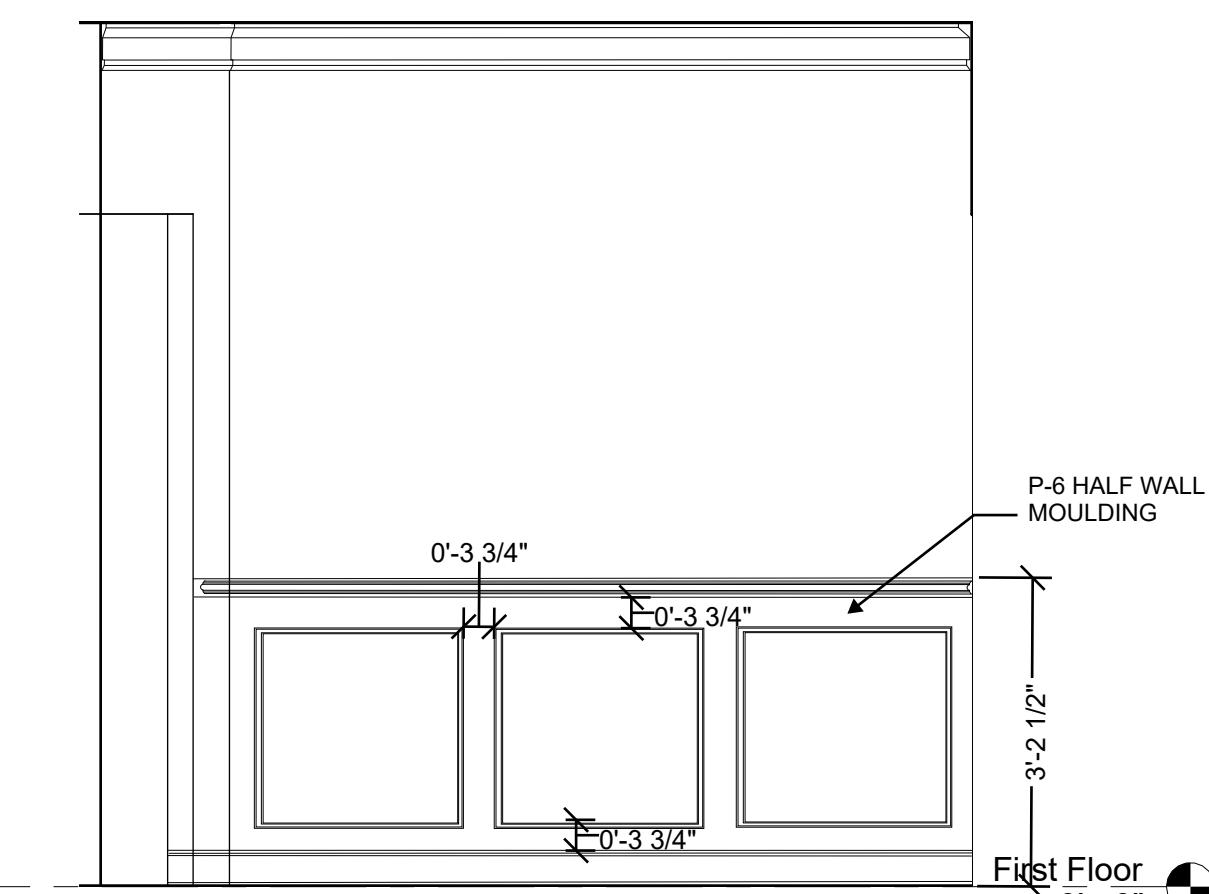

INTERIOR ELEVATION - DINING ROOM


EAST

1/2" = 1'-0"

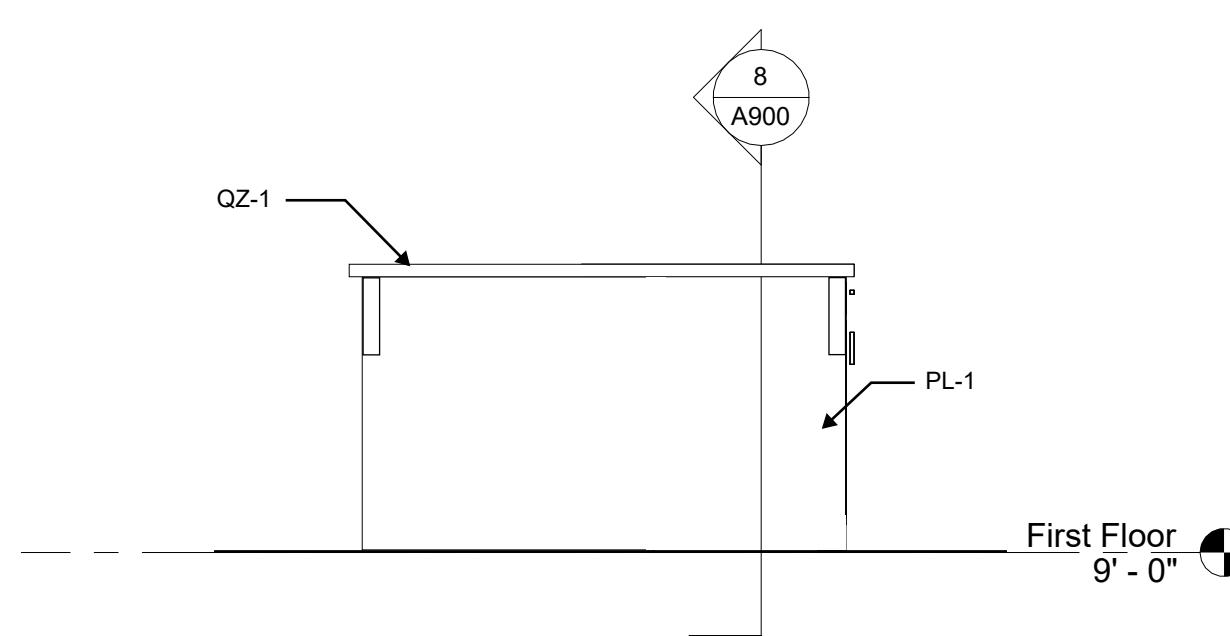


④ INTERIOR ELEVATION - ISLAND SOUTH

1/2" = 1'-0"

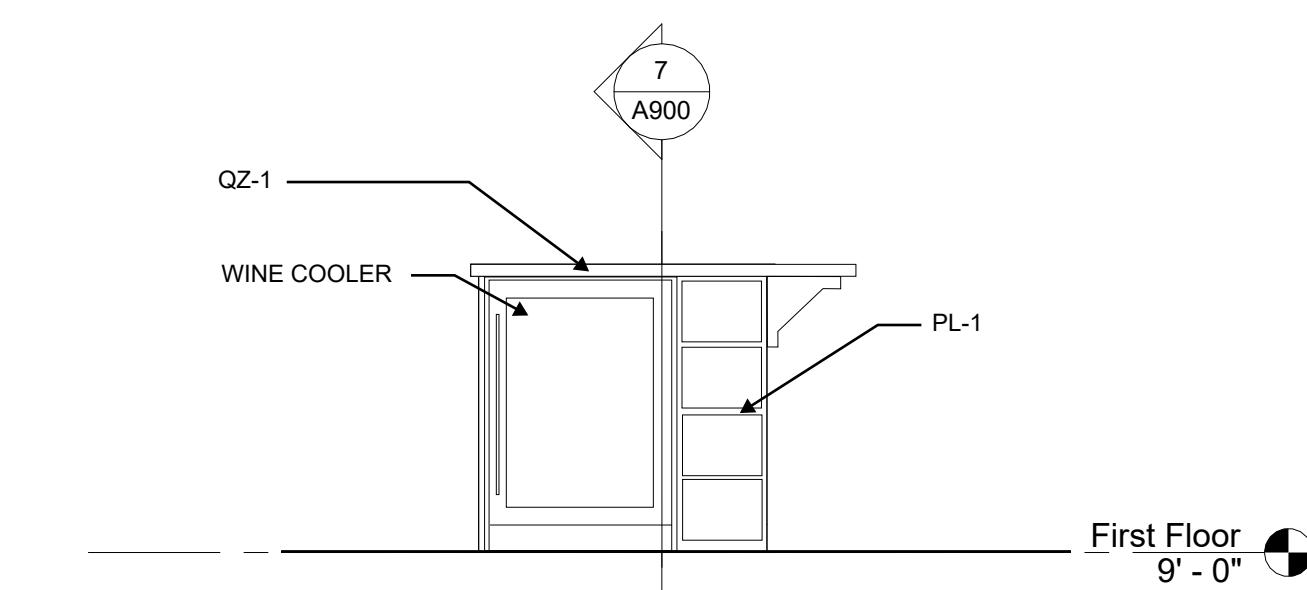


③ INTERIOR ELEVATION - ISLAND WEST

1/2" = 1'-0"

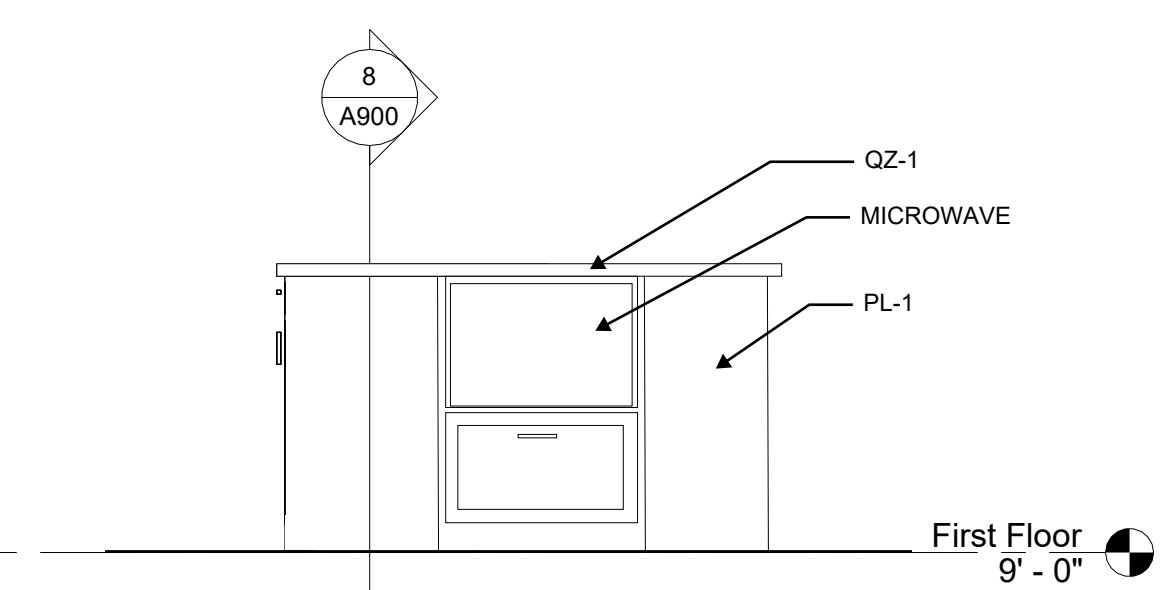


⑤ INTERIOR ELEVATION - ISLAND NORTH

1/2" = 1'-0"

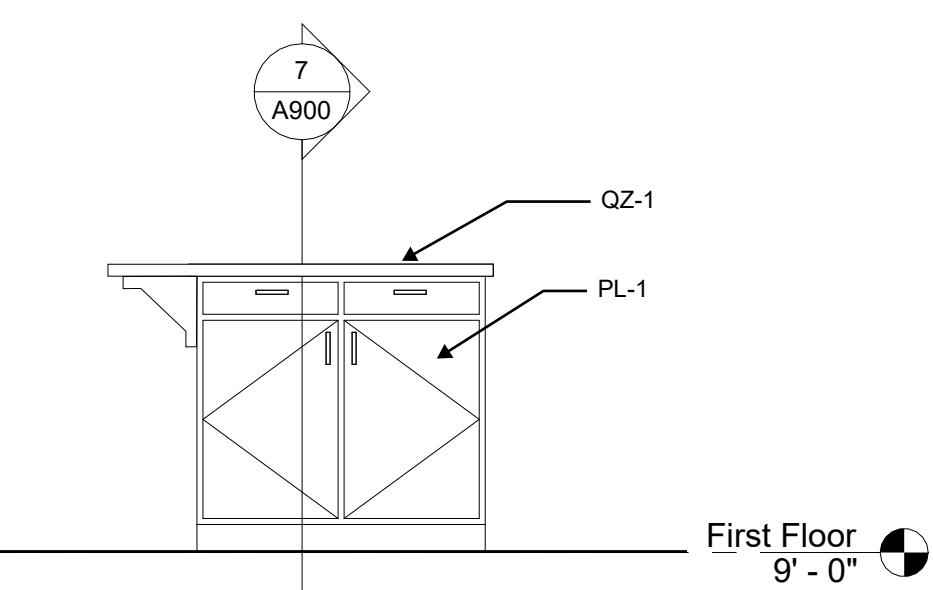


⑥ INTERIOR ELEVATION - ISLAND EAST

1/2" = 1'-0"

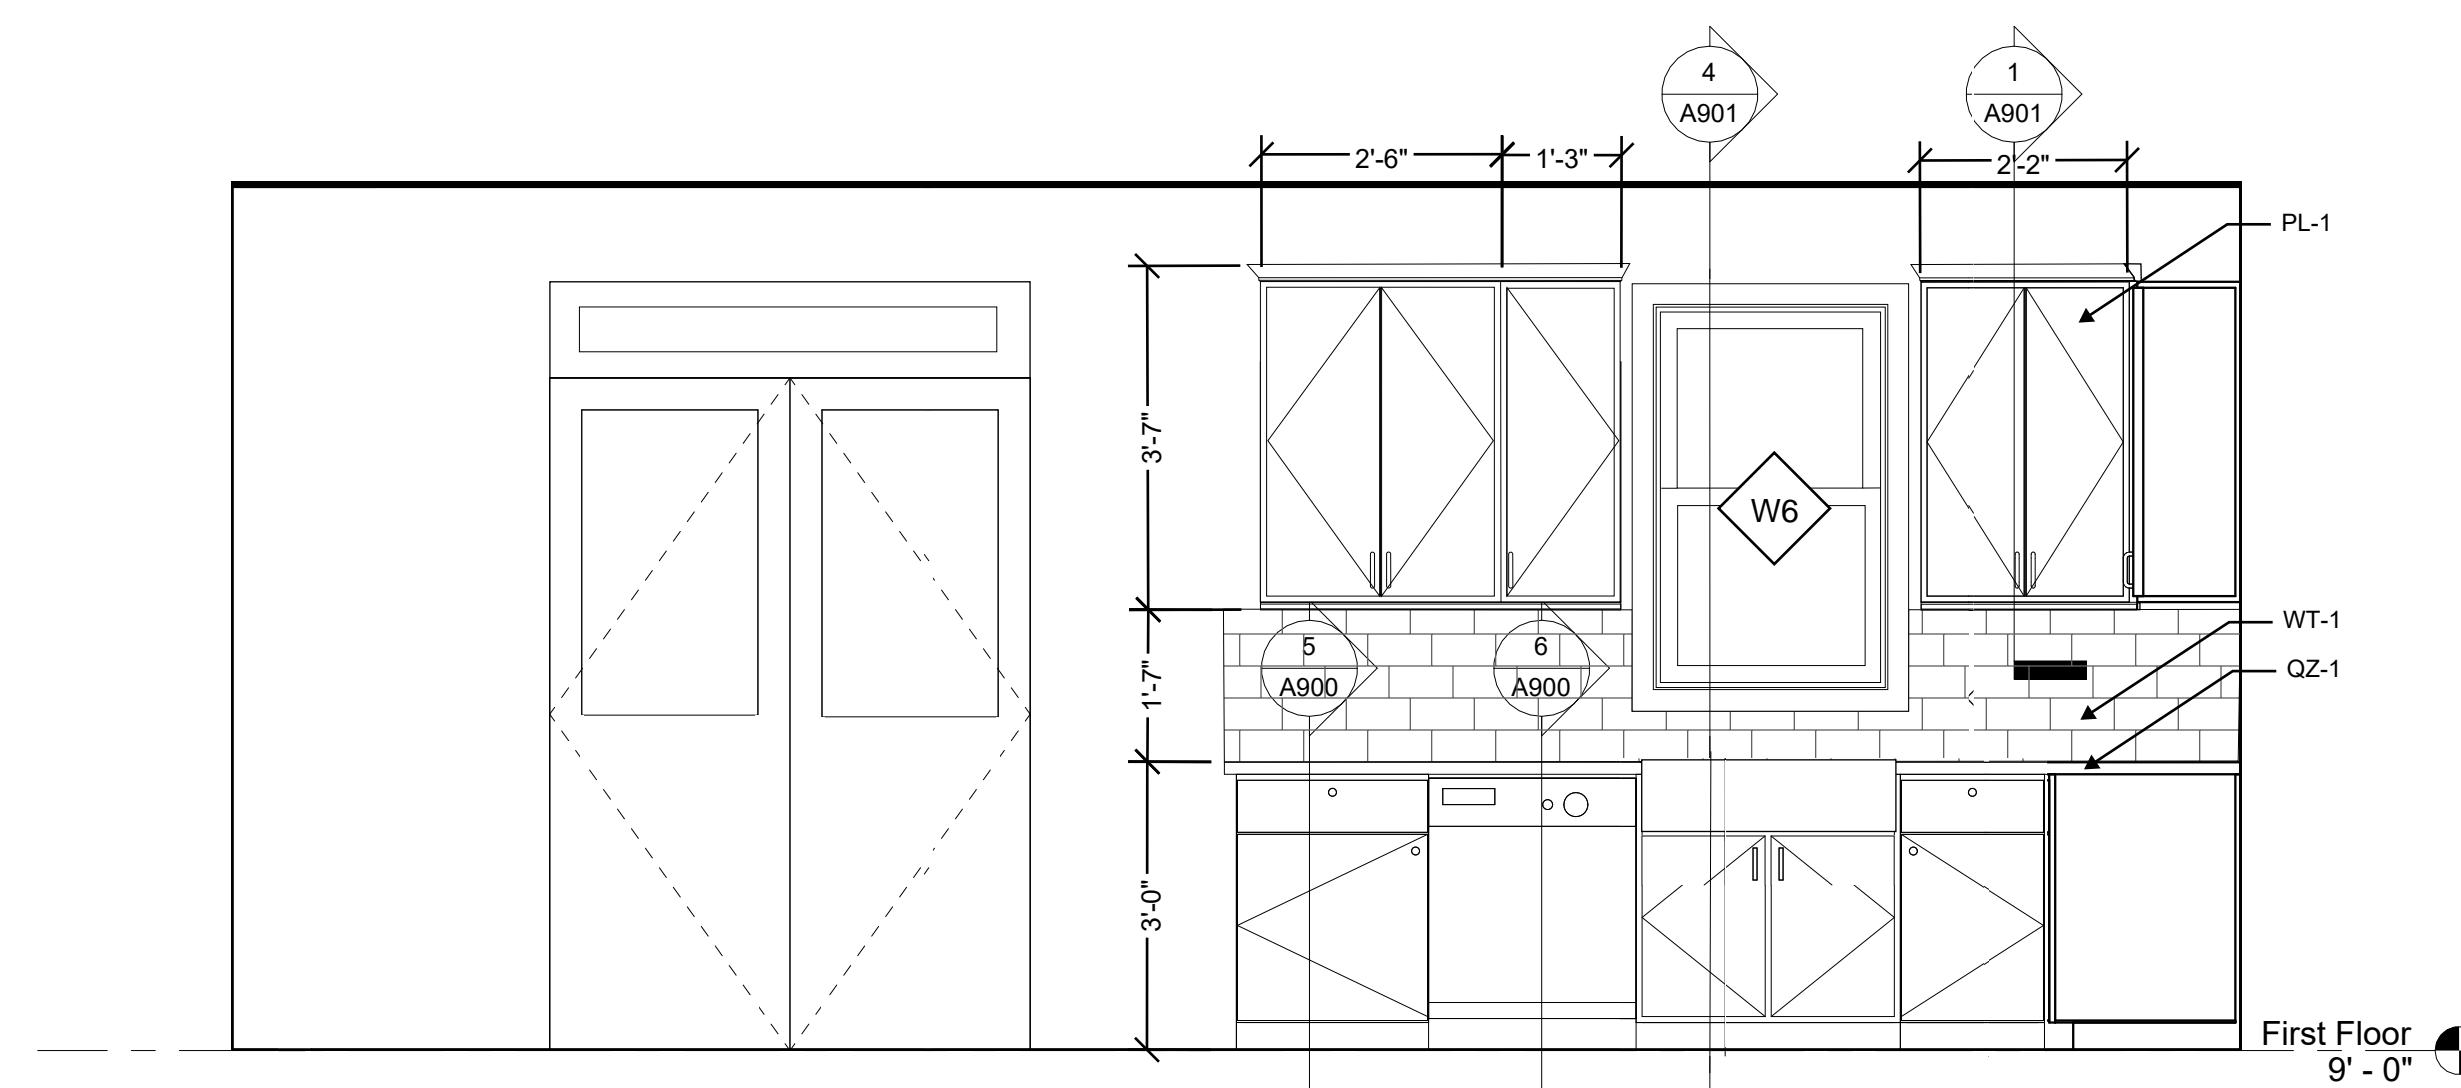

② INTERIOR ELEVATION - KITCHEN NORTH

1/2" = 1'-0"

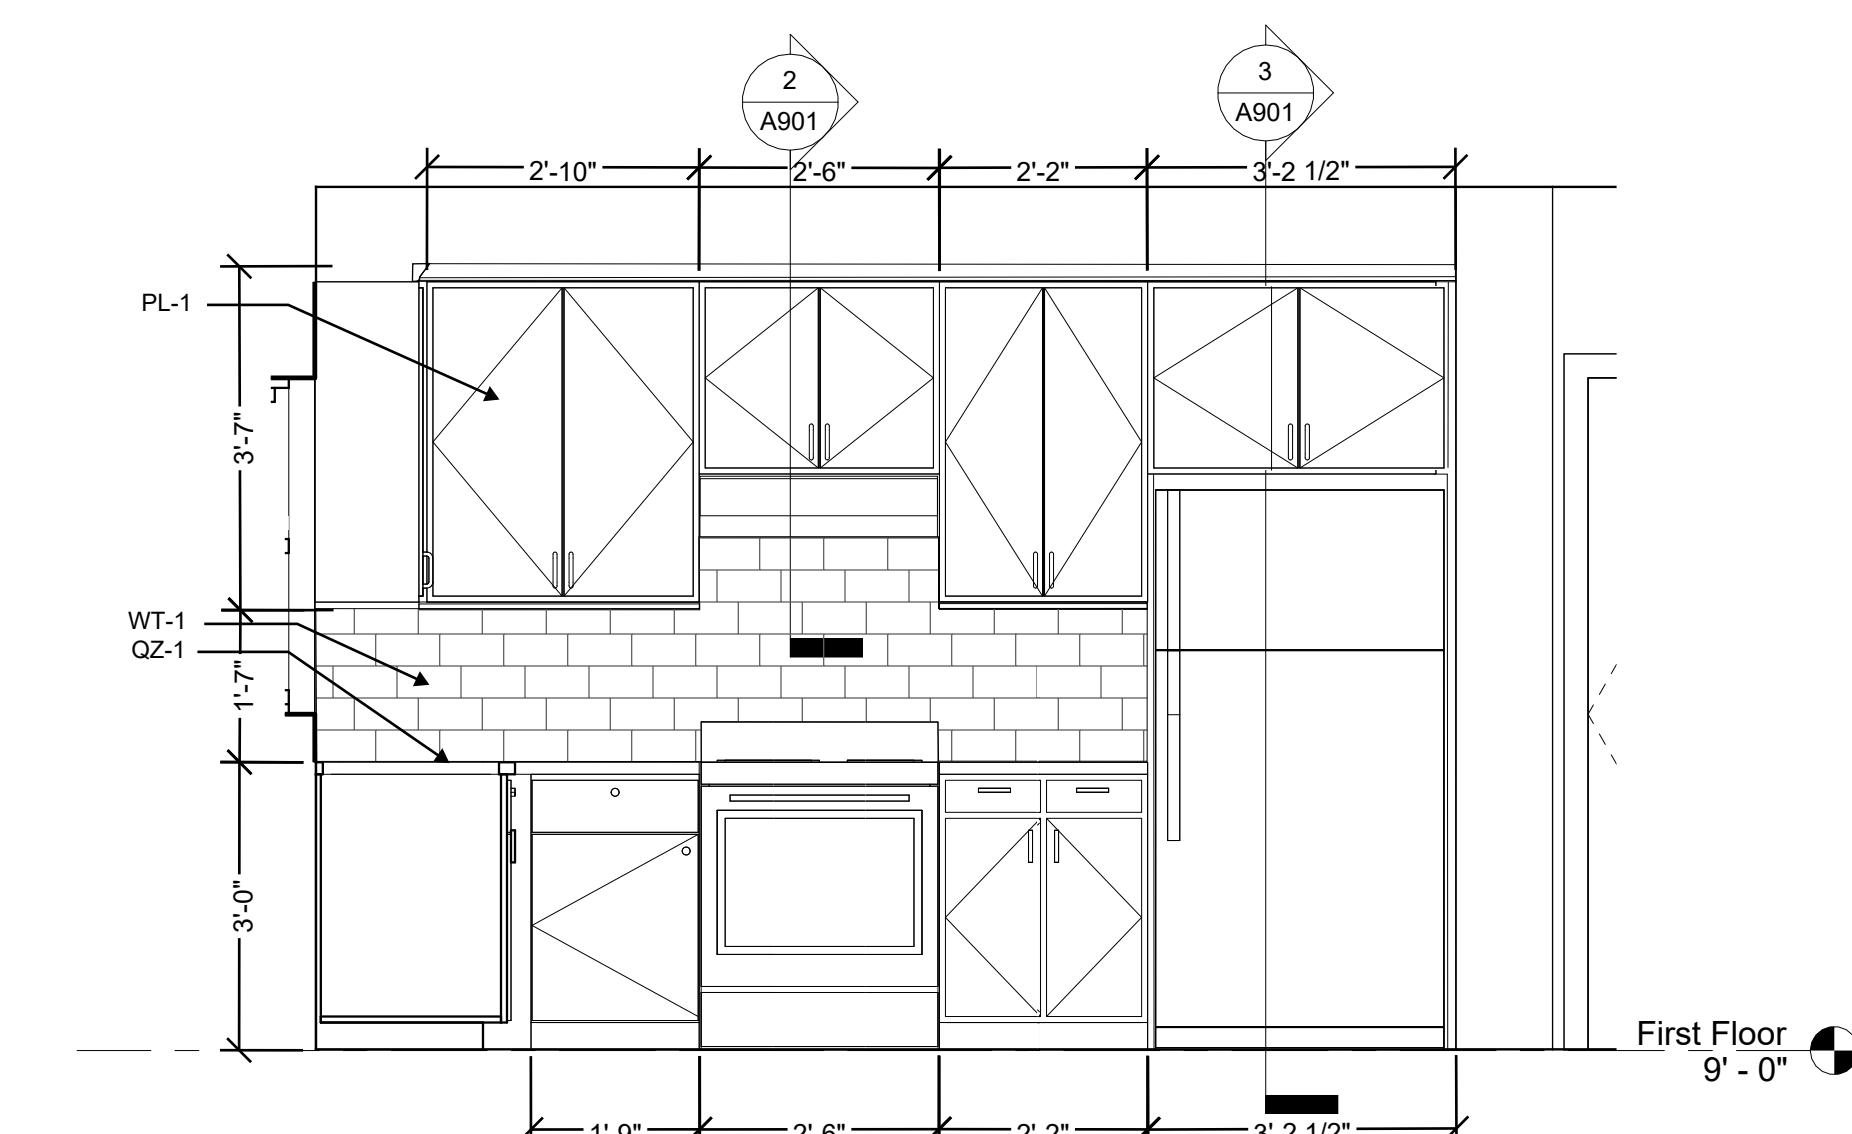

① INTERIOR ELEVATION - KITCHEN EAST

1/2" = 1'-0"

SINGLE FAMILY HOUSE 4 BEDROOM 3.5 BATH

CIOFFI FAMILY

404 PEACHTREE CIRCLE
ATLANTA, GA 30318


Project number 2023.001
Issue Date 09.06.23

CONSTRUCTION DOCUMENTS

Revisions
No. Description Date

INTERIOR ELEVATIONS

A701

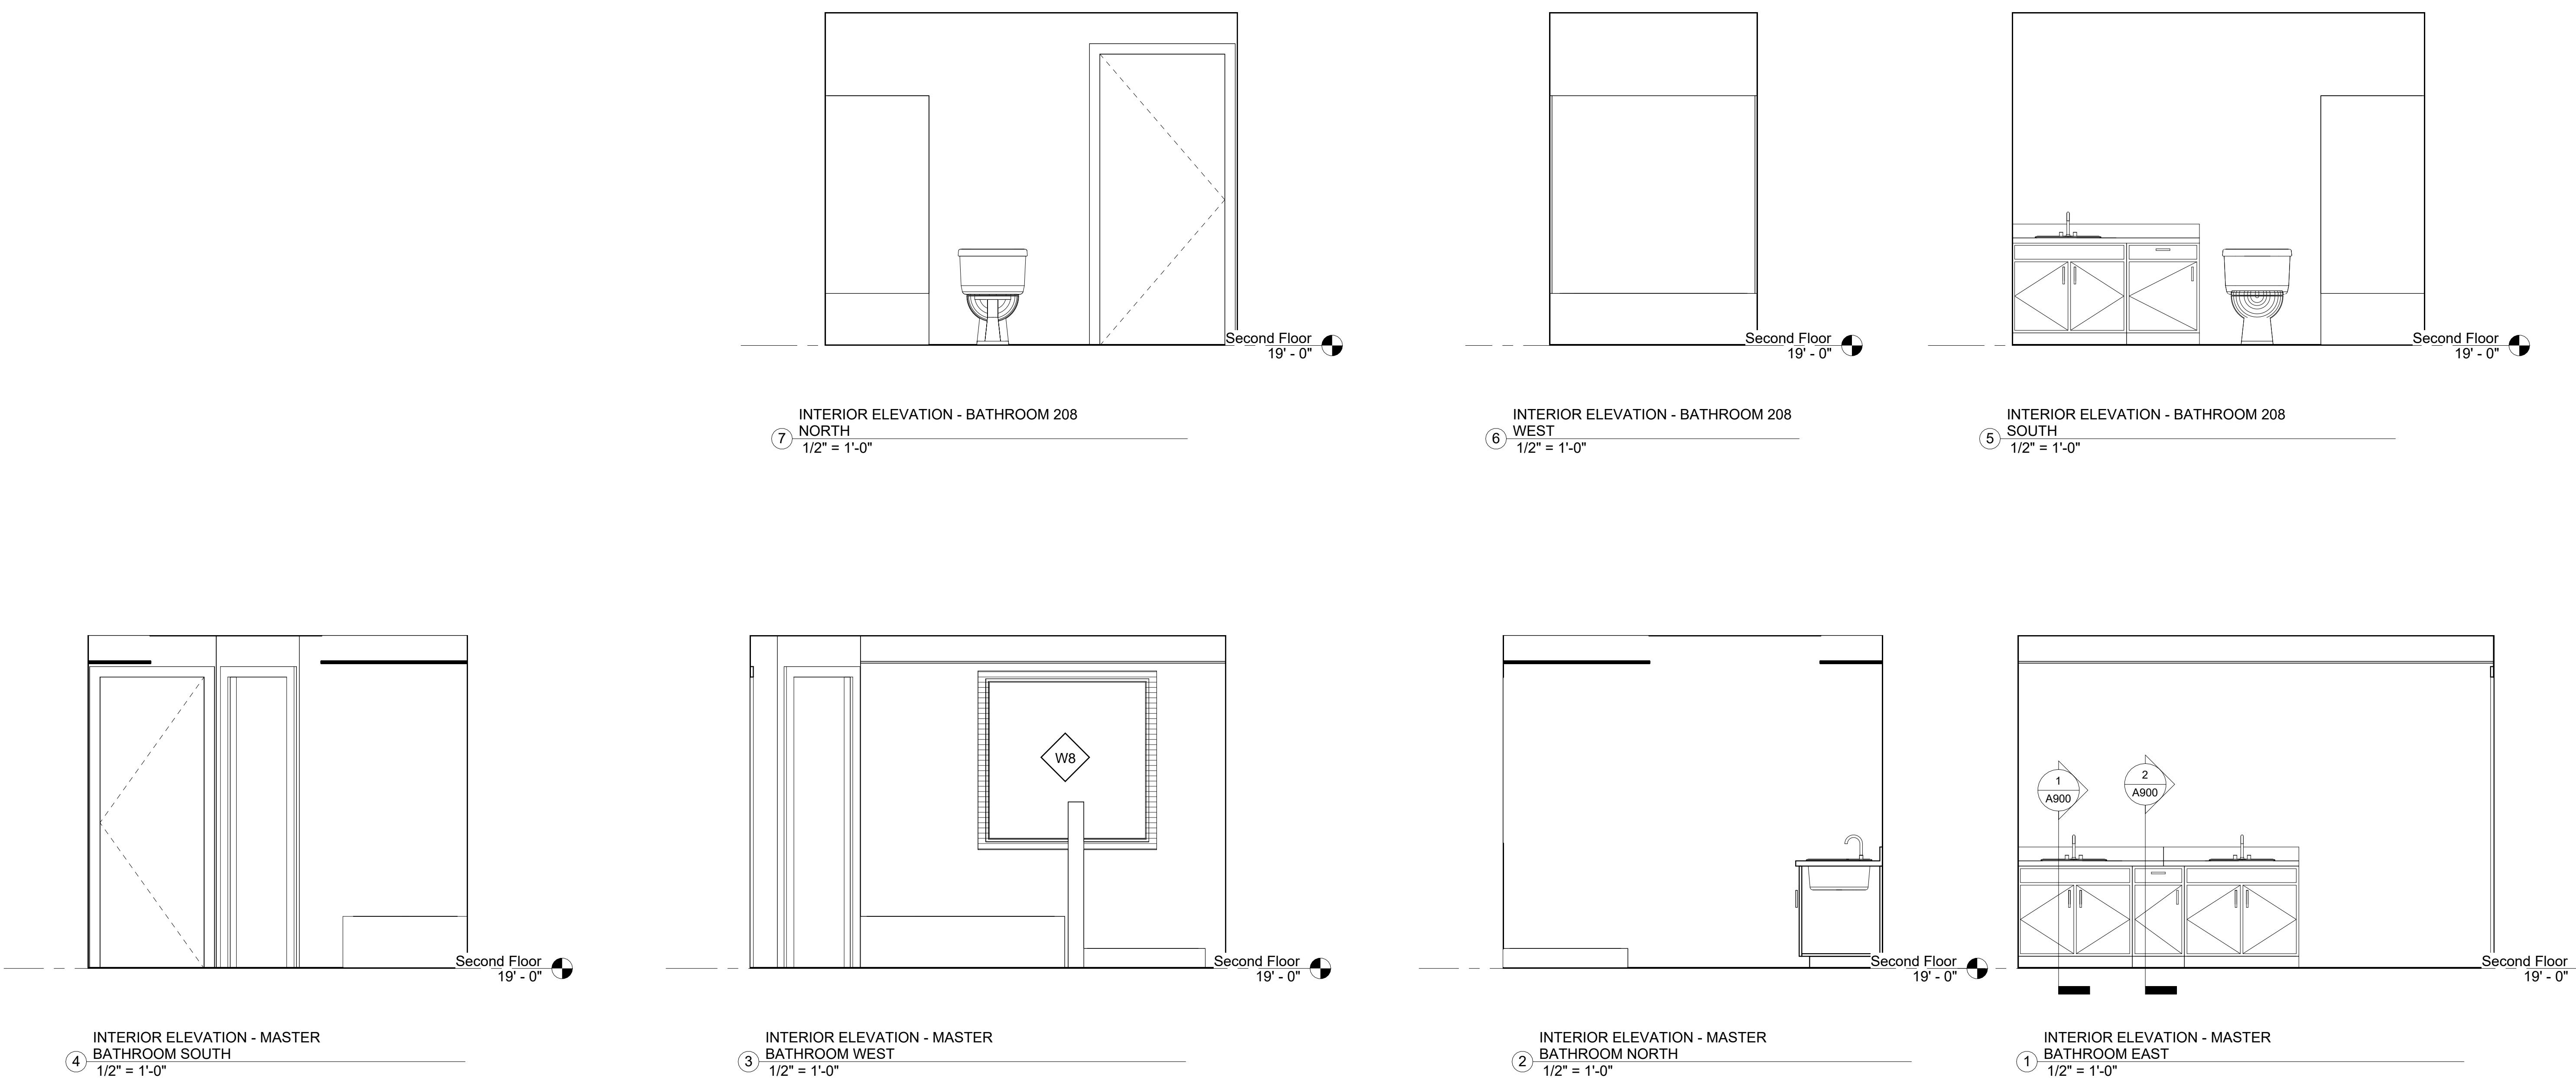

SINGLE FAMILY HOUSE 4 BEDROOM 3.5 BATH

CIOFFI FAMILY
404 PEACHTREE CIRCLE
ATLANTA, GA 30318



Project number 2023.001
Issue Date 09.06.23

CONSTRUCTION DOCUMENTS

Revisions
No. Description Date


INTERIOR ELEVATIONS

A702

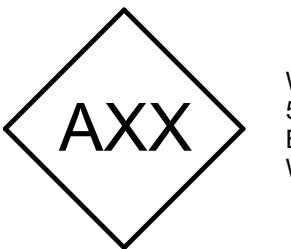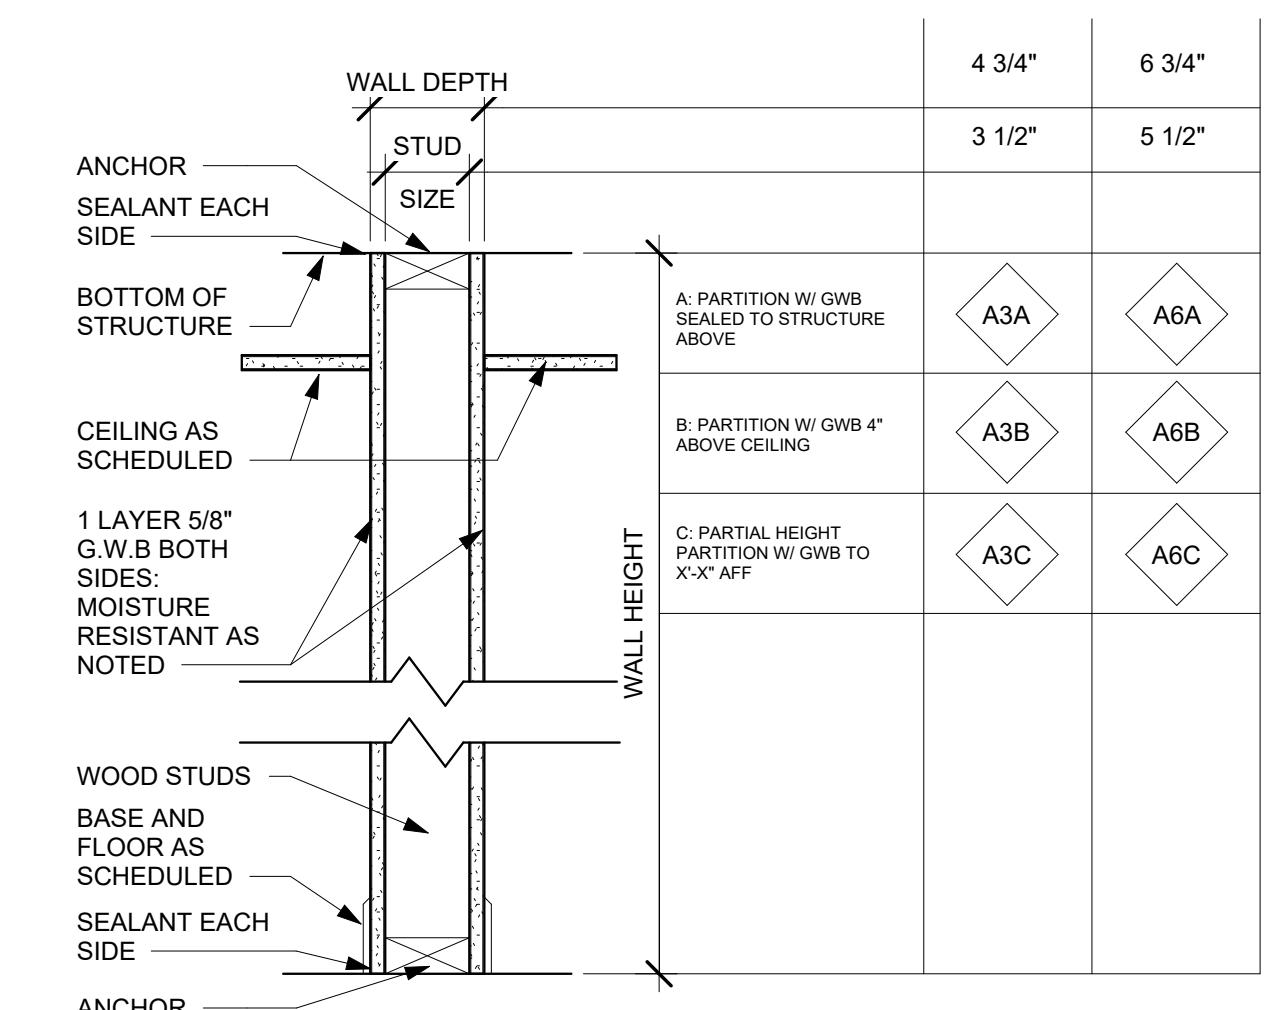

WALL TYPE A:
5/8" G.W.B. ON
BOTH SIDES
WOOD STUDS

Architect Seal

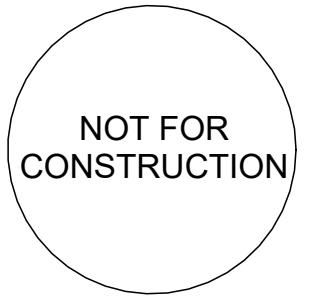

SINGLE FAMILY HOUSE 4 BEDROOM 3.5 BATH

CIOFFI FAMILY
404 PEACHTREE CIRCLE
ATLANTA, GA 30318

Project number 2023.001
Issue Date 09.06.23

CONSTRUCTION DOCUMENTS


Revisions	No.	Description	Date
-----------	-----	-------------	------

WALL TYPES

A800

Door Number	Door Type	Door Size	Manufacturer	Model	Frame Type	Fire Rating	Details			Finish			Comments
							Head	Jamb	Sill	Description	Door	Frame	
001A	58	96" x 84"											
001B	58	96" x 84"											
002	57	72" x 84"											
003	34	36" x 84"											
004	34	36" x 84"											
005	37	30" x 84"											
006	37	30" x 84"											
015	34	36" x 84"											
023	34	36" x 84"											
100	41	36" x 84"											
101	60	36" x 84"											
102	67	72" x 84"											
103	68	48" x 84"											
104	69	60" x 84"											
105	34	36" x 84"											
106	37	30" x 84"											
107	59	24" x 84"											
108	37	30" x 84"											
202	34	36" x 84"											
203	37	30" x 84"											
204	37	30" x 84"											
205	37	30" x 84"											
206	37	30" x 84"											
207	59	24" x 84"											
209	34	36" x 84"											
210	70	60" x 84"											
211	34	36" x 84"											
212	70	60" x 84"											
213	37	30" x 84"											

Architect Seal

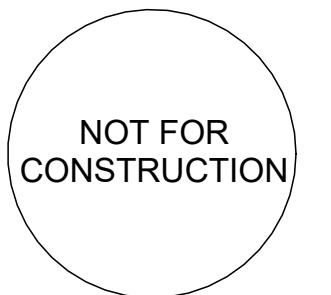

SINGLE FAMILY HOUSE 4 BEDROOM 3.5 BATH

CIOFFI FAMILY

404 PEACHTREE CIRCLE
ATLANTA, GA 30318

Project number 2023.001
Issue Date 09.06.23

CONSTRUCTION DOCUMENTS

Revisions	No.	Description	Date
-----------	-----	-------------	------

DOOR SCHEDULE & TYPES

A820


Scale

As Indicated

Window Schedule

Type Mark	Rough Opening			Type	Material	Finish	Detail			Glazing		Comments
	Width	Height	Head Height				Head	Jamb	Sill	Thickness	Type	
W1	2' - 8"	5' - 0"	6' - 8"	Double Hung - Single	Wood	P-1	2/A600	Jamb	1/A600	1/2"	GL-1	Fabric Roman Blinds
W2	5' - 6"	5' - 0"	6' - 8"	Double Hung - Double	Wood	P-1	7/A601	Jamb	6/A601	1/2"	GL-1	PVC Venetian Blinds
W3	8' - 0"	6' - 2"	7' - 10"	Double Hung - Triple	Wood	P-1	3/A600	3/A620	2/A600	1/2"	GL-1	Wood Plantation Shutters
W4	7' - 2"	6' - 2"	6' - 8"	Double Hung - Triple	Wood	P-1	8/A601	Jamb	7/A601	1/2"	GL-1	PVC Venetian Blinds
W5	2' - 8"	5' - 0"	6' - 8"	Double Hung - Single	Wood	P-1	8/A601	Jamb	7/A601	1/2"	GL-1	PVC Venetian Blinds
W6	2' - 8"	3' - 10"	7' - 10"	Double Hung - Single	Wood	P-1	8/A601	Jamb	7/A601	1/2"	GL-1	PVC Venetian Blinds
W7	4' - 0"	4' - 0"	6' - 8"	Fixed - Single	Wood	P-1	8/A601	Jamb	7/A601	1/2"	GL-1	PVC Venetian Blinds

Architect Seal

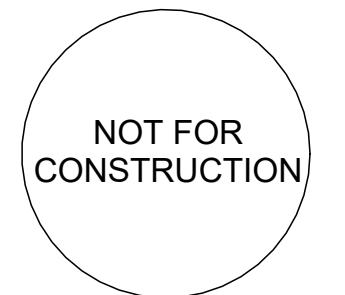

SINGLE FAMILY HOUSE 4 BEDROOM 3.5 BATH

CIOFFI FAMILY

404 PEACHTREE CIRCLE
ATLANTA, GA 30318

Project number 2023.001

Issue Date 09.06.23

CONSTRUCTION DOCUMENTS

Revisions	No.	Description	Date
-----------	-----	-------------	------

WINDOW SCHEDULE & TYPES


A840

Scale

As Indicated

FINISH SCHEDULE							
LEGEND	MATERIAL	MANUFACTURER	STYLE	COLOR	DESCRIPTION	NOTES	INSTALLATION COMMENTS
CEILINGS							
BB-1	BEADBOARD WOOD	ARMSTRONG	WOODHAVEN	WHITE	5" x 7'	TOUNGE AND CROOVE CEILING PLANK	REFER TO DETAILS
GWB-1	GYPSUM	USG	-	WHITE	-	-	REFER TO DETAILS
FLOOR FINISHES							
CPT-1	CARPET	INTERFACE CARPET	WORLD WOVEN	BEIGE	ROLL	-	-
CT-1	CERAMIC TILE	CASTILLE	LEVANTE	CREAM	12" x 12"	--	--
HW-1	HARDWOOD	BRUCE AMERICAN	ORIGINALS	OAK	STAINED FINISH	3/4"	-
SC	SEALED CONCRETE	-	ACRYLIC SEALER	CLEAR	NO POLISH	-	-
MILLWORK							
PL-1	PLASTIC LAMINATE	WILSONART	OAK	GOLDEN OAK	KITCHEN CABINETS	--	--
PL-2	PLASTIC LAMINATE	WILSONART	MELAMINE	WHITE	BATHROOM CABINETS	--	--
QZ-1	QUARTZ	LX HAUSYS	INTERMEZZO	GREEN	COUNTERTOP	POLISHED FINISH	--
SS-1	SOLID SURFACE	LX HAUSYS	GEMINI	WHITE	COUNTERTOP	POLISHED FINISH	--
WT-1	WALL TILE	TILEBAR	MONTAUK GIN	WHITE	BACKSPLASH	4X4	--
MOULDING							
WB-1	WALL BASE	FLOOR & DECOR	BASE	P-1	4 1/2"	REFER TO ELEVATIONS	INSTALLATION COMMENTS
WB-2	WALL BASE	FLOOR & DECOR	BASE	P-1	6"	REFER TO ELEVATIONS	INSTALLATION COMMENTS
WB-3	WALL BASE	FLOOR & DECOR	BASE	P-1	6"	REFER TO ELEVATIONS	INSTALLATION COMMENTS
CR-1	CHAIR RAIL	FLOOR & DECOR	WALL	P-8	--	REFER TO ELEVATIONS	INSTALLATION COMMENTS
WALL FINISHES							
P-1	PAINT	BEHR	PREMIUM PLUS	WHITE	EGGSHELL	-	-
P-2	PAINT	BEHR	PREMIUM PLUS	LIGHT BLUE	EGGSHELL	-	-
P-3	PAINT	BEHR	PREMIUM PLUS	MORNING YELLOW	FLAT	-	-
P-4	PAINT	BEHR	PREMIUM PLUS	LIGHT GREEN	EGGSHELL	-	-
P-5	PAINT	BEHR	ULTRA	COTTON KNIT	EGGSHELL	-	-
P-6	PAINT	BEHR	PREMIUM PLUS	DARK BEIGE	EGGSHELL	-	-
P-7	PAINT	BEHR	ULTRA	BALLERINA	SATIN	-	-
P-8	PAINT	BEHR	ULTRA	CAMEO WHITE	SEMI-GLOSS	-	-

Architect Seal

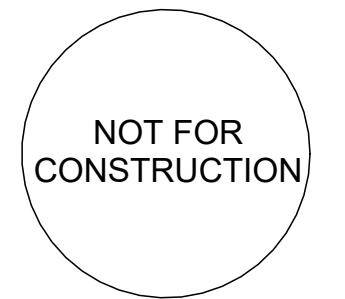

SINGLE FAMILY HOUSE 4 BEDROOM 3.5 BATH

CIOFFI FAMILY

404 PEACHTREE CIRCLE
ATLANTA, GA 30318



Project number 2023.001
Issue Date 09.06.23

CONSTRUCTION DOCUMENTS

Revisions	No.	Description	Date
-----------	-----	-------------	------



FINISH SCHEDULE

A860

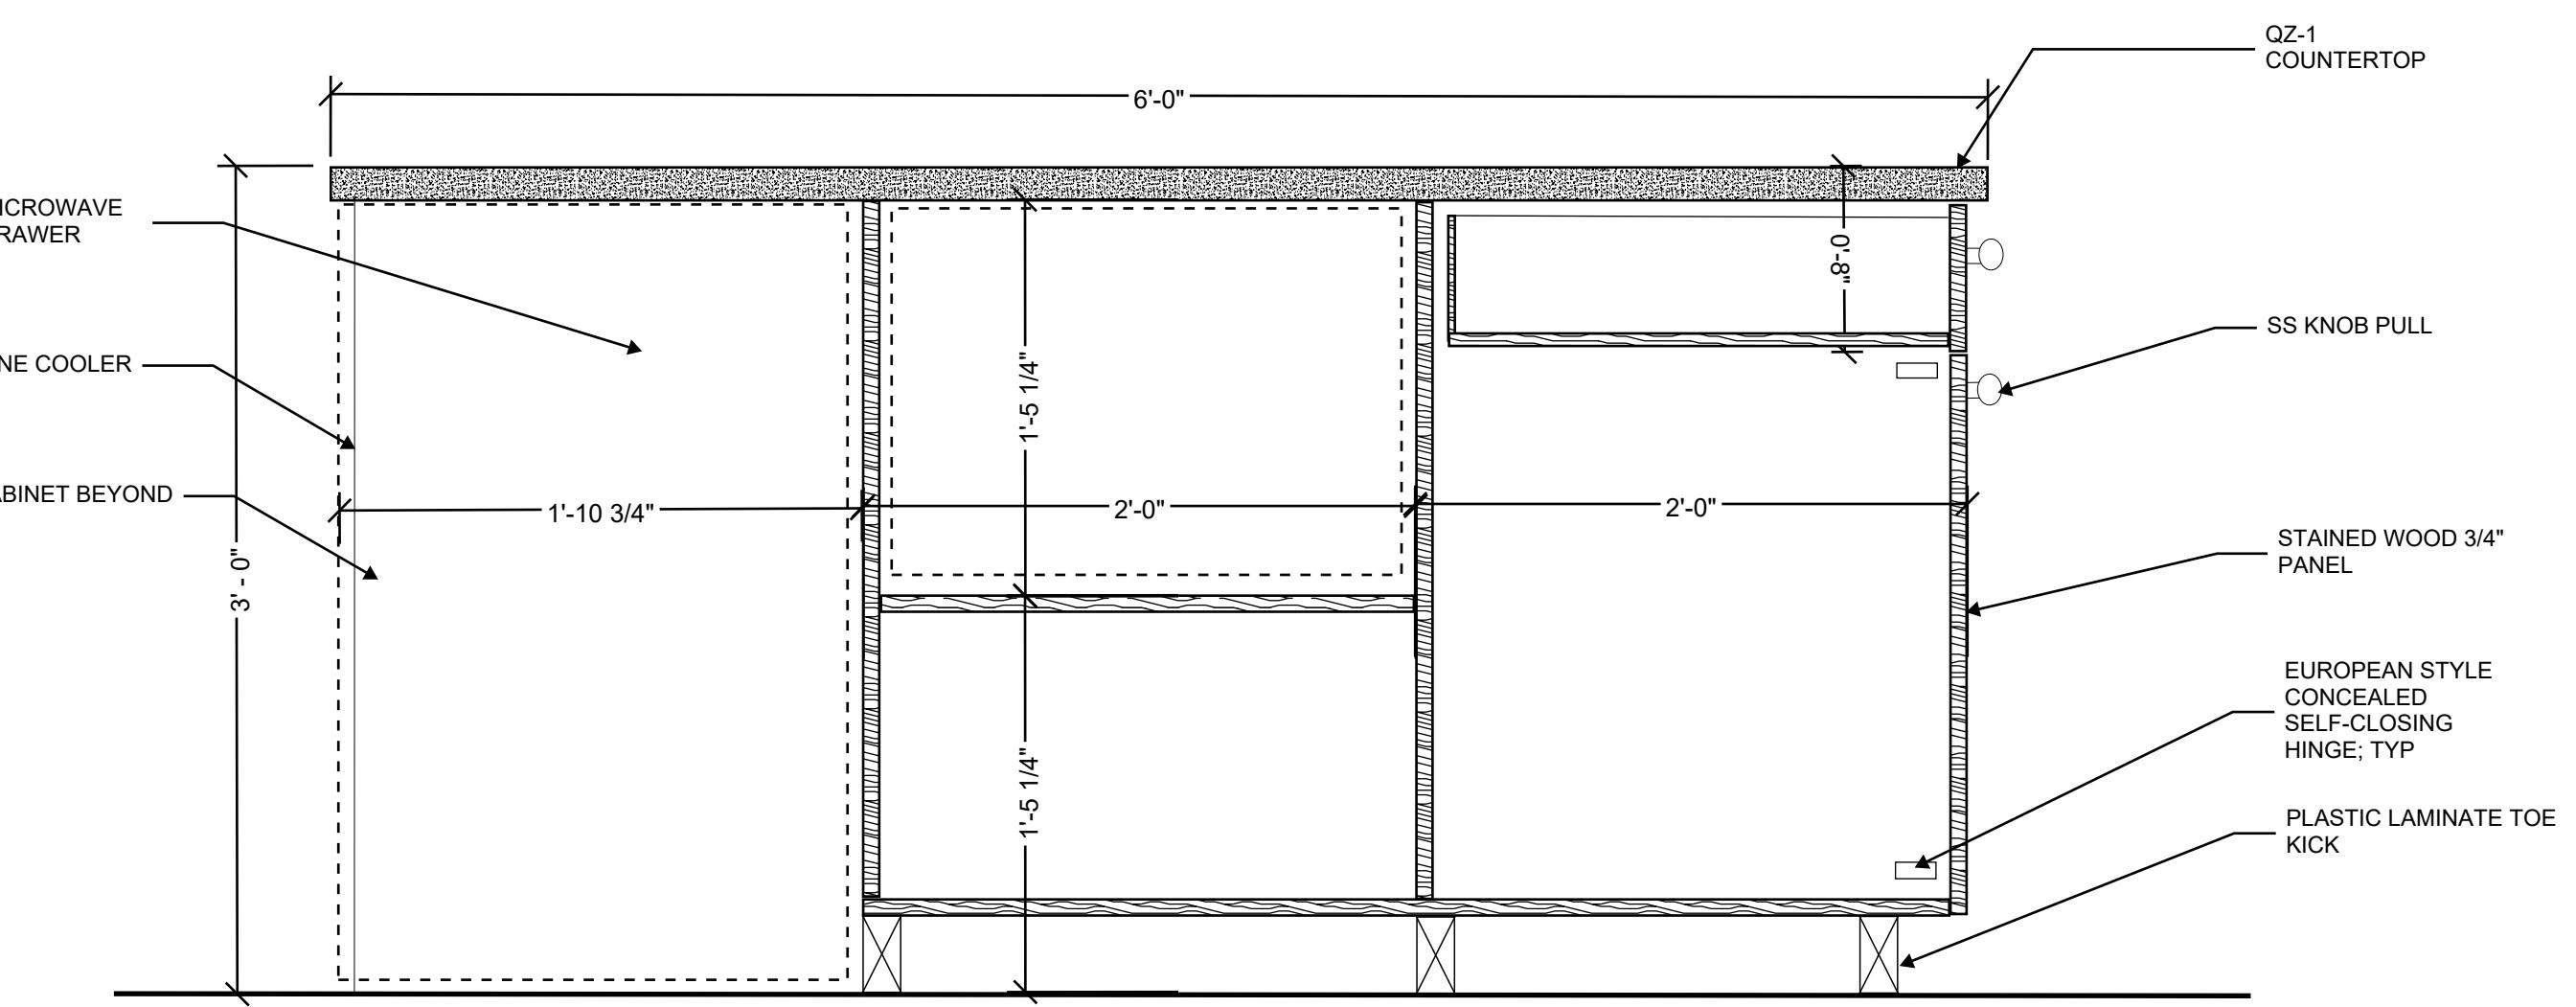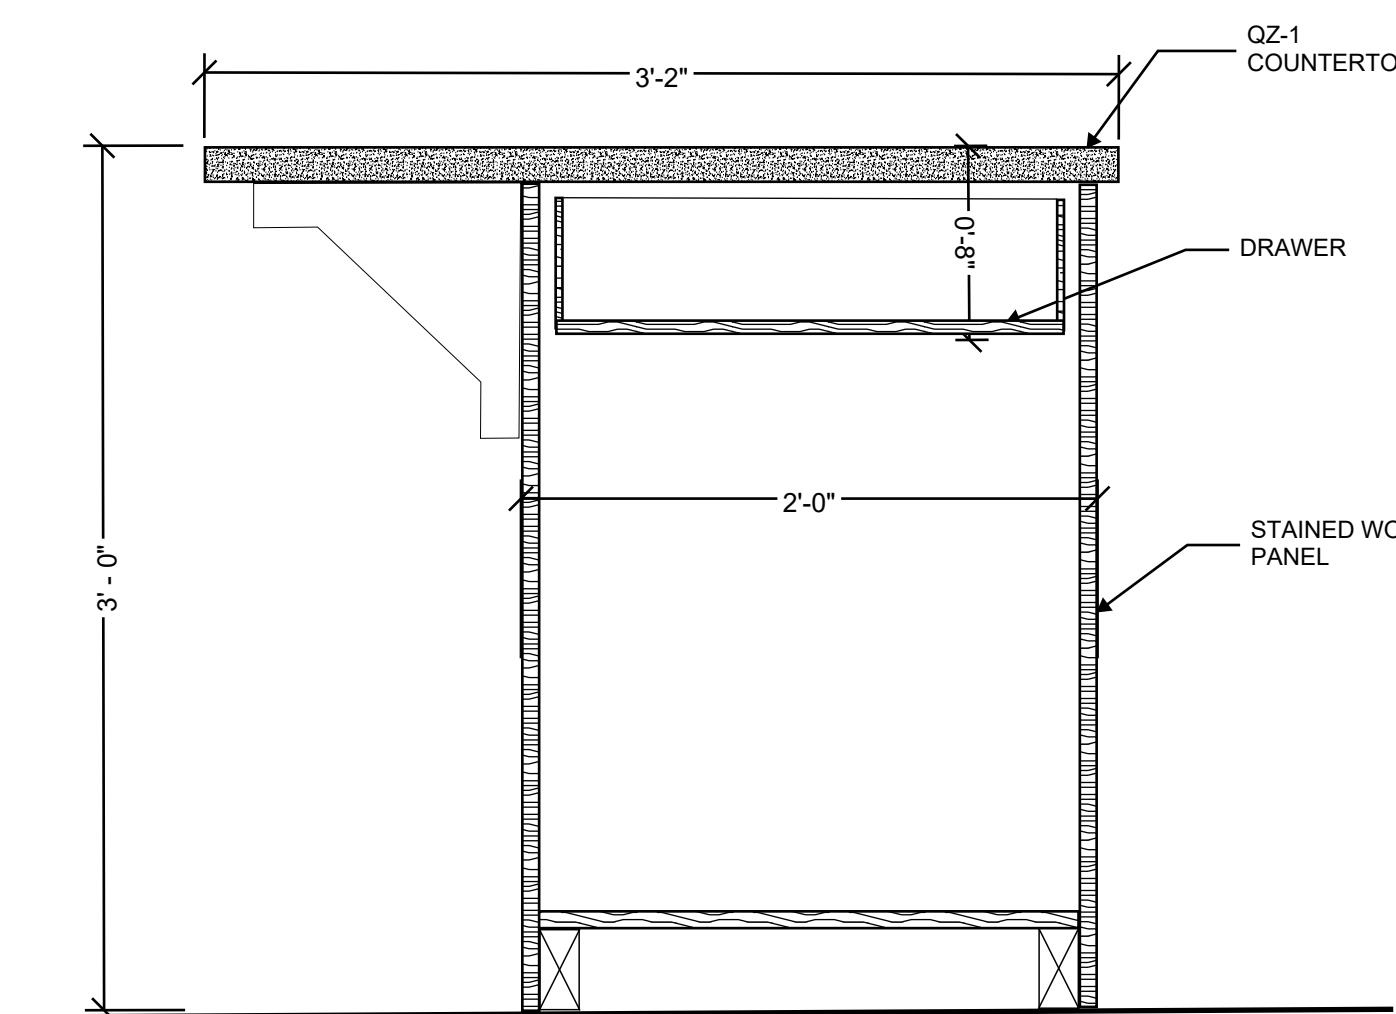

⑧ SECTION DETAIL - ISLAND WIDE
1 1/2" = 1'-0"

⑦ SECTION DETAIL - ISLAND LONG
1 1/2" = 1'-0"



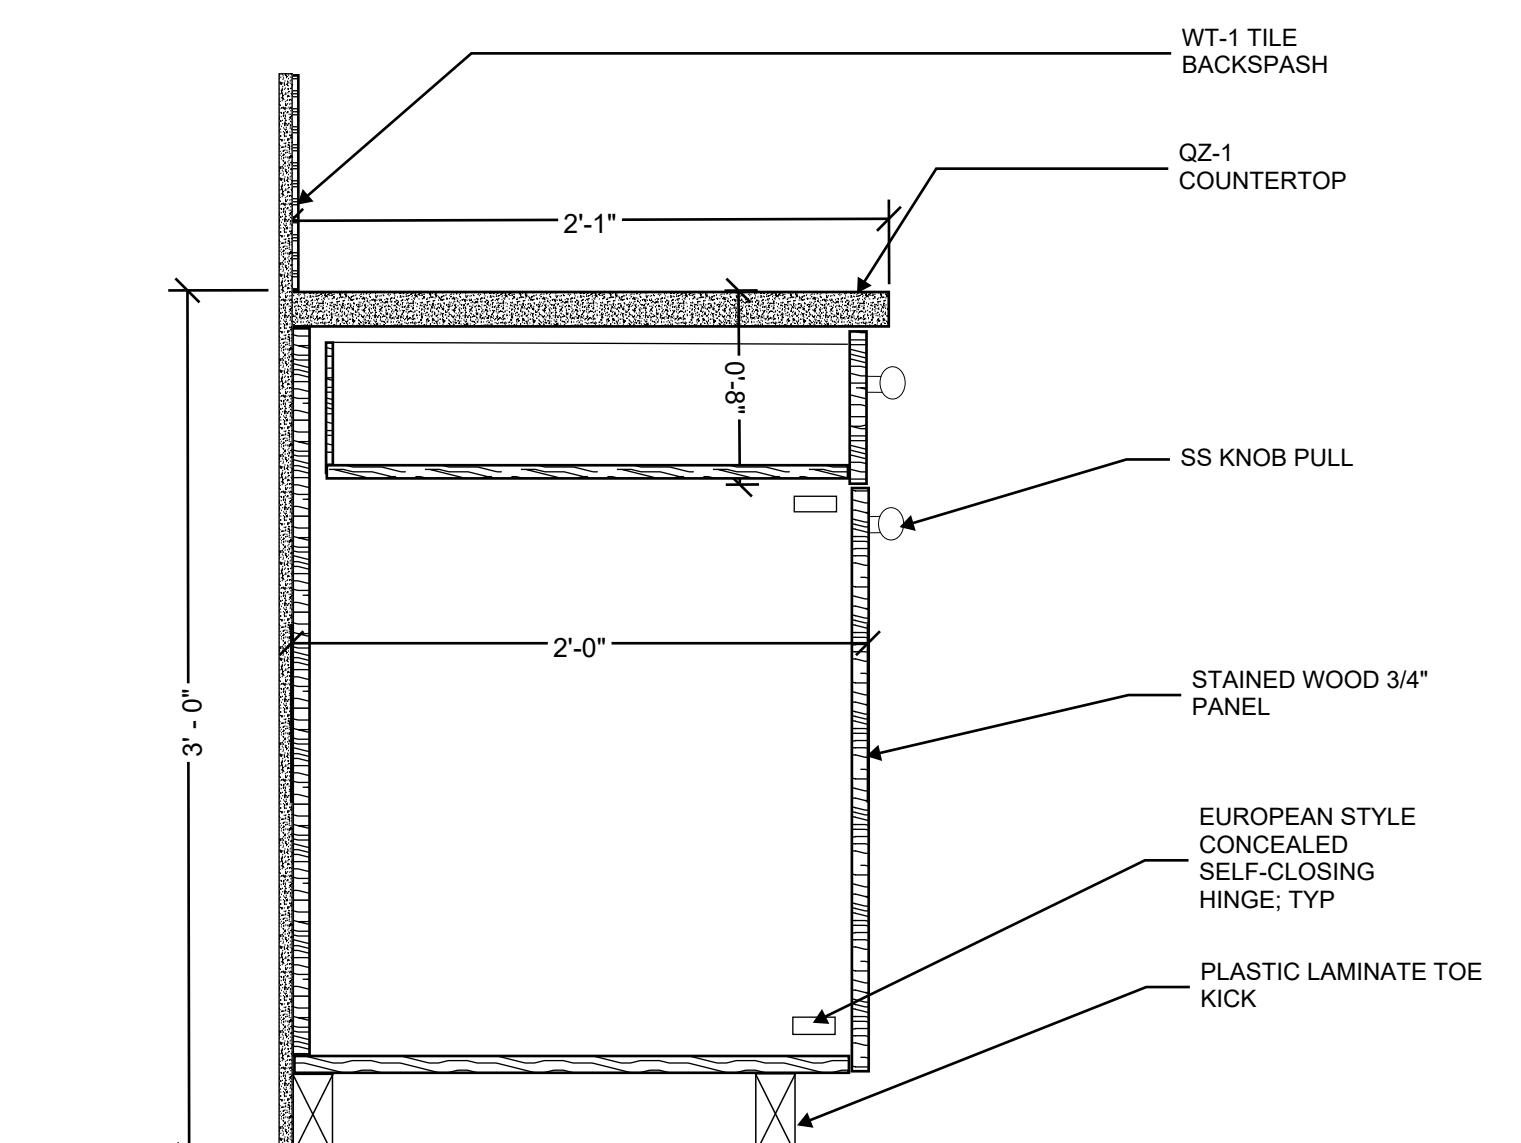
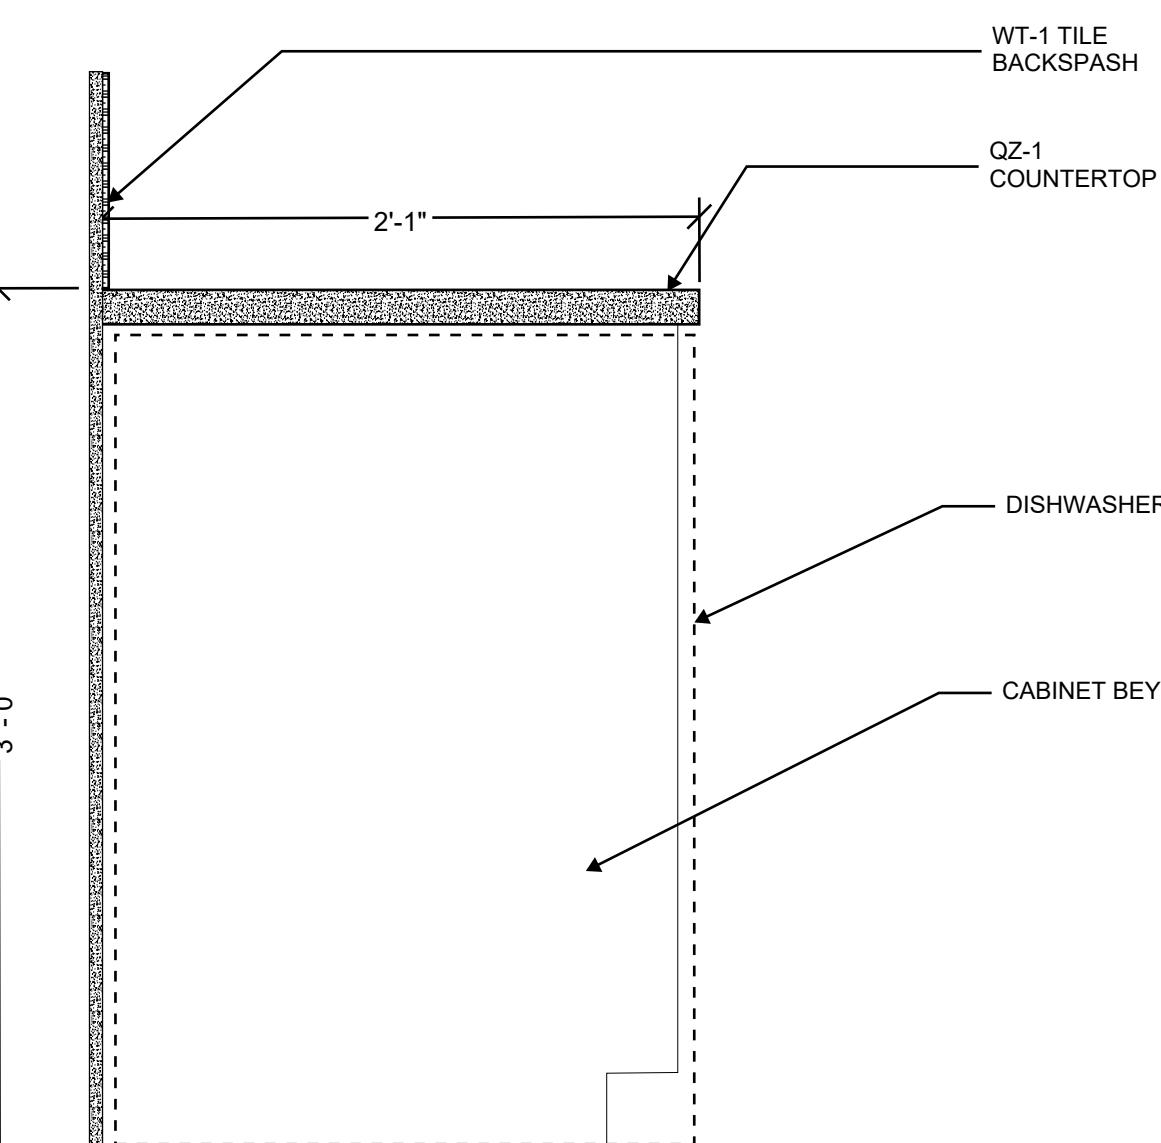


⑥ SECTION DETAIL - BASE CABINET OPEN
1 1/2" = 1'-0"

⑤ SECTION DETAIL - BASE CABINET DOOR AND DRAWER
1 1/2" = 1'-0"

Architect Seal

NOT FOR CONSTRUCTION

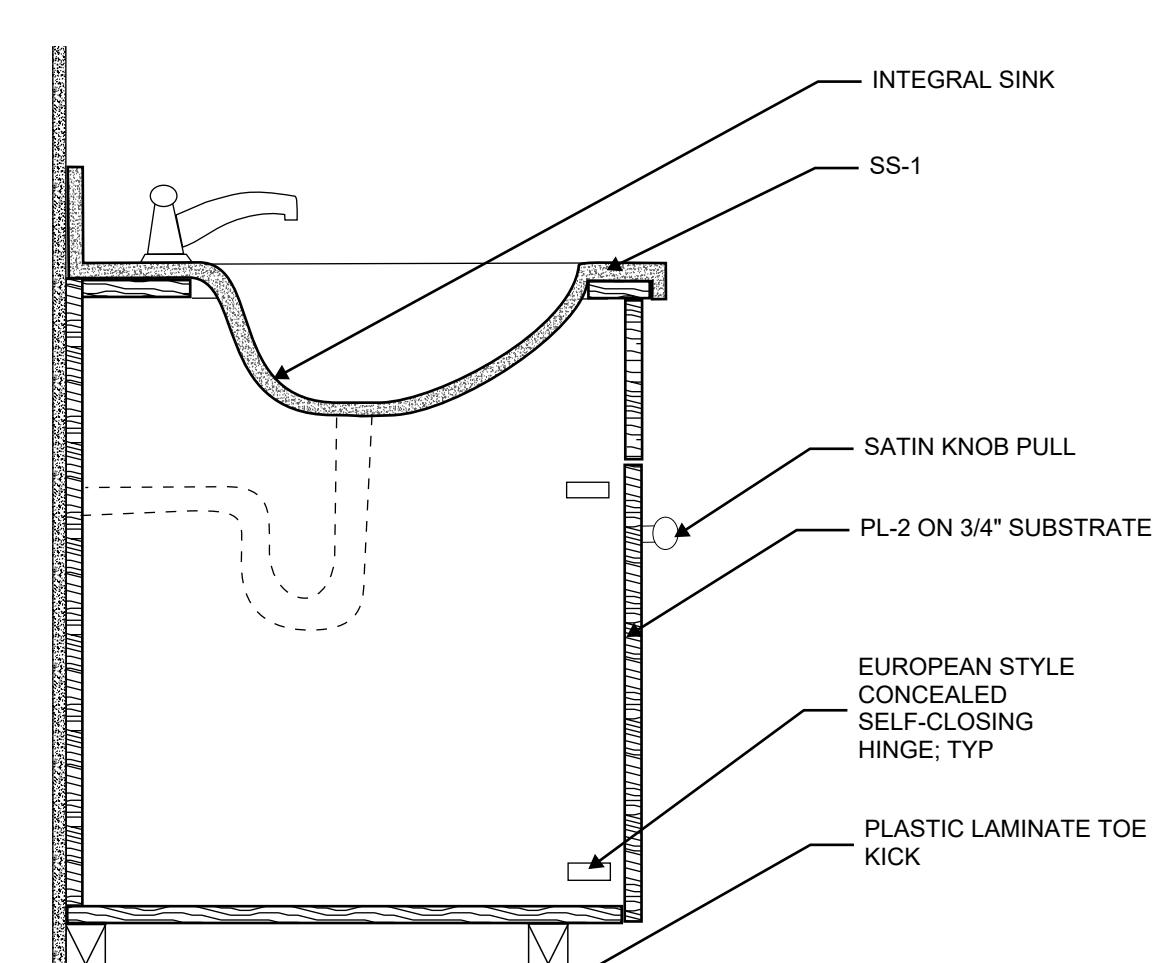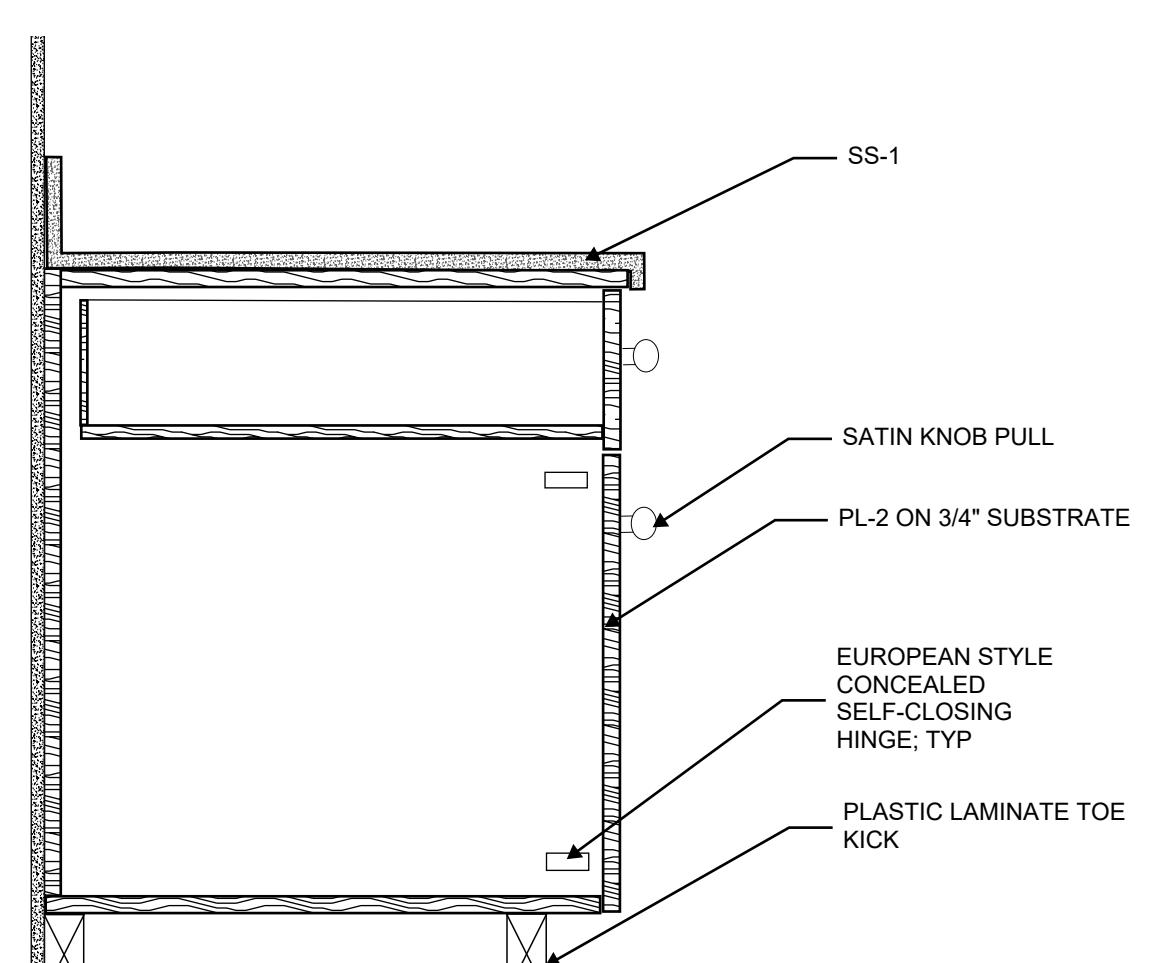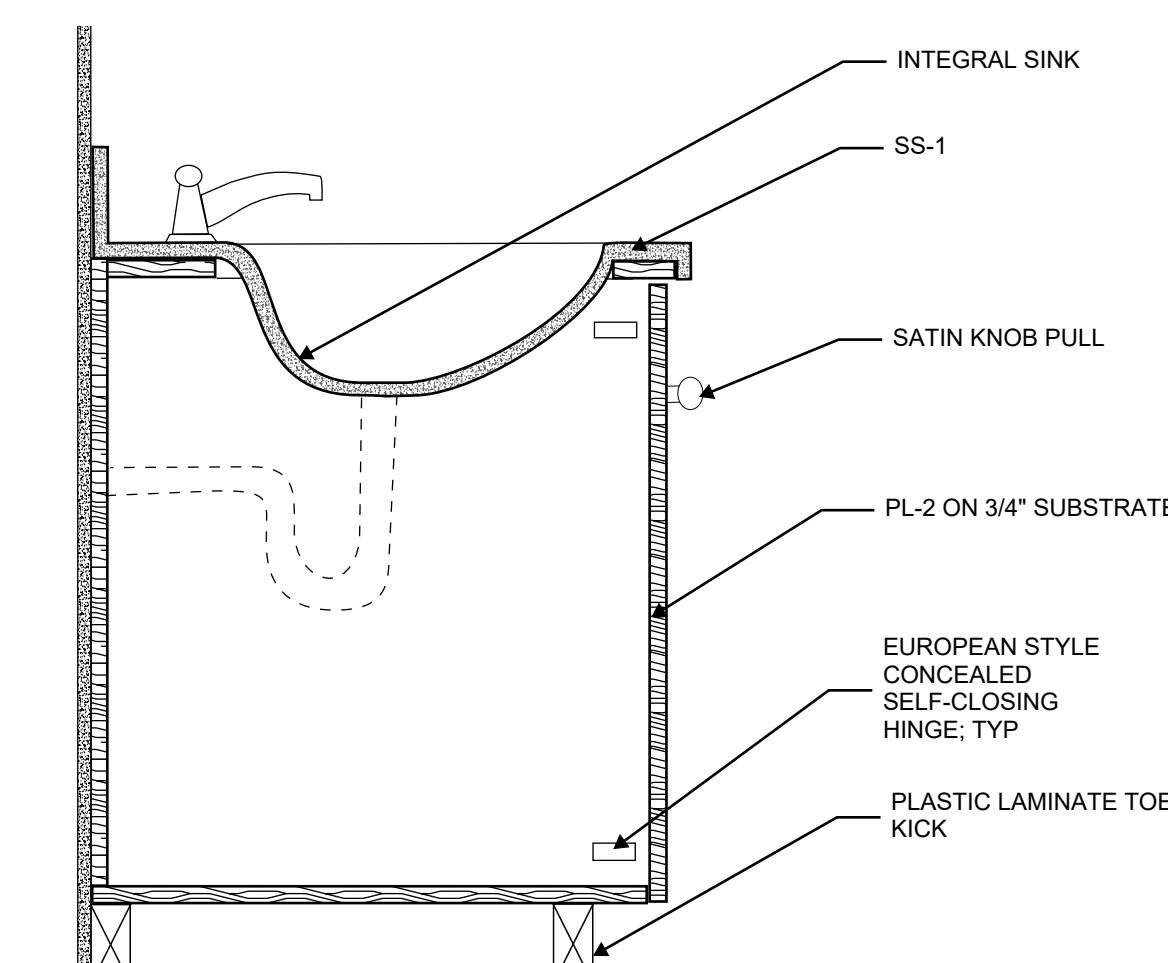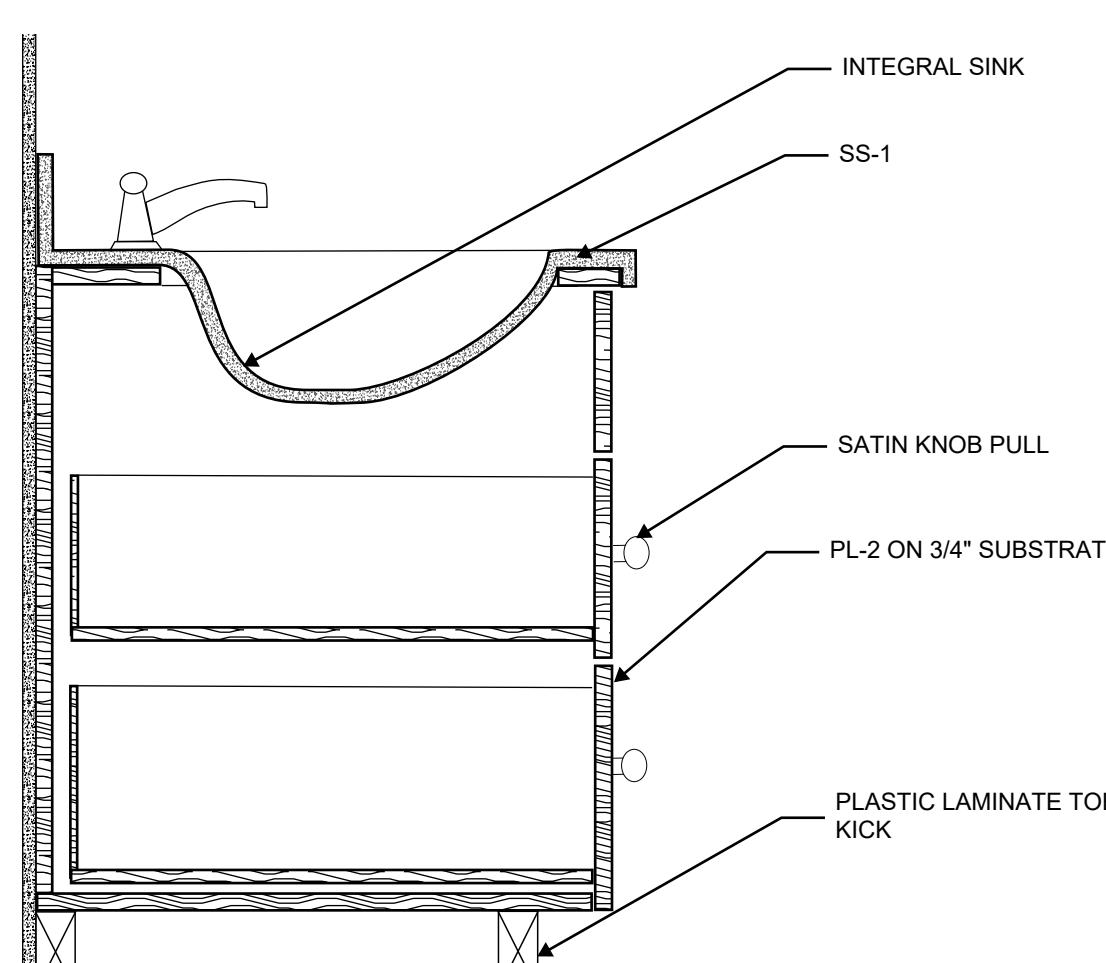

SECTION DETAIL - SINK DOUBLE
1 1/2" = 1'-0"

③ SECTION DETAIL - SINK DOOR
1 1/2" = 1'-0"

SECTION DETAIL - BATH SINK DOOR & DRAWER
1 1/2" = 1'-0"

① SECTION DETAIL - BATH SINK DOOR
1 1/2" = 1'-0"

SINGLE FAMILY HOUSE 4 BEDROOM 3.5 BATH

CIOFFI FAMILY

404 PEACHTREE CIRCLE
ATLANTA, GA 30318

Project number 2023.001
Issue Date 09.06.23

CONSTRUCTION DOCUMENTS


No.	Description	Date
-----	-------------	------

INTERIOR DETAILS

A900

Scale

As Indicated

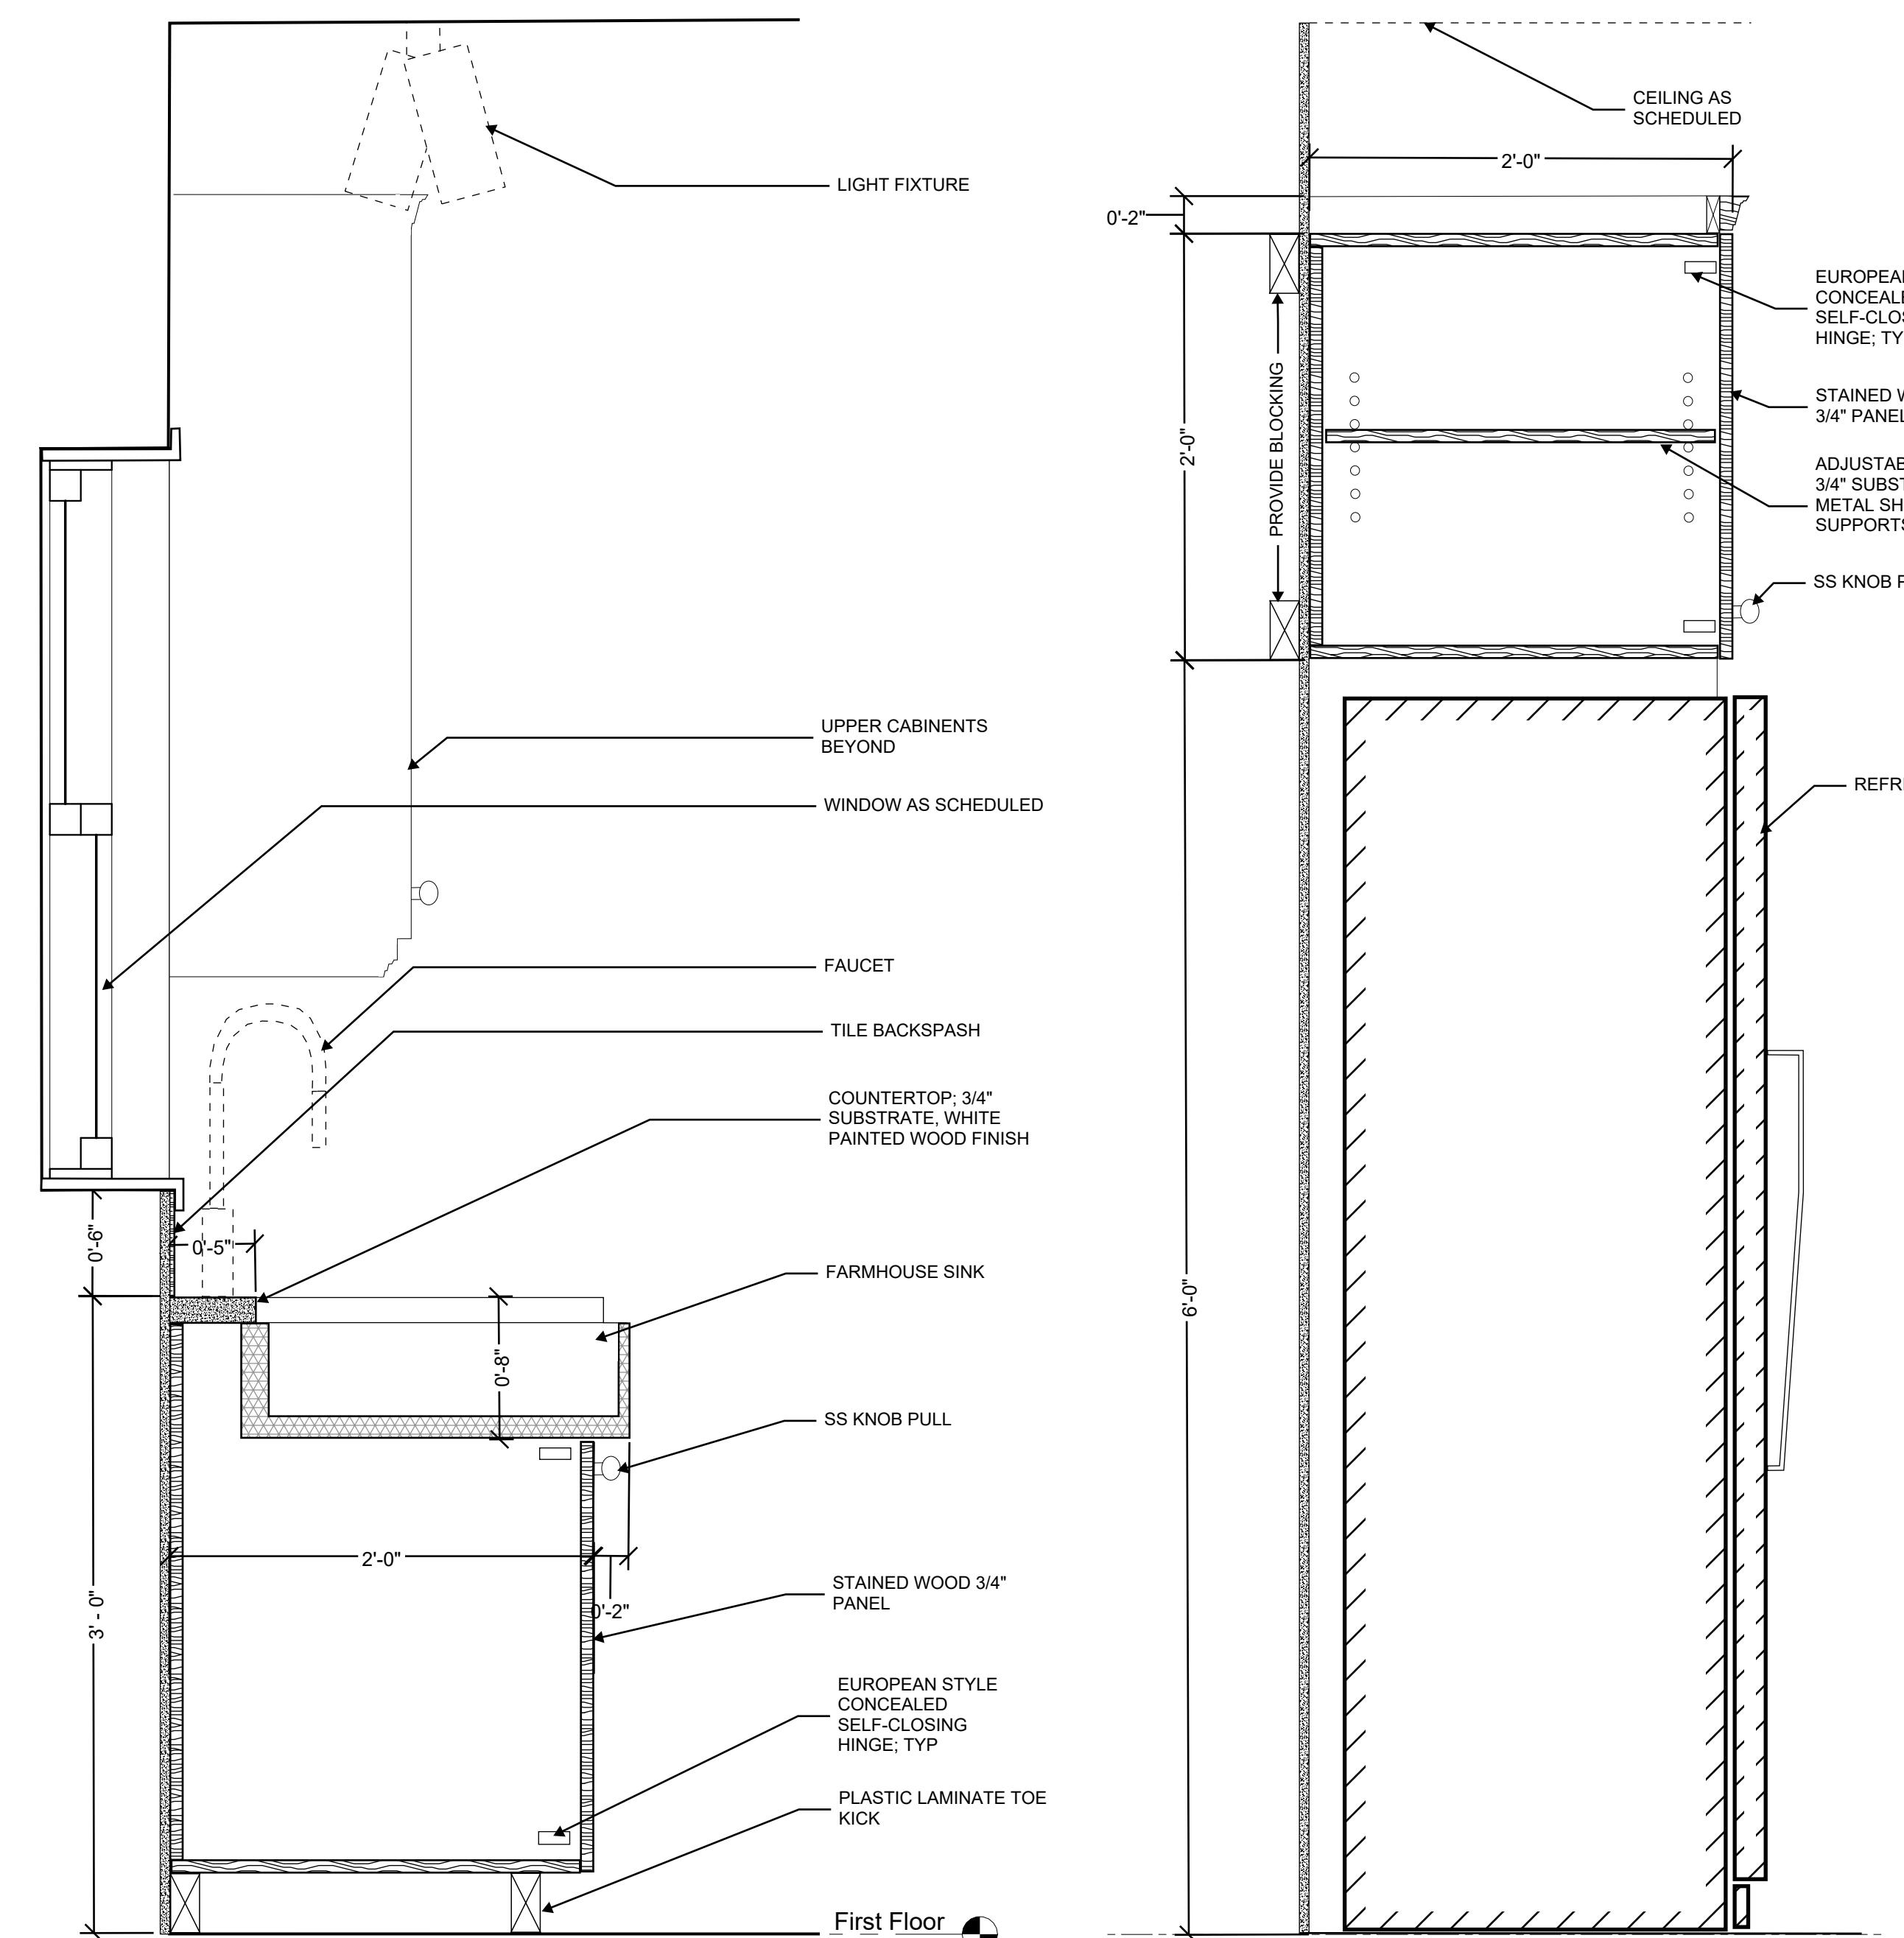


④ SECTION DETAIL - KITCHEN SINK
1 1/2" = 1'-0"

③ SECTION DETAIL - UPPER CABINET REF
1 1/2" = 1'-0"

SECTION DETAIL - UPPER CABINET
RANGE
1 1/2" = 1'-0"

② SECTION DETAIL - UPPER CABINET
1 1/2" = 1'-0"

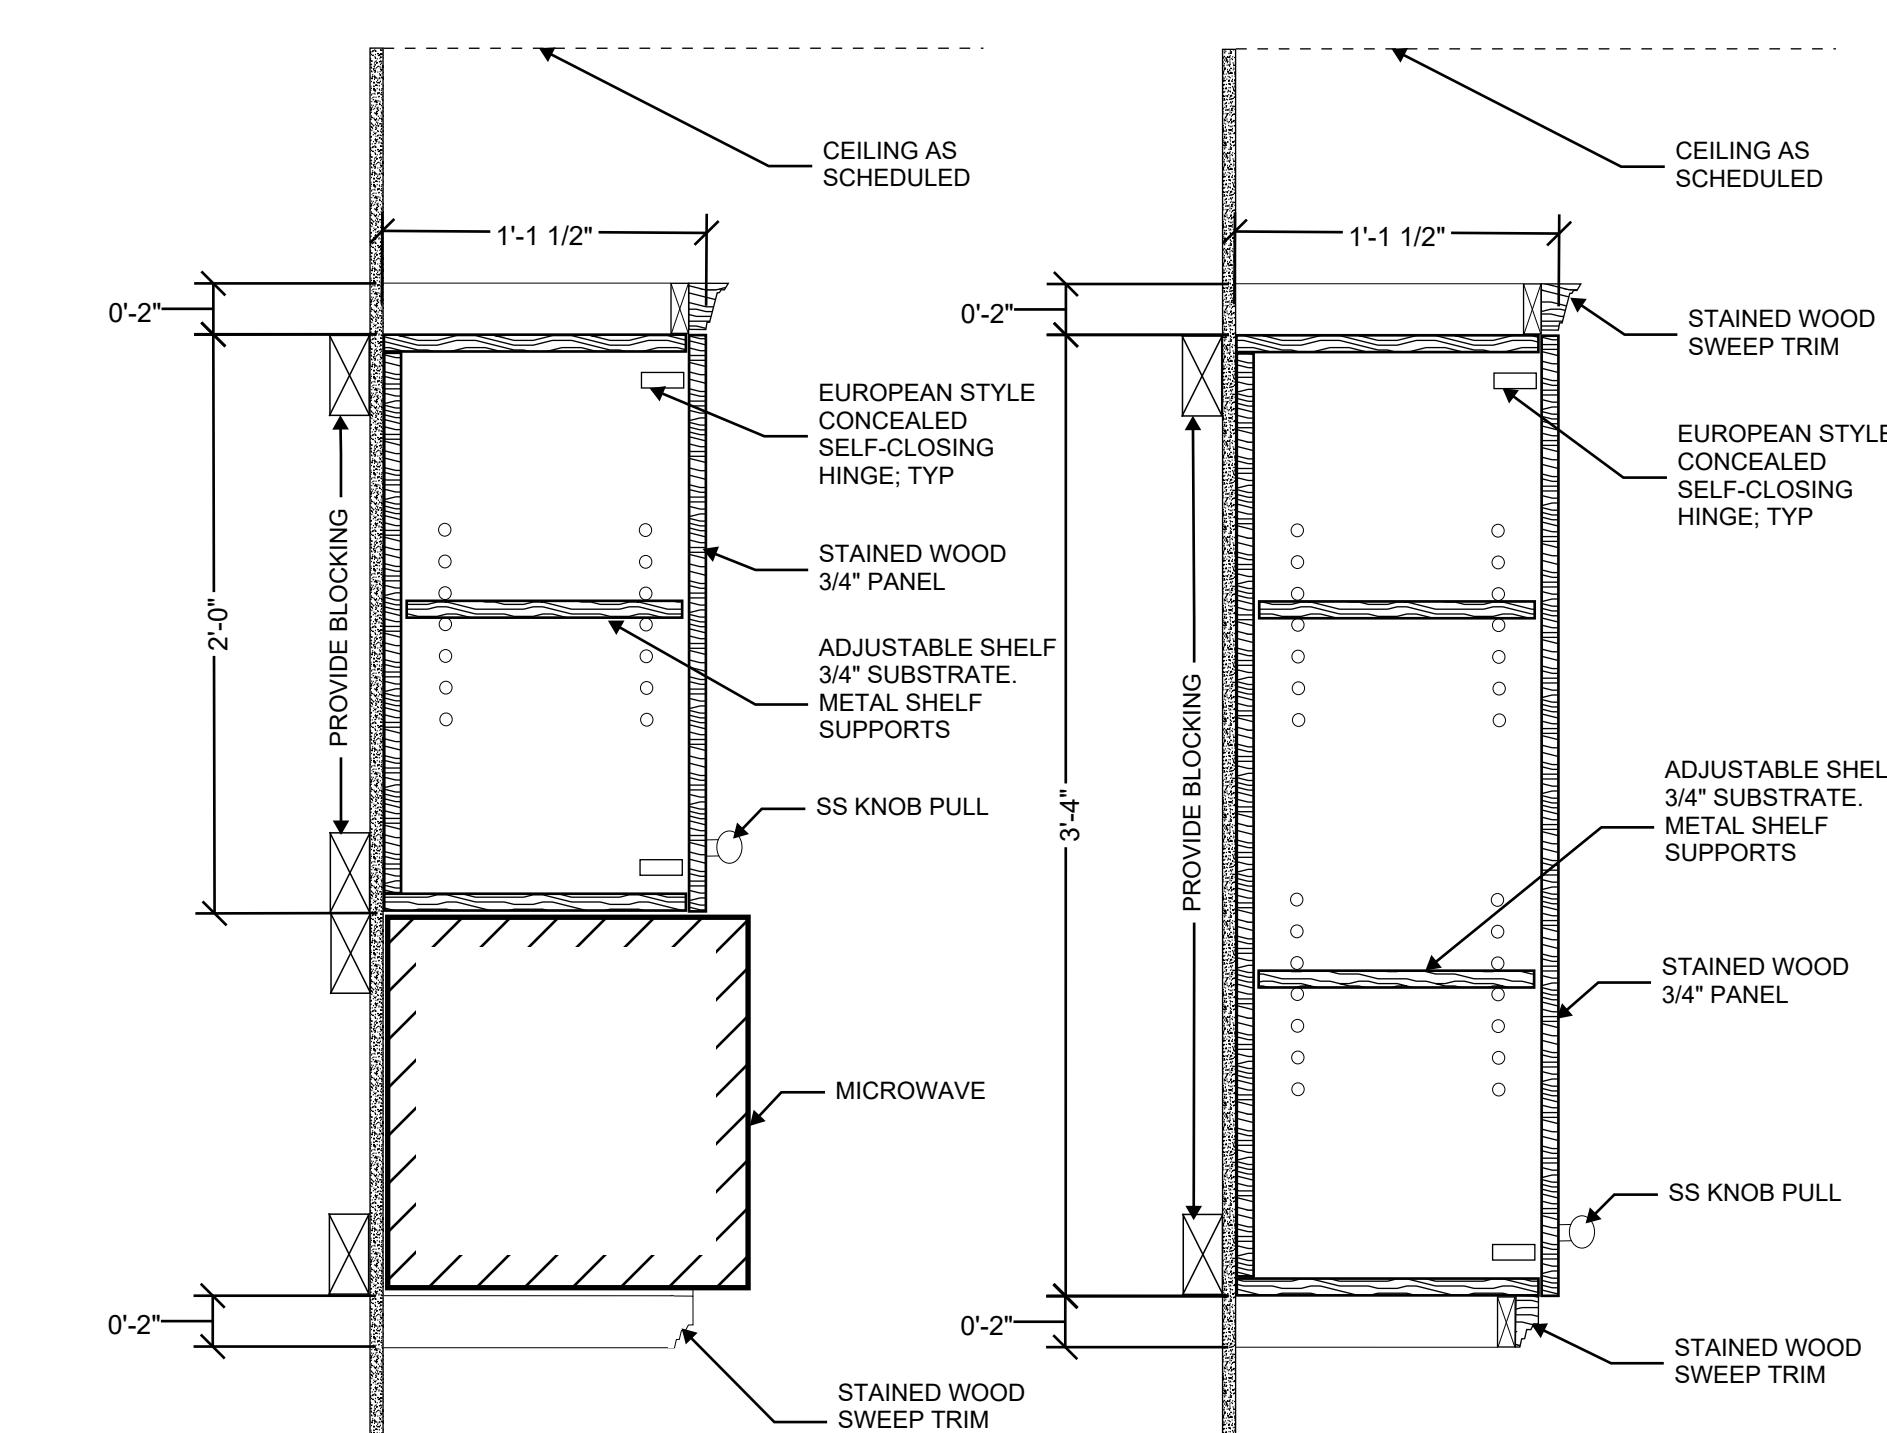

① SECTION DETAIL - UPPER CABINET
1 1/2" = 1'-0"

NOT FOR
CONSTRUCTION

SINGLE FAMILY HOUSE 4 BEDROOM 3.5 BATH

CIOFFI FAMILY
404 PEACHTREE CIRCLE
ATLANTA, GA 30318


Project number 2023.001
Issue Date 09.06.23

CONSTRUCTION DOCUMENTS

Revisions	No.	Description	Date
-----------	-----	-------------	------

INTERIOR DETAILS

A901

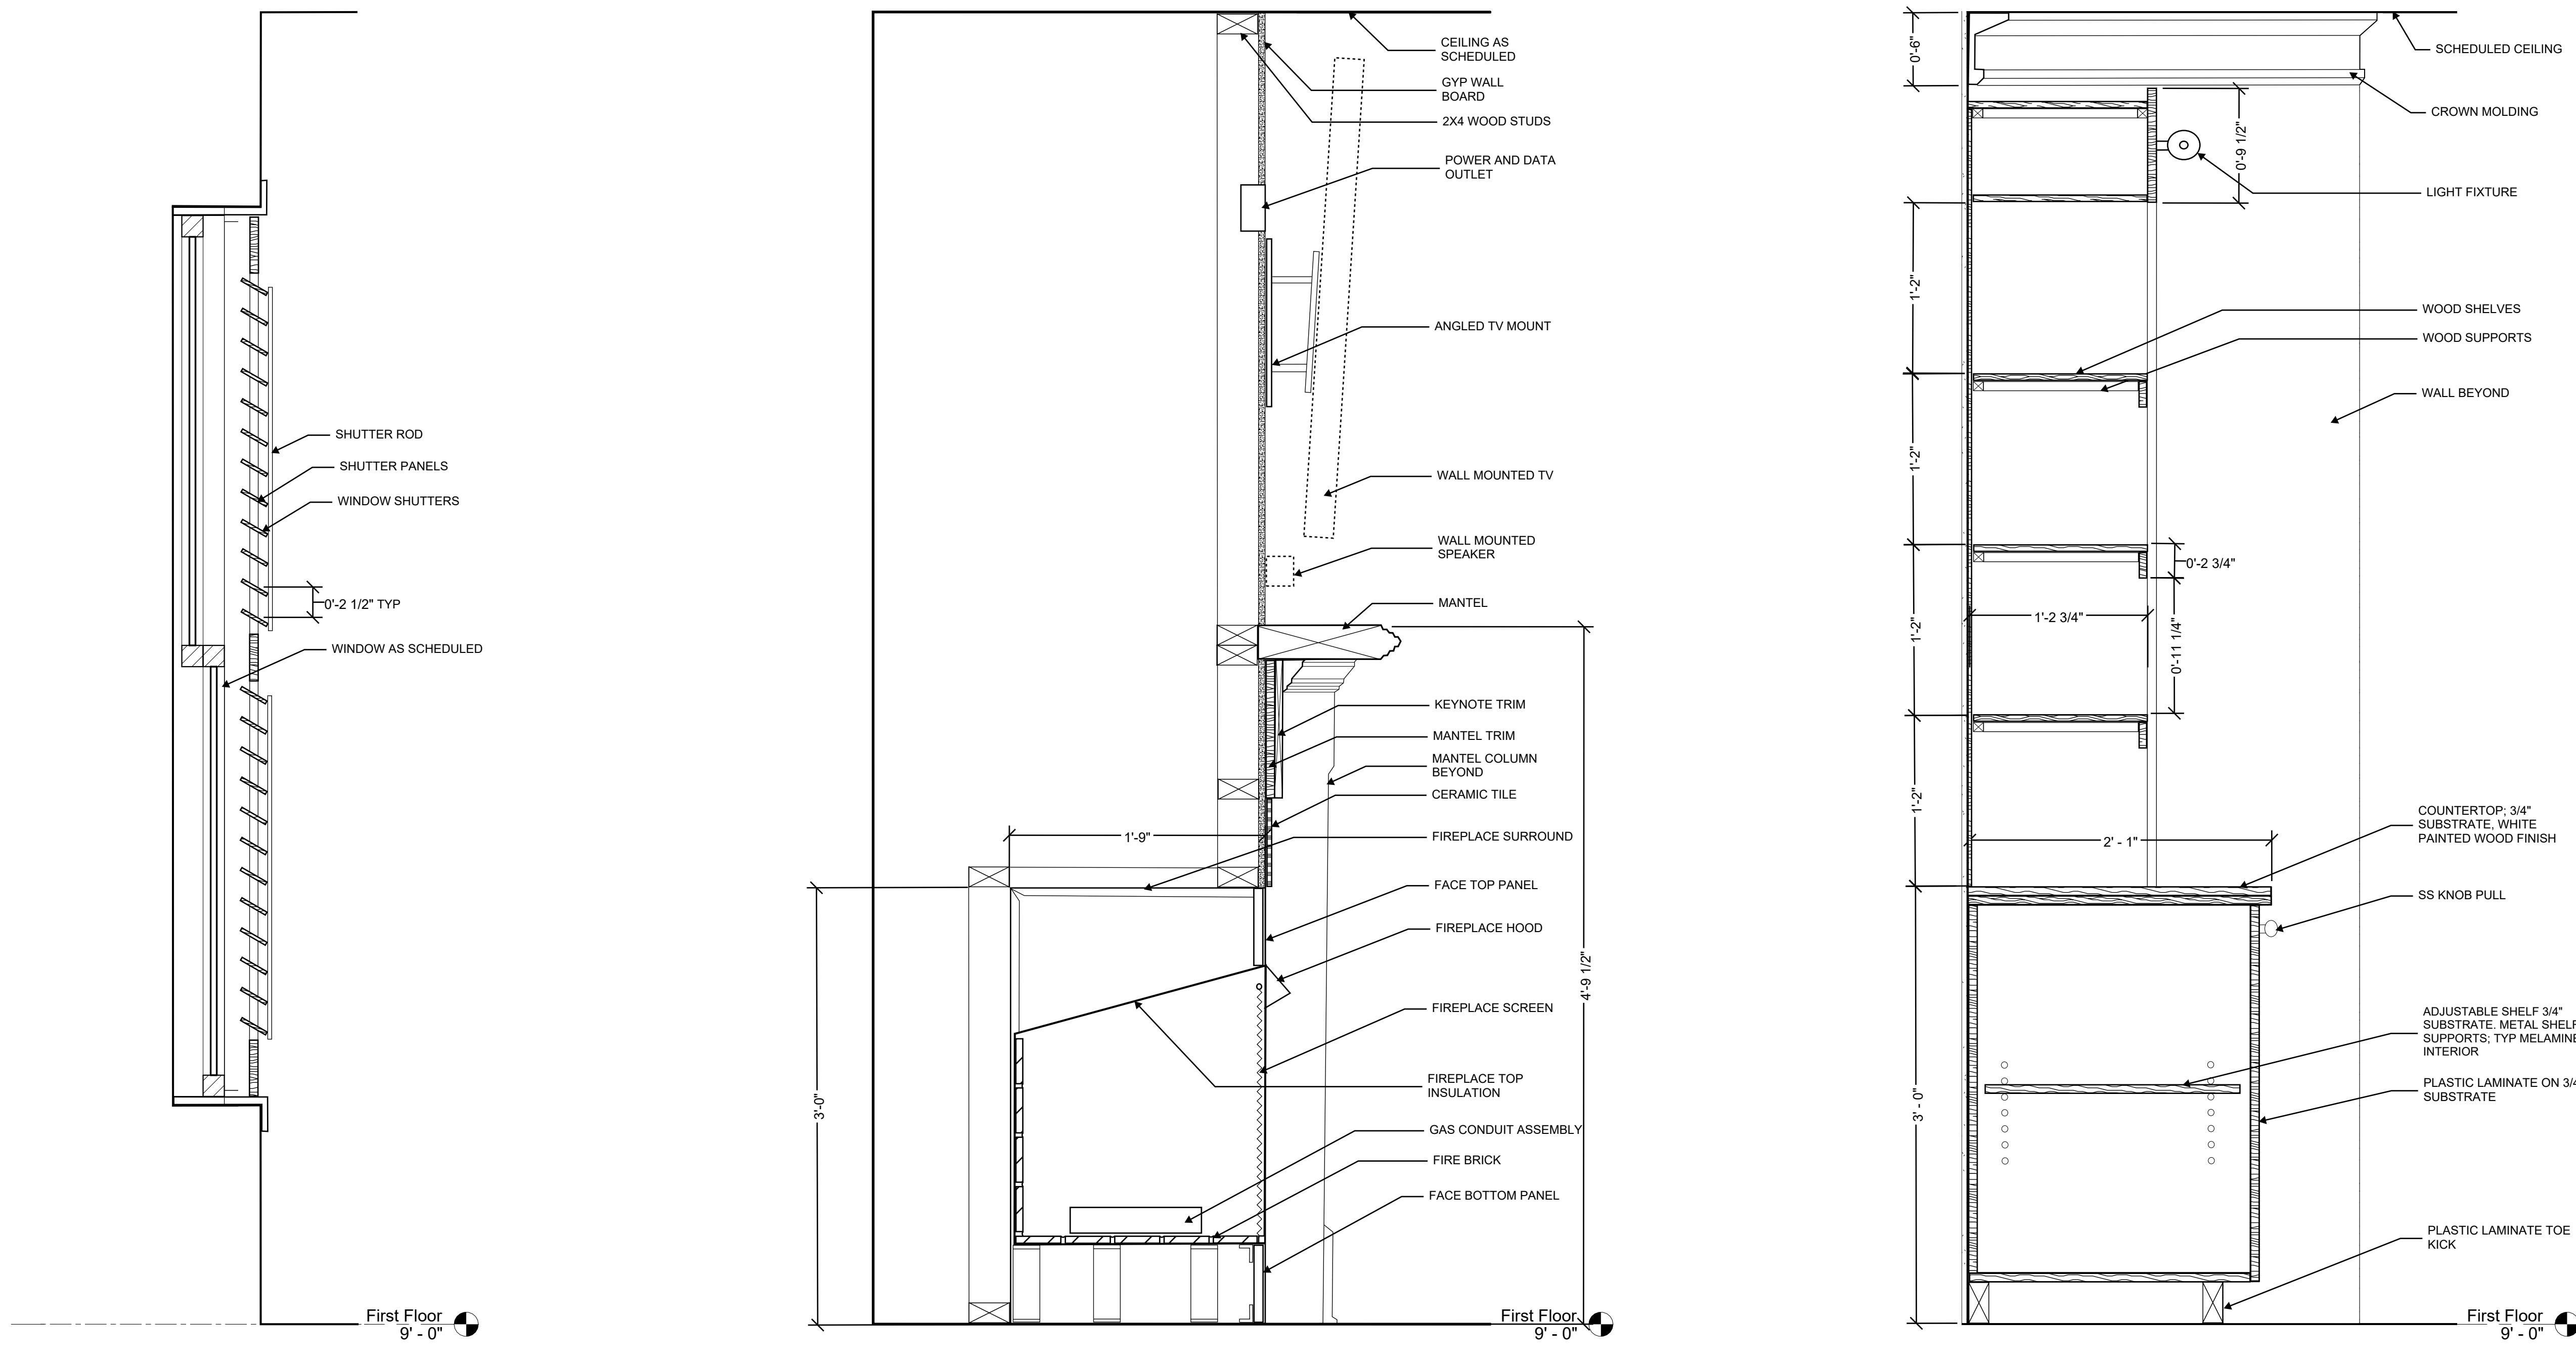


INTERIOR DETAILS

A902

Scale

As Indicated

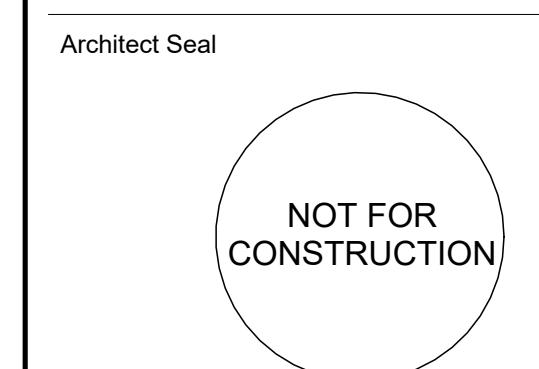

SINGLE FAMILY HOUSE 4 BEDROOM 3.5 BATH

CIOFFI FAMILY
404 PEACHTREE CIRCLE
ATLANTA, GA 30318

Project number 2023.001
Issue Date 09.06.23

CONSTRUCTION DOCUMENTS

No.	Description	Date
-----	-------------	------