




⑨ SECTION DETAIL - PORTICO ROOF CONNECTION
1 1/2" = 1'-0"

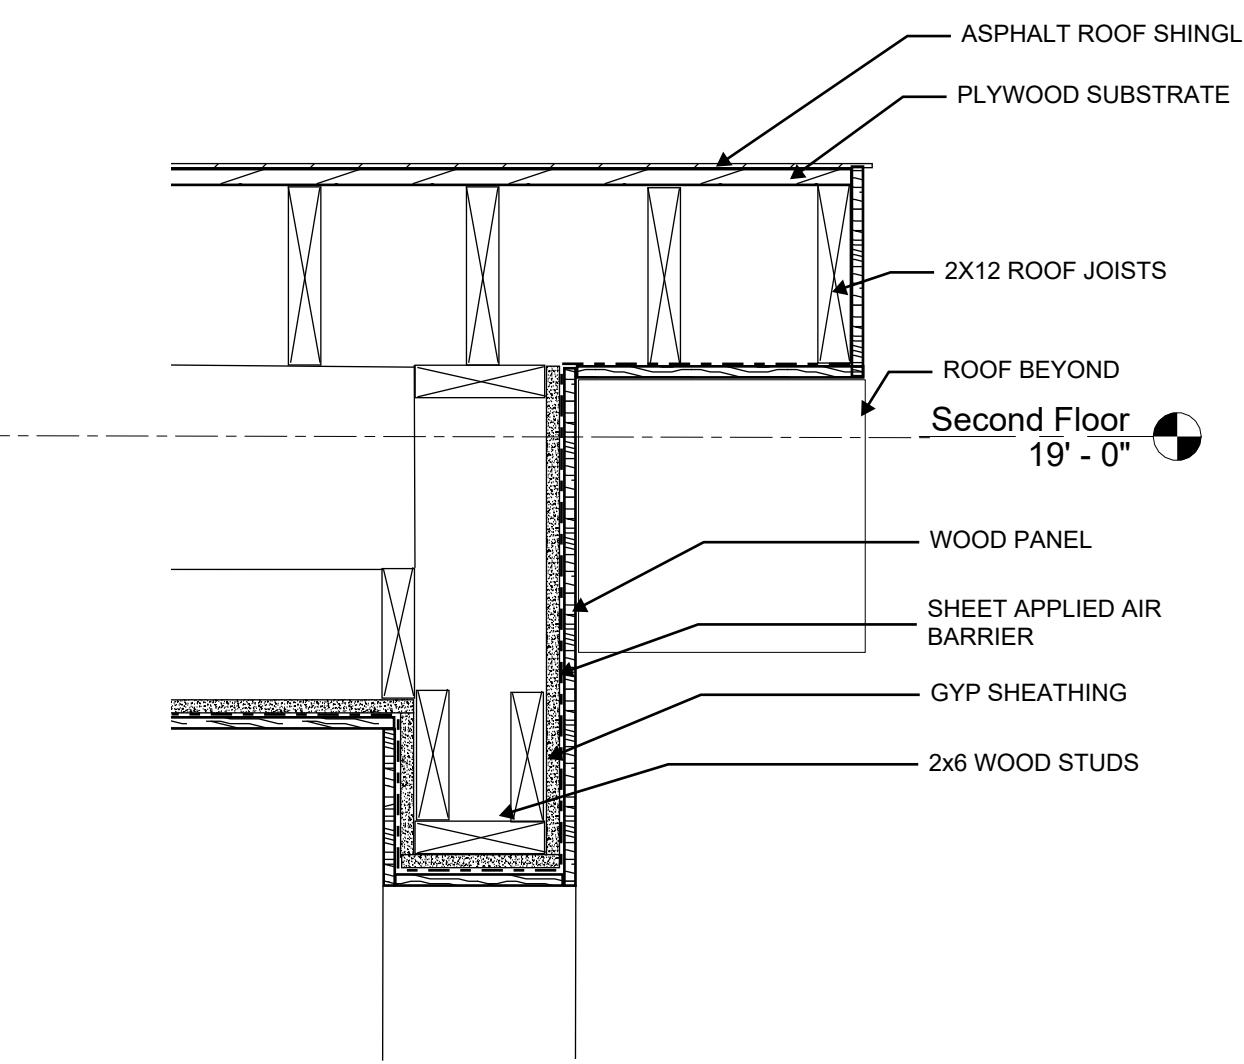


⑥ SECTION DETAIL - PORTICO ROOF
1 1/2" = 1'-0"

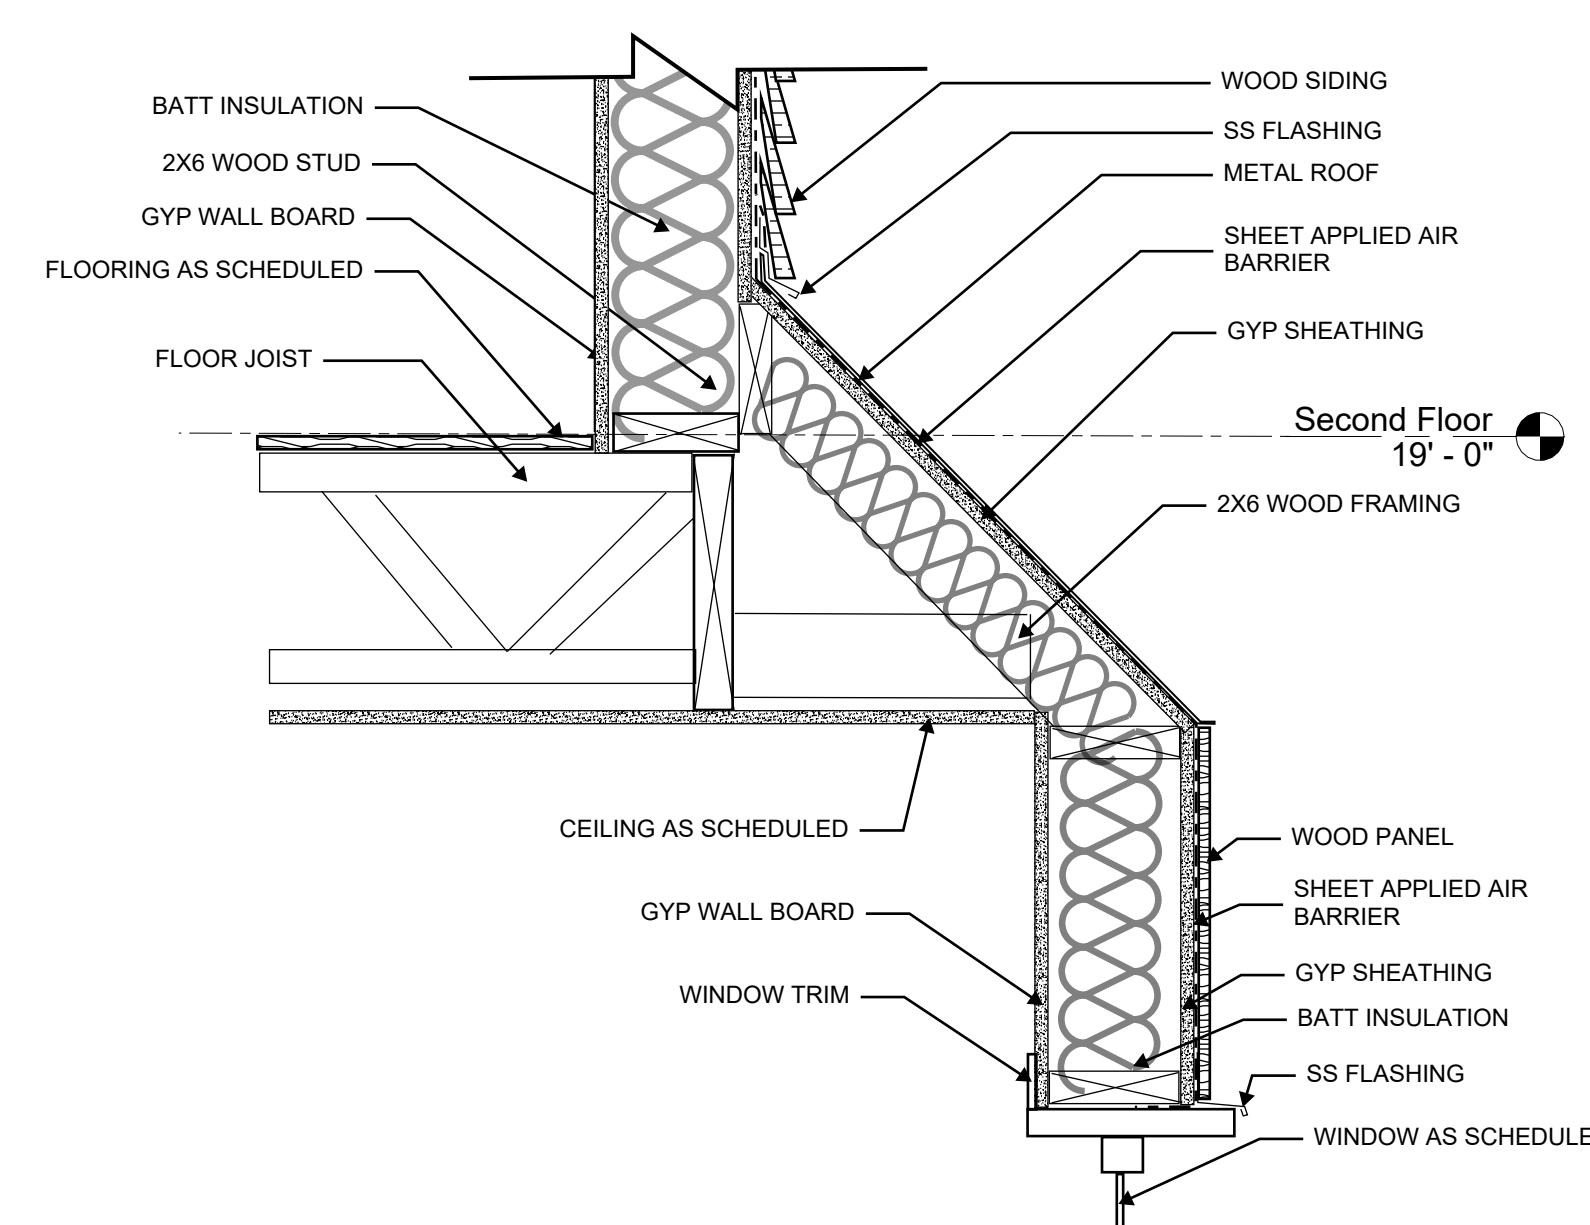


③ SECTION DETAIL - BAY WINDOW HEADER AND ROOF
1 1/2" = 1'-0"

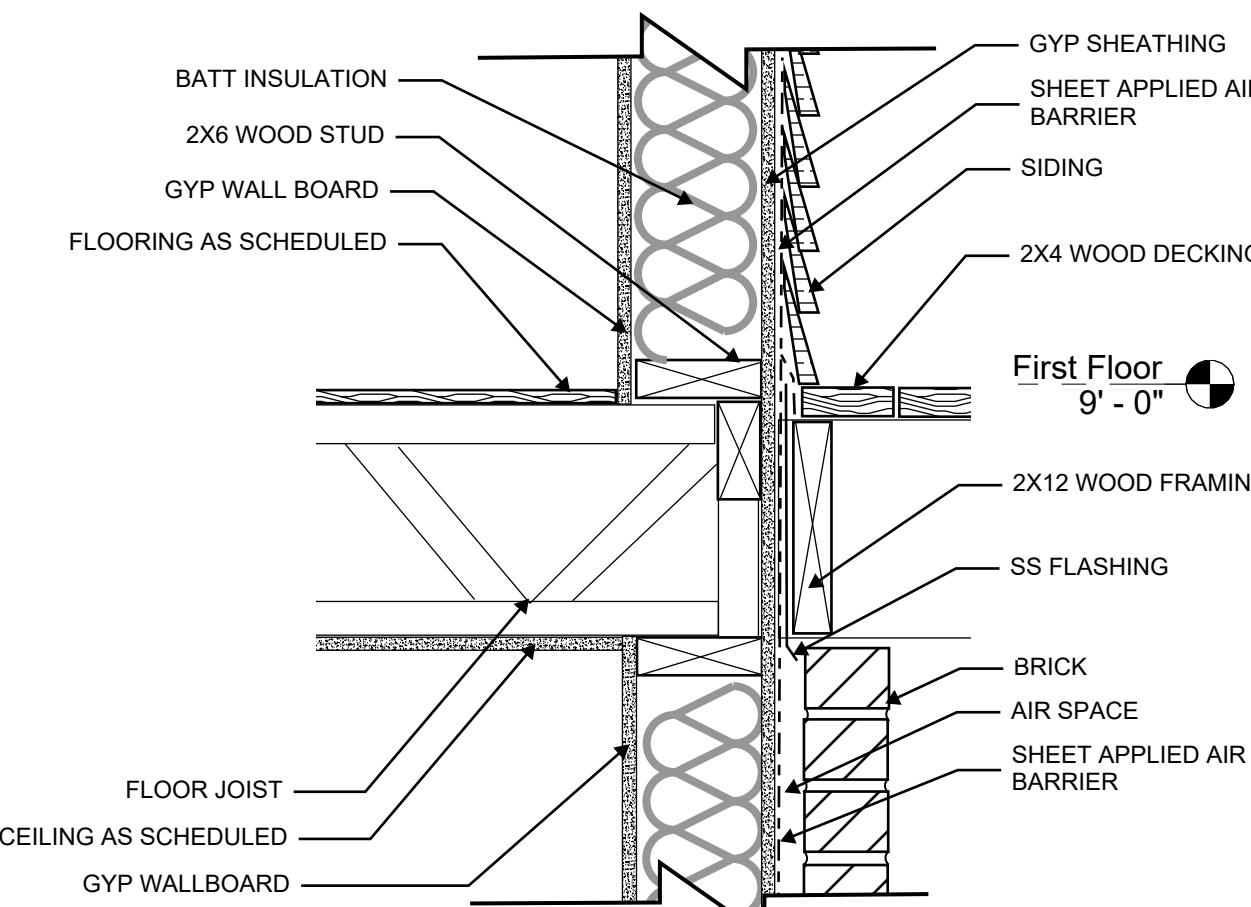


⑧ SECTION DETAIL - PORTICO FLOOR
1 1/2" = 1'-0"

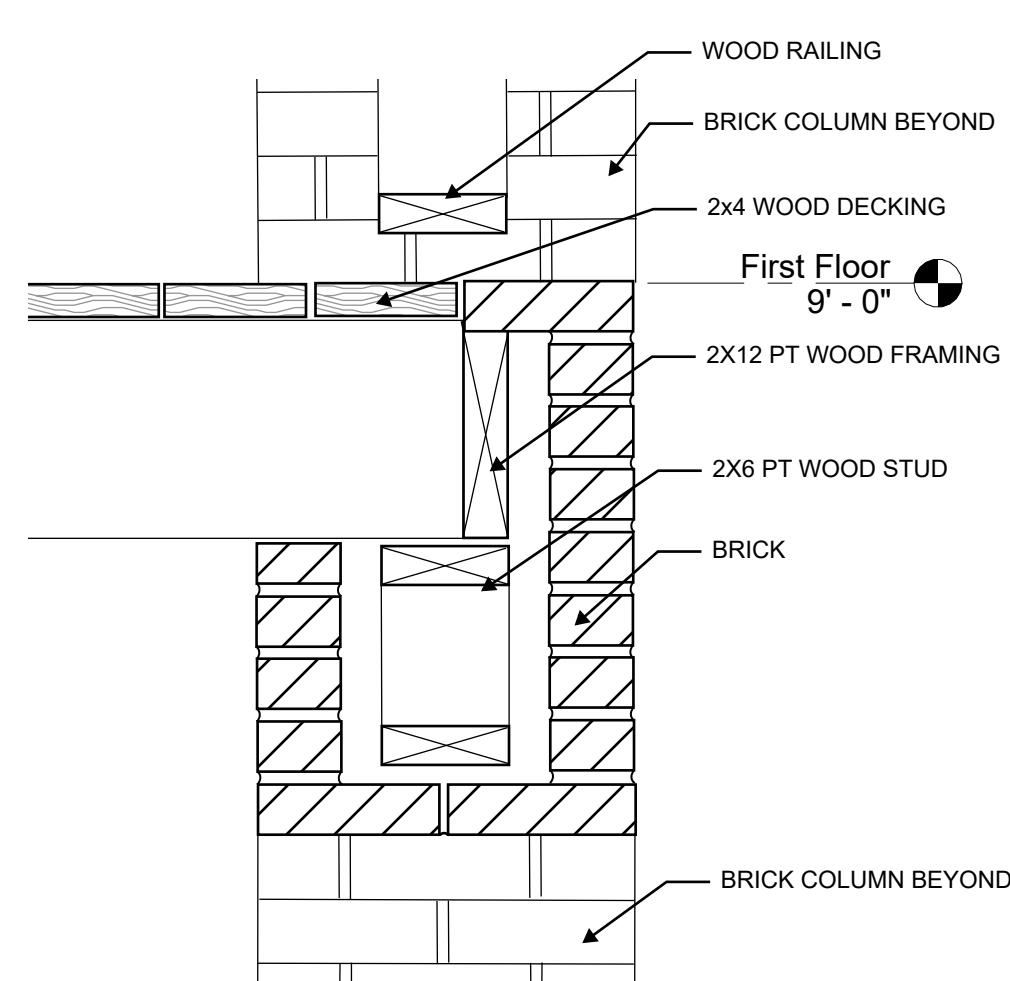


⑤ SECTION DETAIL - BRICK ARCH
1 1/2" = 1'-0"

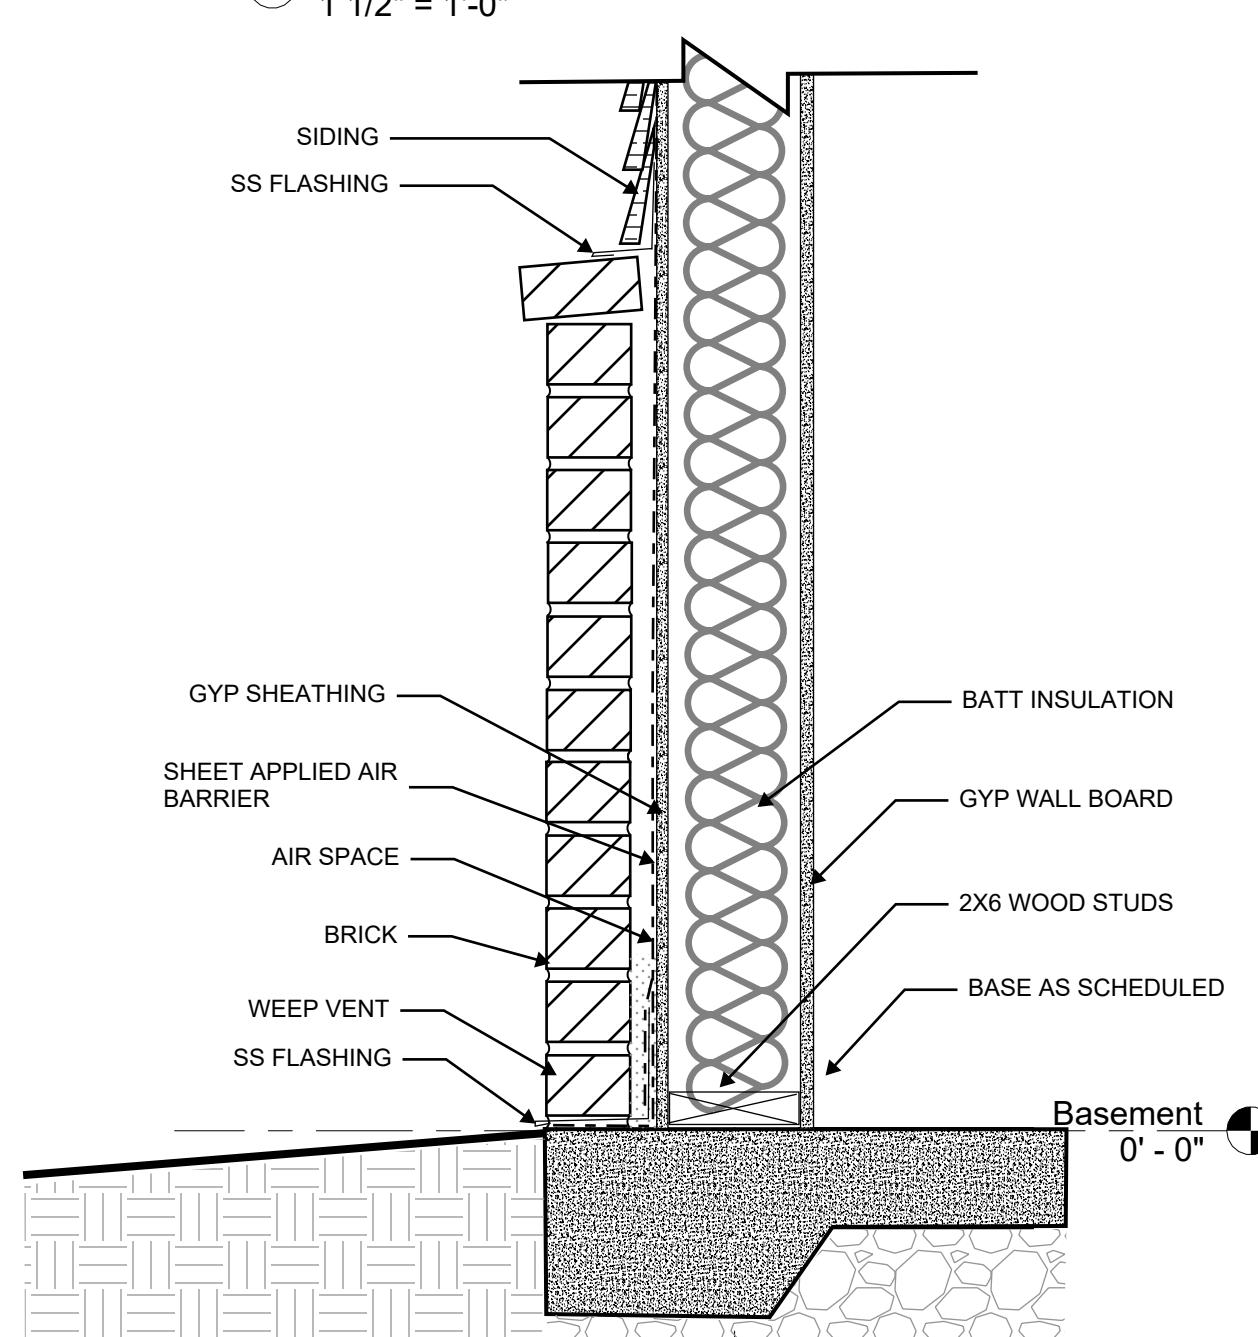


⑦ SECTION DETAIL - BRICK TO SIDING
1 1/2" = 1'-0"

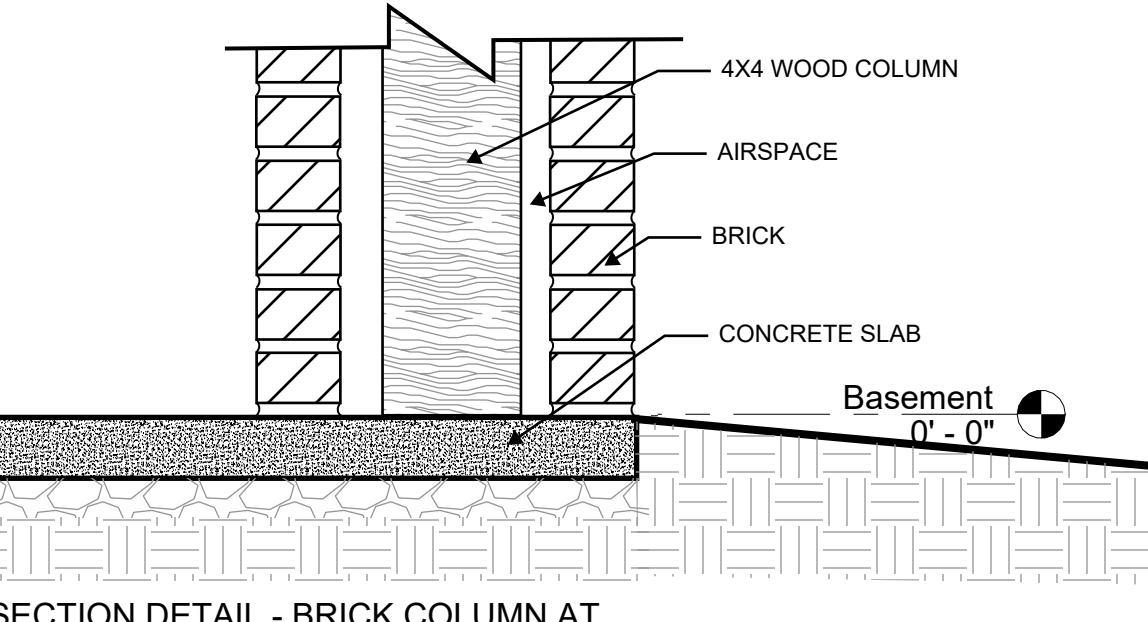

④ SECTION DETAIL - BRICK COLUMN AT GROUND
1 1/2" = 1'-0"

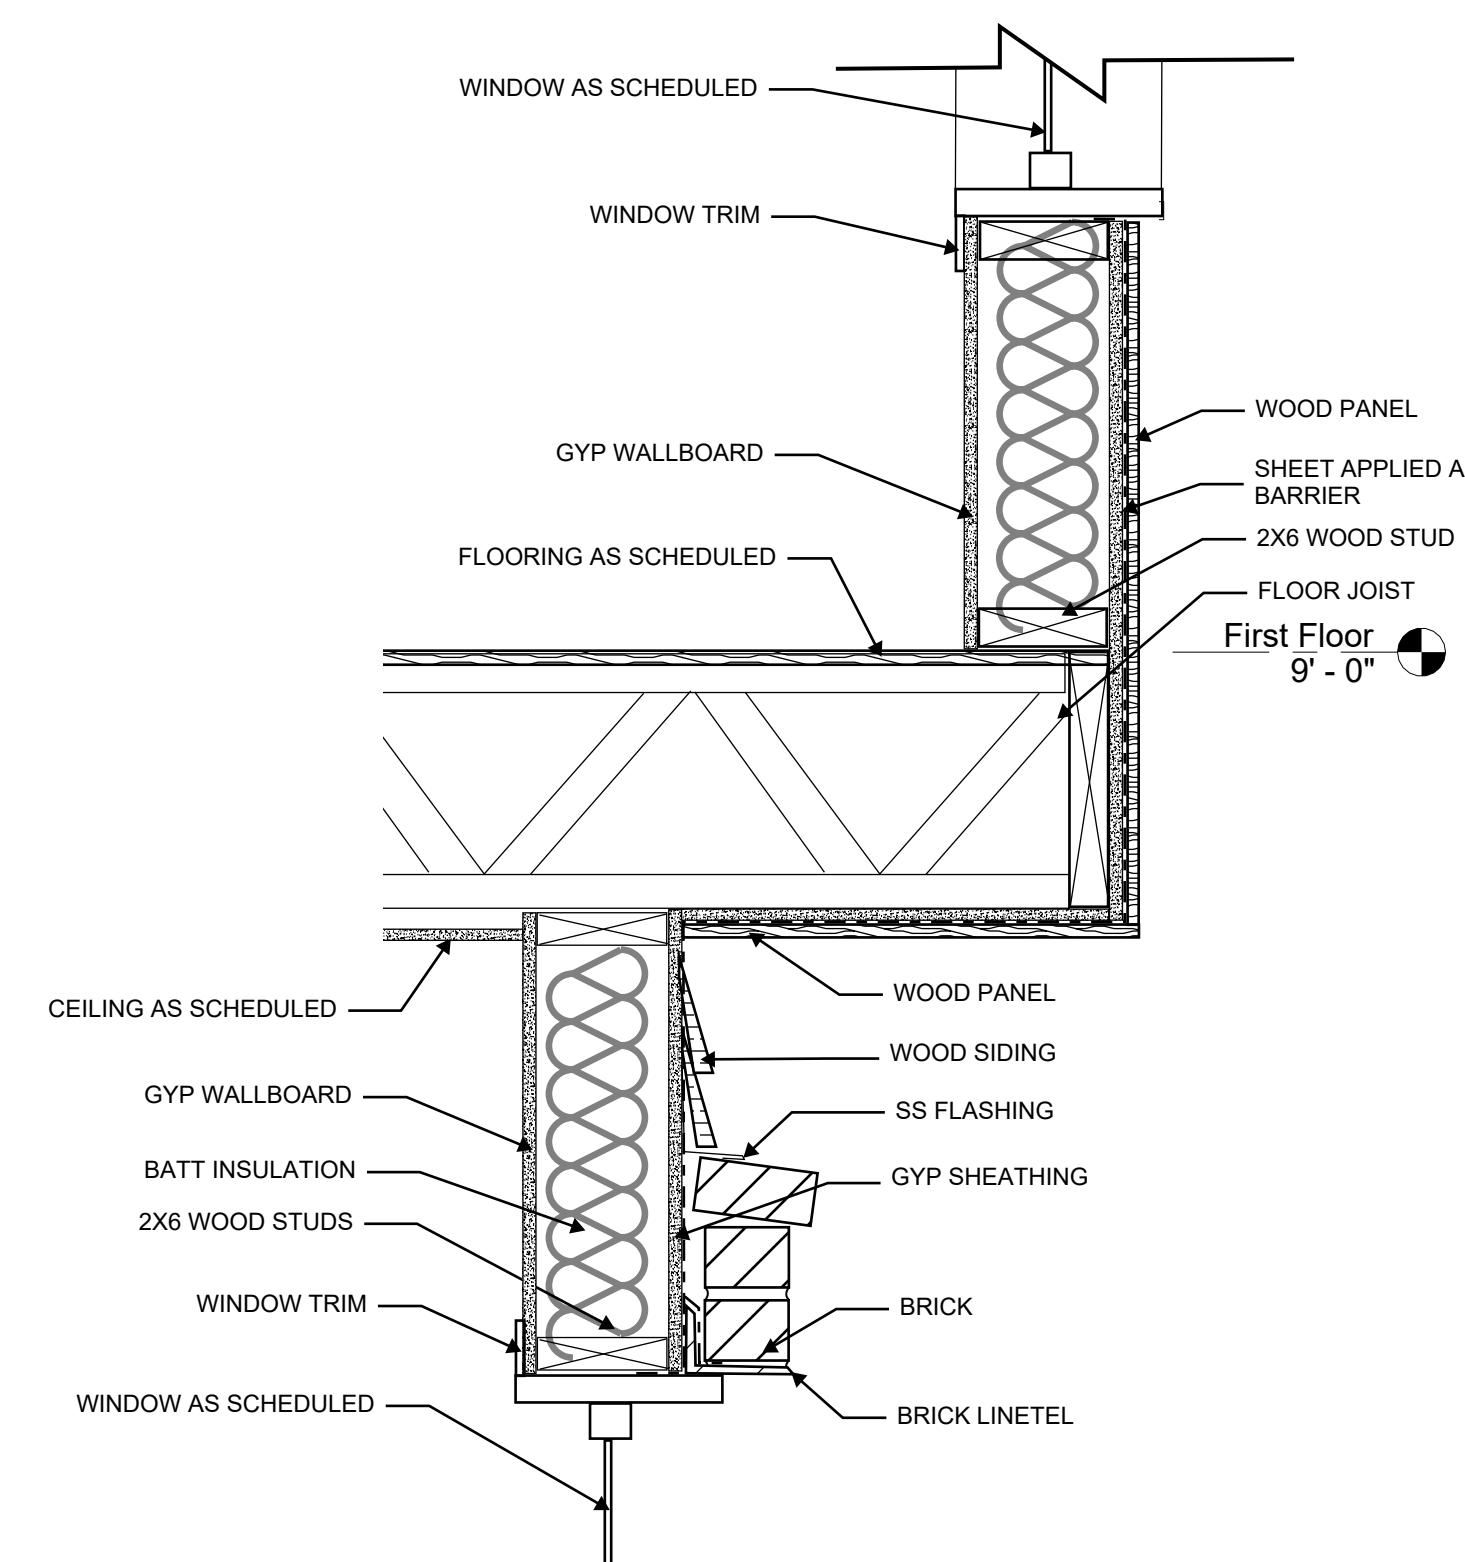

② SECTION DETAIL - WINDOW HEAD TO OVERHANG
1 1/2" = 1'-0"

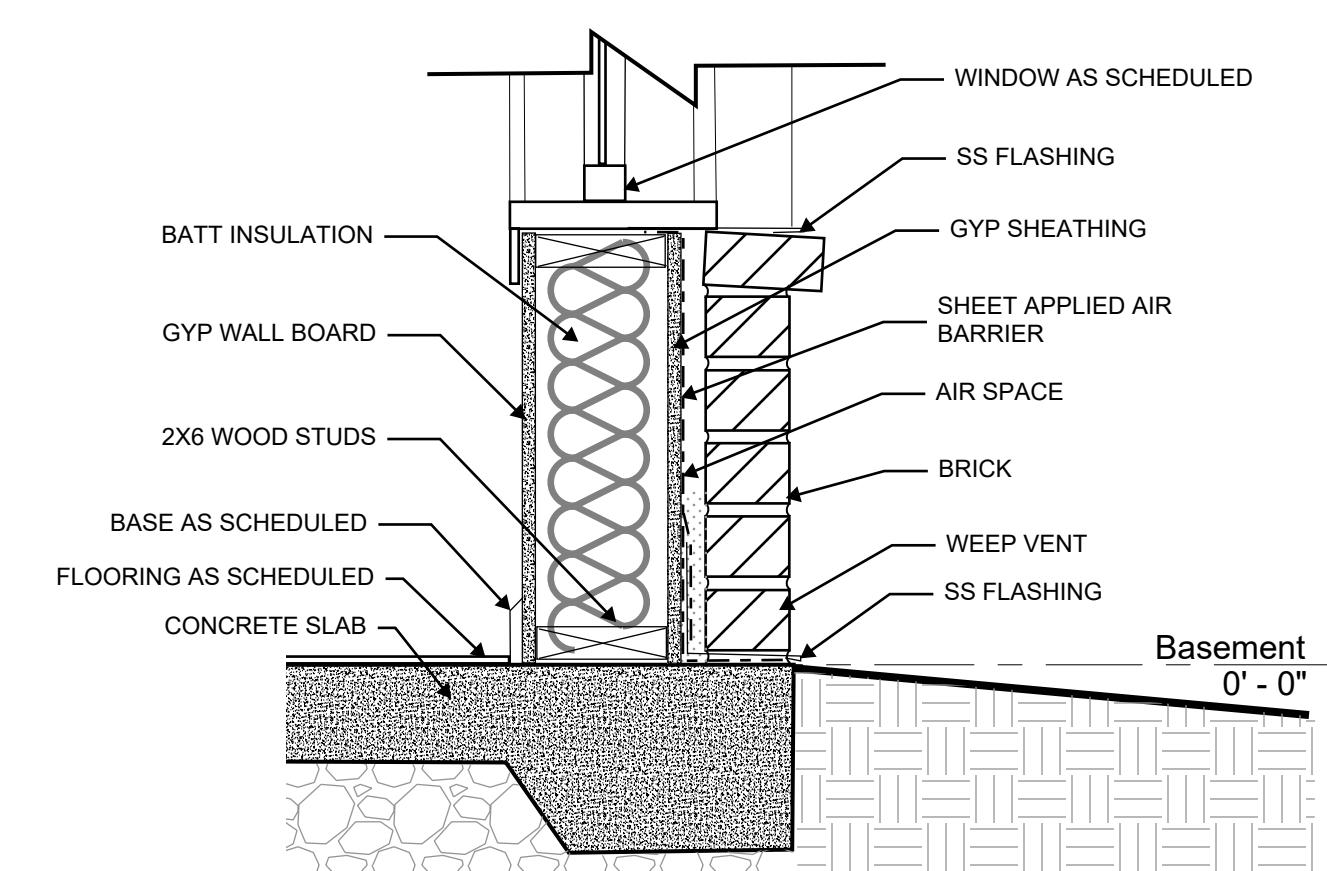

① SECTION DETAIL - WINDOW SILL BRICK
1 1/2" = 1'-0"

SINGLE FAMILY HOUSE
4 BEDROOM 3.5 BATH

CIOFFI FAMILY

404 PEACHTREE CIRCLE
ATLANTA, GA 30318

Project number 2023.001
Issue Date 09.06.23

CONSTRUCTION DOCUMENTS

Revisions
No. Description Date

SECTION DETAILS

A600